
## MAIN ROOF LAYOUT

GA BACKGROUND RETAINED | WRITTEN SURVEY DIMENSIONS GOVERN | FOR ENGINEER REVIEW

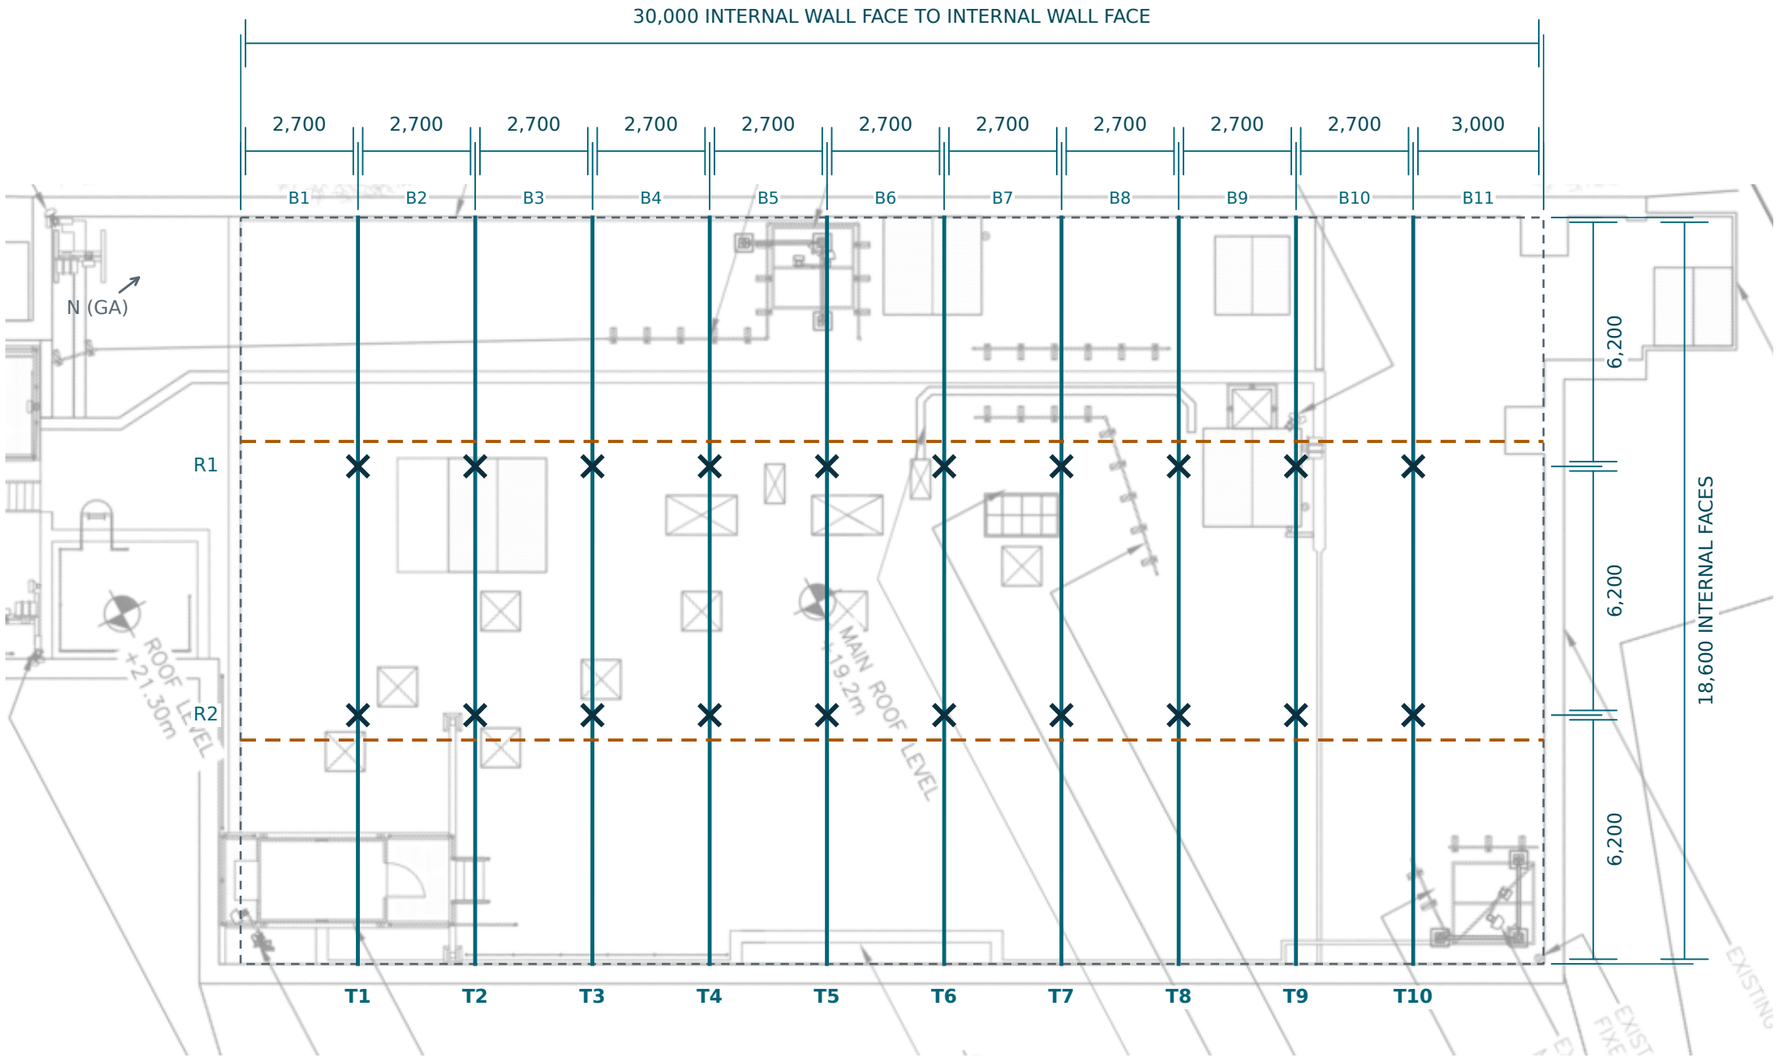


**MAIN RECTANGLE ONLY — STEPPED SECTIONS AT BOTH ENDS EXCLUDED**

**DIMENSION DATUM: WALLS = INTERNAL FACE; BEAMS / COLUMNS = CENTRELINE.**

Source: Survey Notes p3; client GA 200 Rev A (PDF p3); engineering lead clarifications. Stepped roof sections excluded.

**ALL DIMENSIONS IN mm UNLESS STATED OTHERWISE**

**NOTES:**

1. Main rectangular roof only. Stepped sections at both ends excluded.

2. Wall dimensions refer to internal faces; beam and column dimensions refer to centrelines.

3. Transverse beam ends assumed to bear at external walls. End support details and wall-position beams unverified.

4. Longitudinal beams shown continuous for sketch. Exact positions, sizes and end details unverified; no direct column connection.

5. Diagrammatic annotation on client GA. Do not scale or use for setting out. For engineer review; not for construction.

**STRUCTURAL MEMBER KEY**

- Steel columns (20)
- Transverse steel beams T1-T10
- Longitudinal steel beams Position schematic; size unverified
- Wall / scope reference Not a confirmed beam

T = beam ID; R = column row; B = bay.

| | | | | |
|---|---|---|---|---|
| | | | | |
| | | | | |
| | | | | |
| P04 | FORMAT + KEY | AT | AF | 21-10-2026 |
| Rev: | Issue: | Drawn: | Chkd: | Date: |

Consultant:

KA ENGINEERING GROUP

Client:

JET network solutions

Job Title:

STRUCTURAL SLAB SCAN

Drawing Title:

MAIN ROOF LAYOUT

Address:

ASMER HOUSE
ASH STREET
LEICESTER, LEICESTERSHIRE
LE5 0DA

| Drawn By: | Checked By: |
|---|---|
| AT | AF |

| Scale at A3: | Date (reference sheet): |
|---|---|
| NTS / DO NOT SCALE | 14-10-2026 |

| Project No: | Drawing No: | Rev: |
|---|---|---|
| 7015 | 01 | P04 |