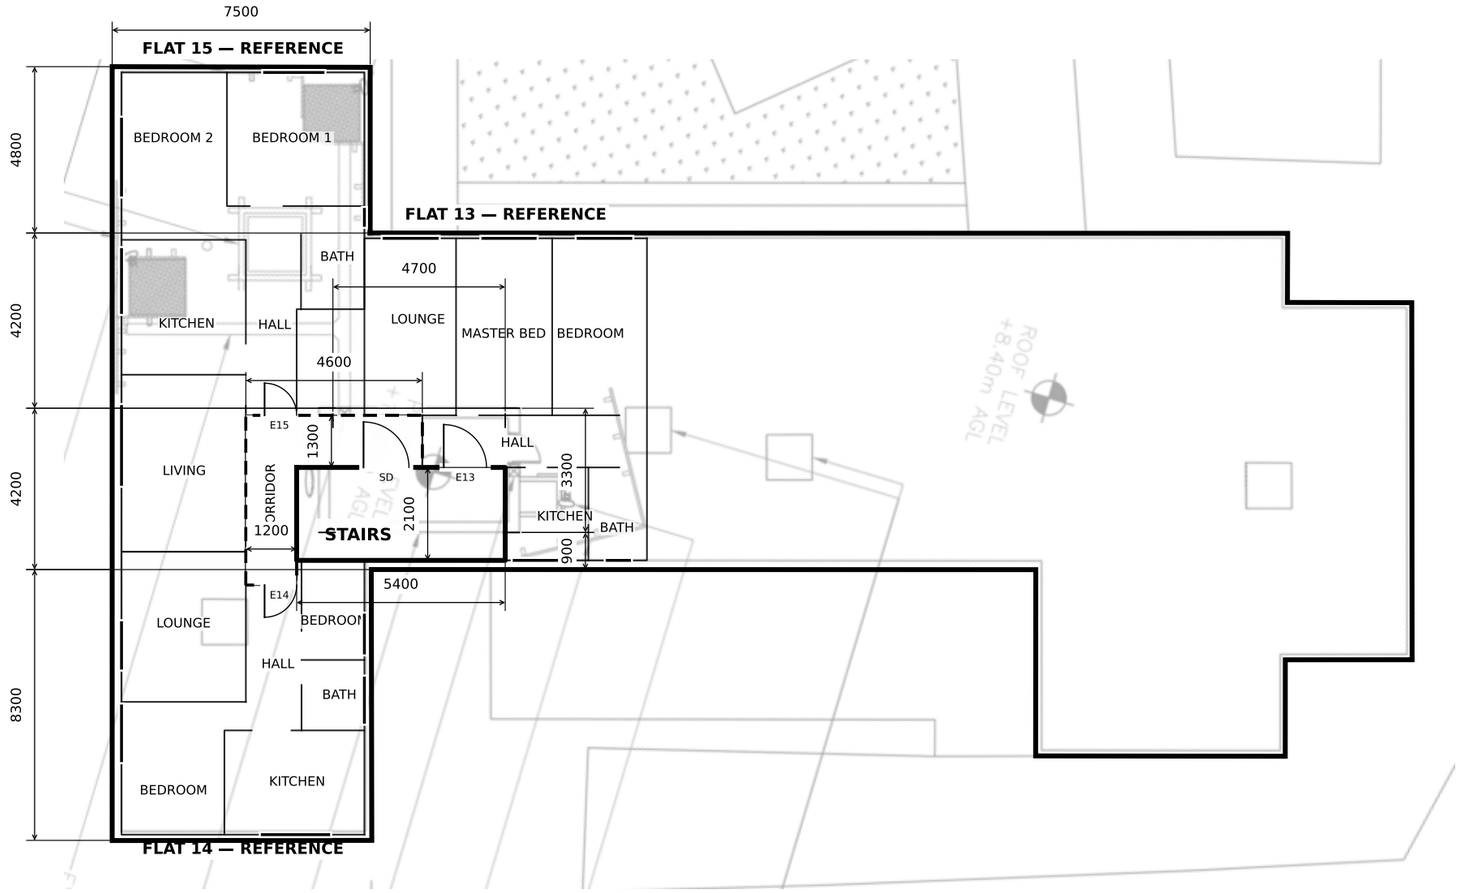


ALL DIMENSIONS IN mm. DIMENSION EXTENSIONS IDENTIFY THE REFERENCE FACES. DO NOT SCALE.

ALL DIMENSIONS IN mm UNLESS STATED OTHERWISE

NOTES:

1. Top-floor flats 13-15 were inaccessible. Apartment plans are third-party references, not surveyed structure.

2. Written survey dimensions govern. Apartment partitions are approximate graphic references. Do not scale.

3. Plant room is above the flat/stair layout. Its face marks identify dimension references. Door/window sizes and swings schematic.

4. Plant-room wall thickness: 280 mm.

STRUCTURAL MEMBER KEY

- Load-bearing walls — External boundary and stairs
- Non-load-bearing corridors
- Apartment reference partitions — Structural status unverified

01	FIRST ISSUE	AT	AF	23-10-2026
Rev:	Issue:	Drawn:	Chkd:	Date:

Consultant:

KA ENGINEERING GROUP

Client:

CONNECT

Job Title:

ROOF STRUCTURAL SURVEY

Drawing Title:


Roof Support Layout

Address:


HONEYPOT HALL
HAROLD ROAD
CLACTON-ON-SEA, ESSEX
CO15 6AL

Drawn By:	Checked By:
AT	AF
Scale at A3:	Date (reference sheet):
NTS / DO NOT SCALE	23-10-2026


Project No:	Drawing No:	Rev:
7111	7111-01	01

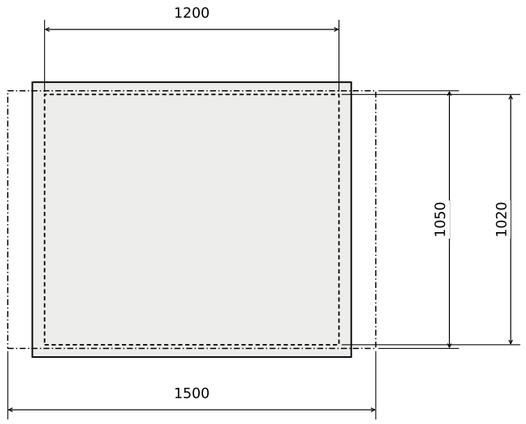


1 PLAN 1:25

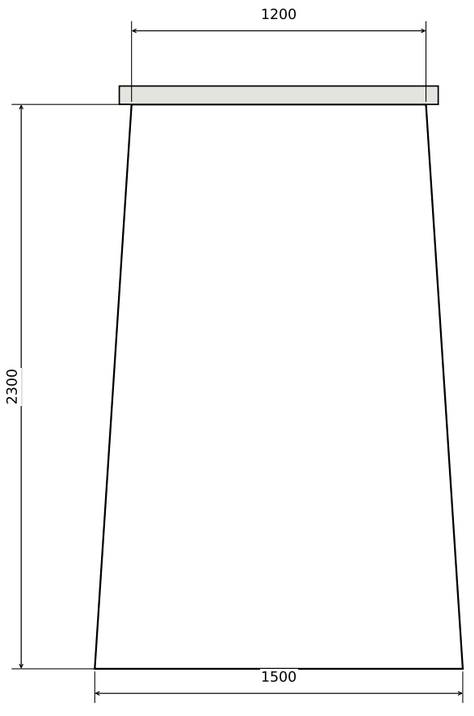

2 X-FACE ELEVATION 1:25

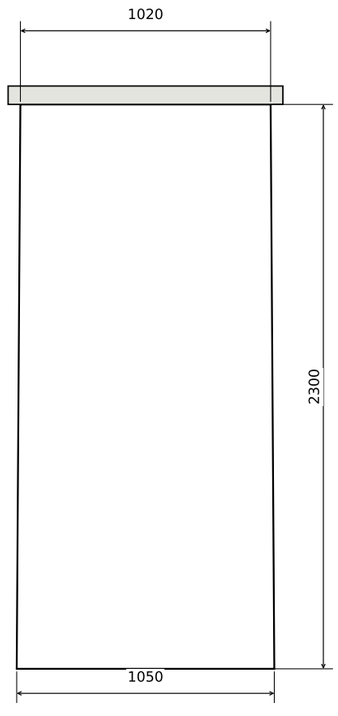

3 Y-FACE ELEVATION 1:25

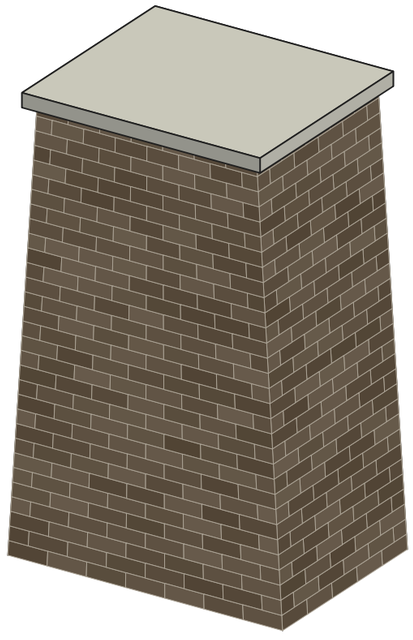

4 3D VIEW NTS

ALL DIMENSIONS IN mm. HEIGHT 2300 TO TOP OF BRICKWORK; CAP EXCLUDED.

ALL DIMENSIONS IN mm UNLESS STATED OTHERWISE

NOTES:

1. Brickwork: base 1500 x 1050; top 1200 x 1020; height 2300. Top centred over base.

2. CAP UNMEASURED: 75 thick and 50 projection each side are schematic estimates.

3. Internal voids and wall thickness not surveyed. Model shows external envelope only.

4. Brick pattern is indicative. Telecom steelwork, antenna, pipe and adjacent roof excluded.

5. Plan shows cap and brickwork/base projections. X/Y face orientation on GA unconfirmed.

STRUCTURAL MEMBER KEY

Brickwork external envelope

Cap - schematic estimate

Base / concealed brick outlines

X / Y identify faces; not GA axes.

01	FIRST ISSUE	AT	AF	23-10-2026
Rev:	Issue:	Drawn:	Chkd:	Date:

Consultant:

KA ENGINEERING GROUP

Client:

CONNECT

Job Title:

ROOF STRUCTURAL SURVEY

Drawing Title:

CHIMNEY - LAYOUT AND 3D VIEW

Address:

HONEYPOT HALL
HAROLD ROAD
CLACTON-ON-SEA, ESSEX
CO15 6AL

Drawn By:	Checked By:
AT	AF
Scale at A3:	Date (reference sheet):
2D 1:25 / 3D NTS	23-10-2026

Project No:	Drawing No:	Rev:
7111	7111-02	01