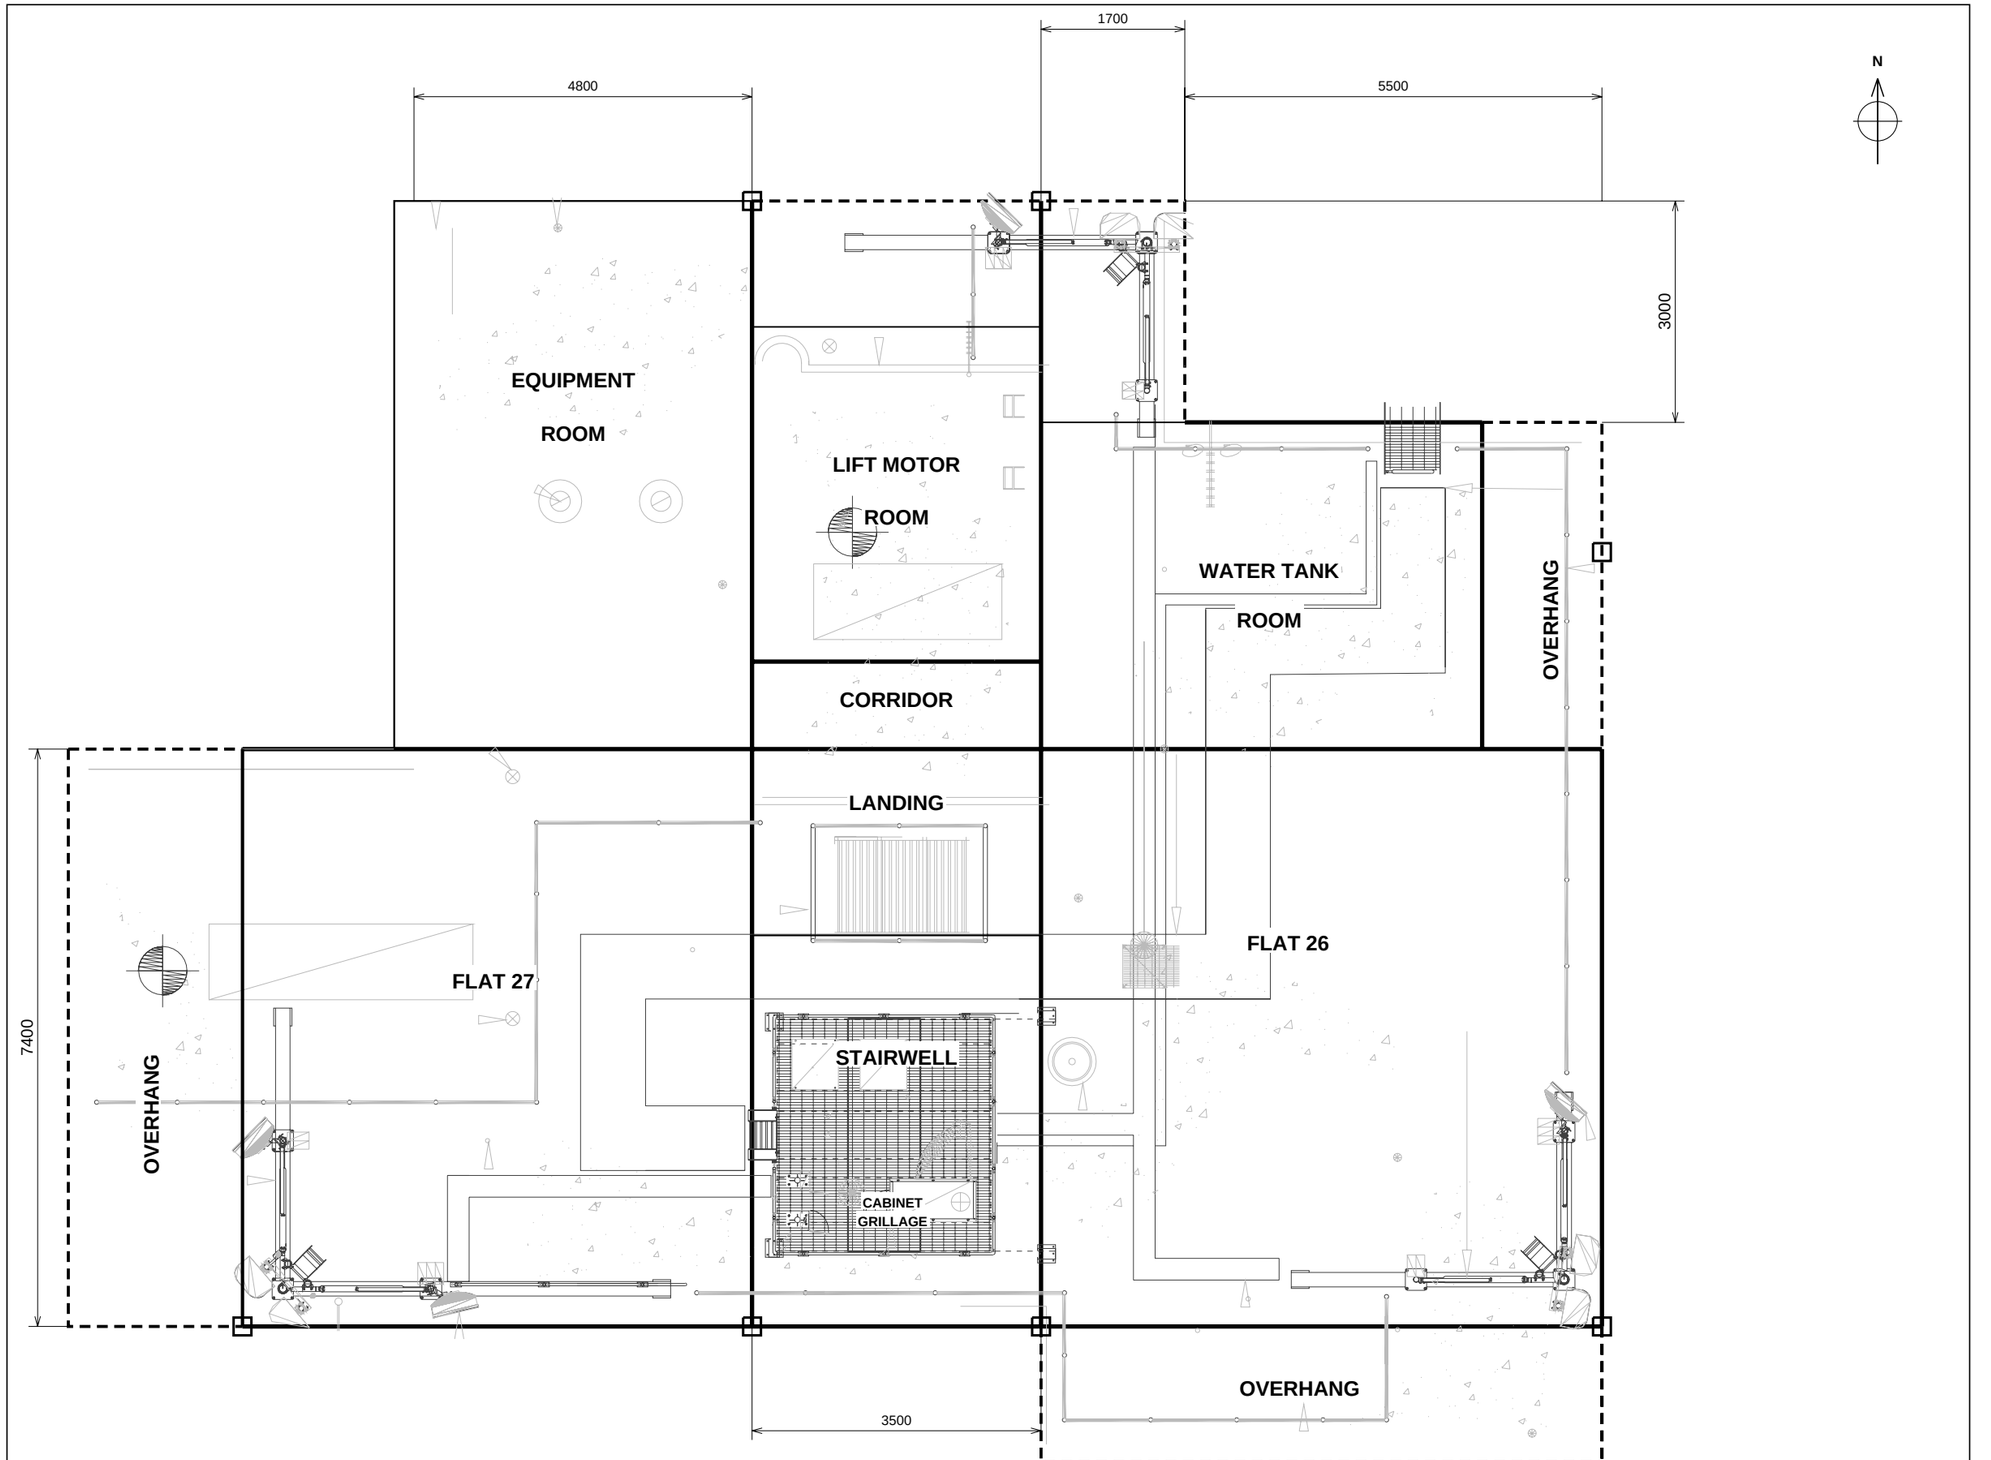


1 **Roof Support Layout**

NTS

DIMENSIONS IN mm; LEVELS ABOVE GROUND

ELEMENT KEY

- Load-bearing walls
- Columns
- Beams

Rev	Issue	Drawn	Chkd	Date
1	REVIEW	ST	AF	02-11-26

Consultant:

KA ENGINEERING GROUP

Client:

Skye Consultants Ltd

Drawing Title:


Roof Support Layout

TADWORTH HOUSE

Webber Street, London SE1 0RH


Drawn: ST Checked: AF

5166-01 | Rev 1 NTS

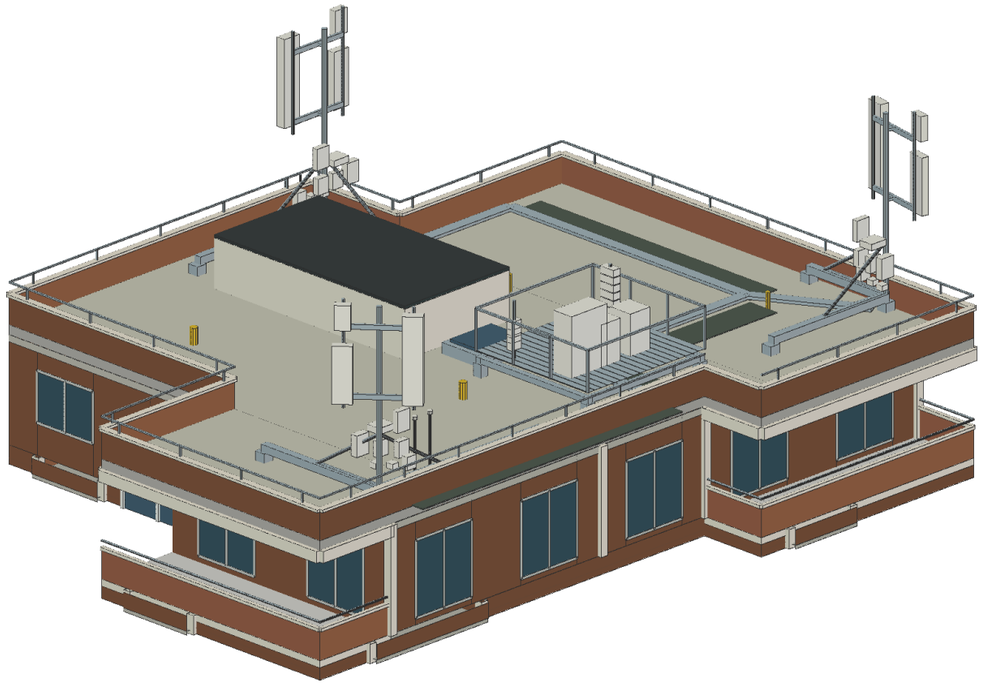

1 **Roof / Top-Floor Arrangement**

3D NTS

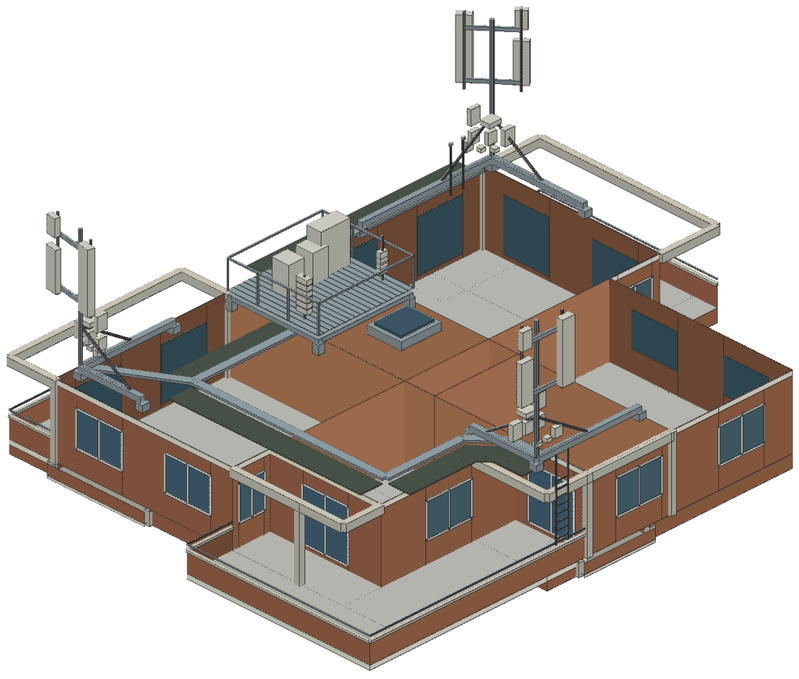

2 **Top-Floor Supports - Roof Omitted**

3D NTS

DIMENSIONS IN mm; LEVELS ABOVE GROUND

DRAWING NOTES

1. Roof and top-floor support arrangement.

2. Main roof +26.10 m; plant-room roof +27.42 m.

3. Second view omits roof for clarity.

ELEMENT KEY

Top-floor load-bearing walls

Overhang beams / columns

Braced mast with yoke brackets

Antenna arrangement: 1 + 2

Rev	Issue	Drawn	Chkd	Date
1	REVIEW	ST	AF	02-11-26

Consultant:

KA ENGINEERING GROUP

Client:

Skye Consultants Ltd

Drawing Title:

Roof / Top-Floor Supports


TADWORTH HOUSE

Webber Street, London SE1 0RH

Drawn: ST Checked: AF

5166-02 | Rev 1 NTS

DIMENSIONS IN mm; LEVELS ABOVE GROUND

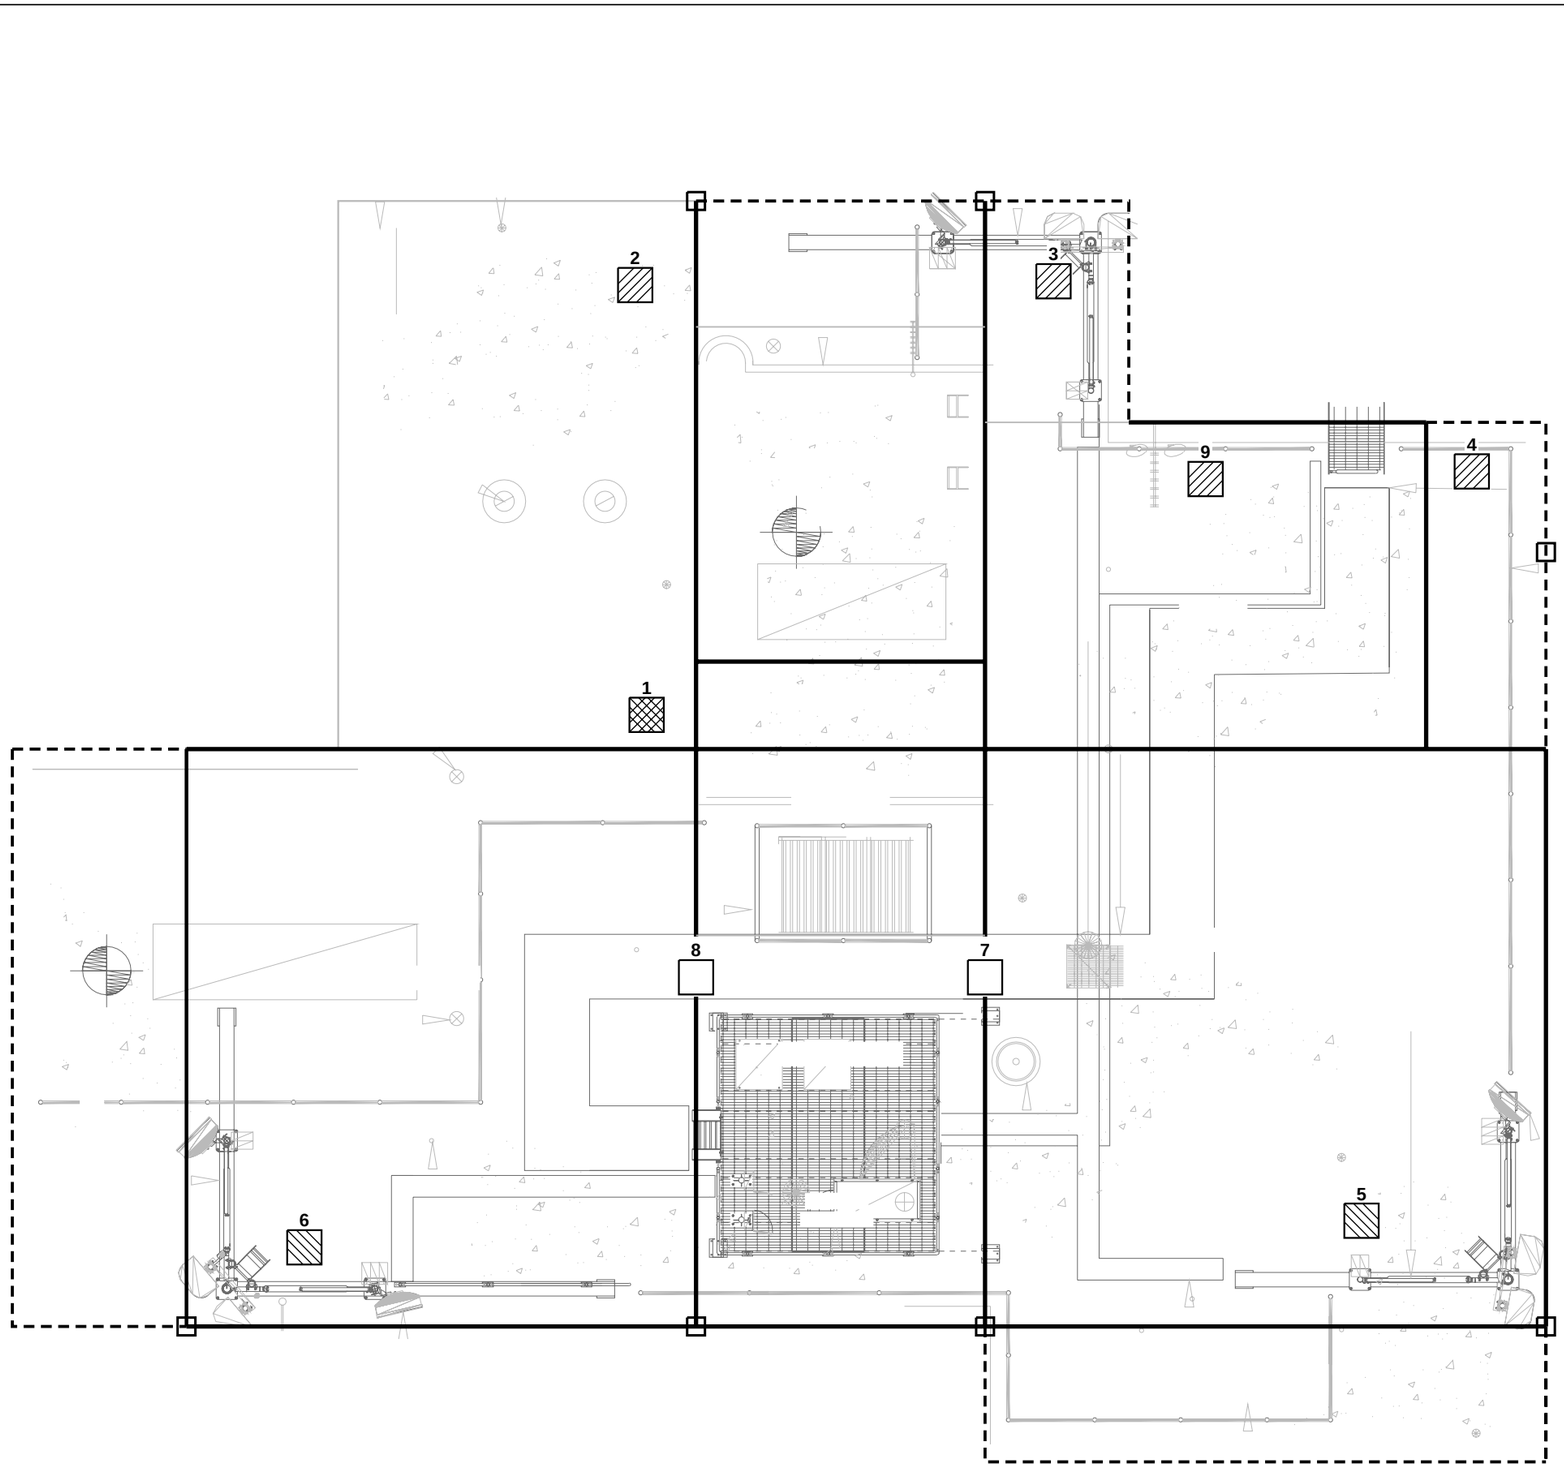

1 **Scan Locations**

NTS

SCAN KEY

- Roof topside
- Soffit
- Topside + soffit
- General

Rev	Issue	Drawn	Chkd	Date
1	REVIEW	ST	AF	02-11-26

Consultant:

KA ENGINEERING GROUP

Client:

Skye Consultants Ltd

Drawing Title:

Scan Locations

TADWORTH HOUSE

Webber Street, London SE1 0RH

Drawn: ST Checked: AF

5166-03 | Rev 1 NTS