
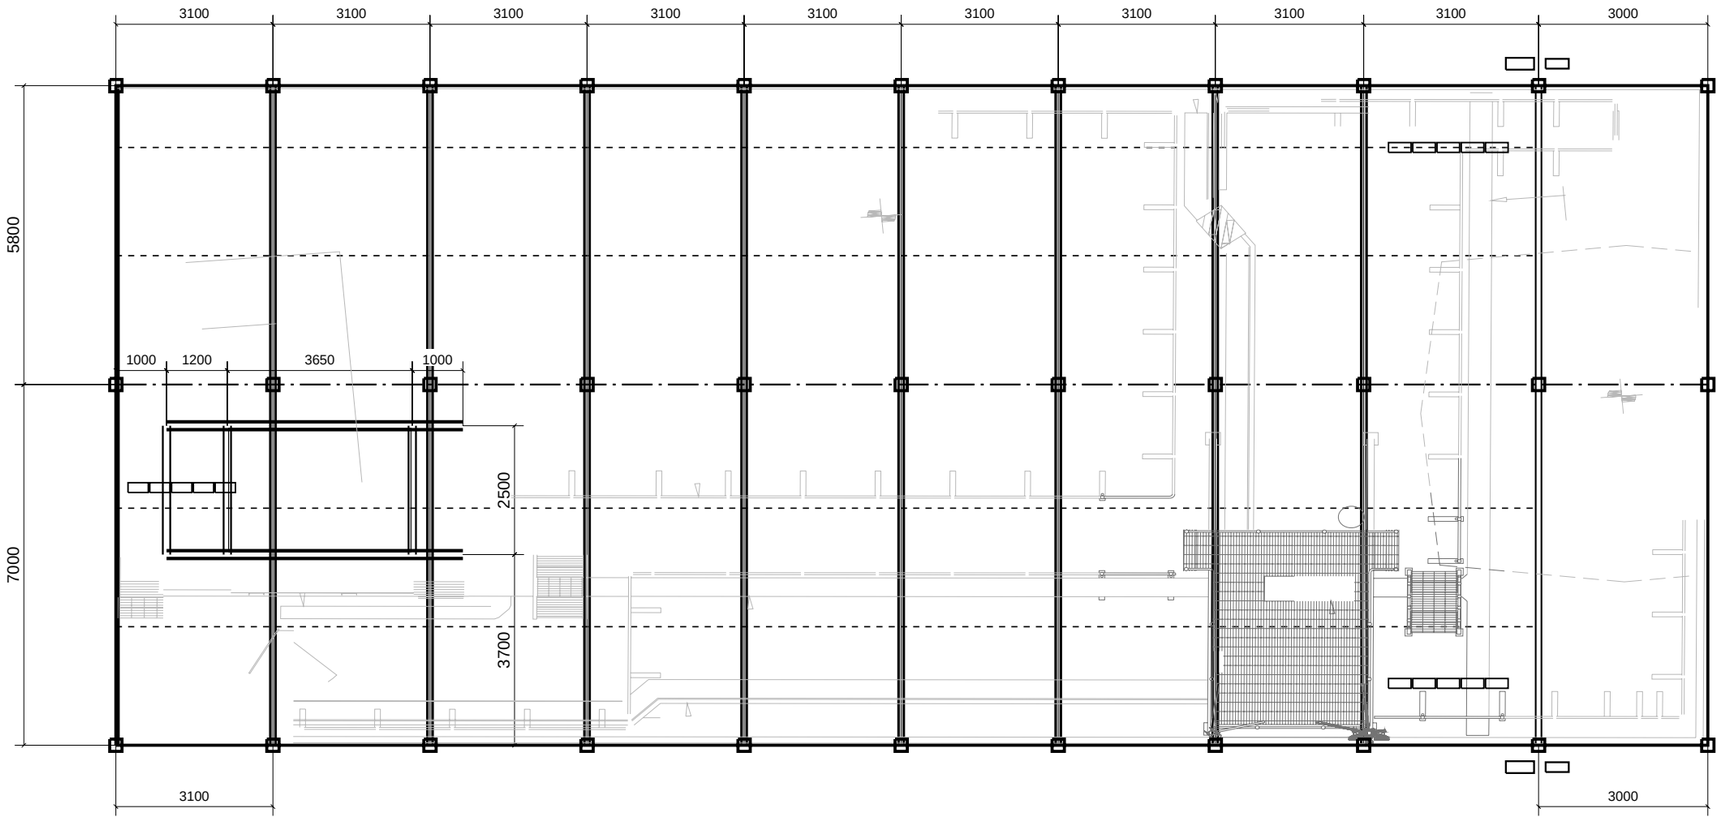


1 Roof Support Layout

NTS

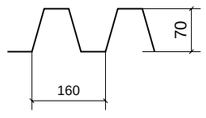

2 Metal Deck Profile

NTS

DIMENSIONS IN mm

DRAWING NOTES

1. Metal deck roof; no scanning conducted.
2. Existing GA grillage retained; new steel overlay aligned to its bearing lines.
3. EMA supports: first column line from east wall.
4. N-S: easternmost beam 203 section; all others 305. Central W-E beam: 152 section.

MEMBER KEY

- 203 mm x 102 mm x 23 kg/m
- 305 mm x 102 mm x 33 kg/m
- 152 mm x 89 mm x 16 kg/m
- EA 65 mm x 65 mm x 8 mm
- 457 mm x 152 mm x 60 kg/m
- 254 mm x 146 mm x 31 kg/m
- Concrete encased columns: 152 mm x 152 mm x 30 kg/m

Rev	Issue	Drawn	Chkd	Date
1	REVIEW	AT	AF	11-11-26

Consultant:

KA ENGINEERING GROUP

Client: JetNSL

JET network solutions

Drawing title:

Roof Support Layout


OASIS HOTEL

The Promenade, Great Yarmouth

Norfolk, NR30 2RB


Drawn: AT Checked: AF

7149-01 | Rev 1 NTS

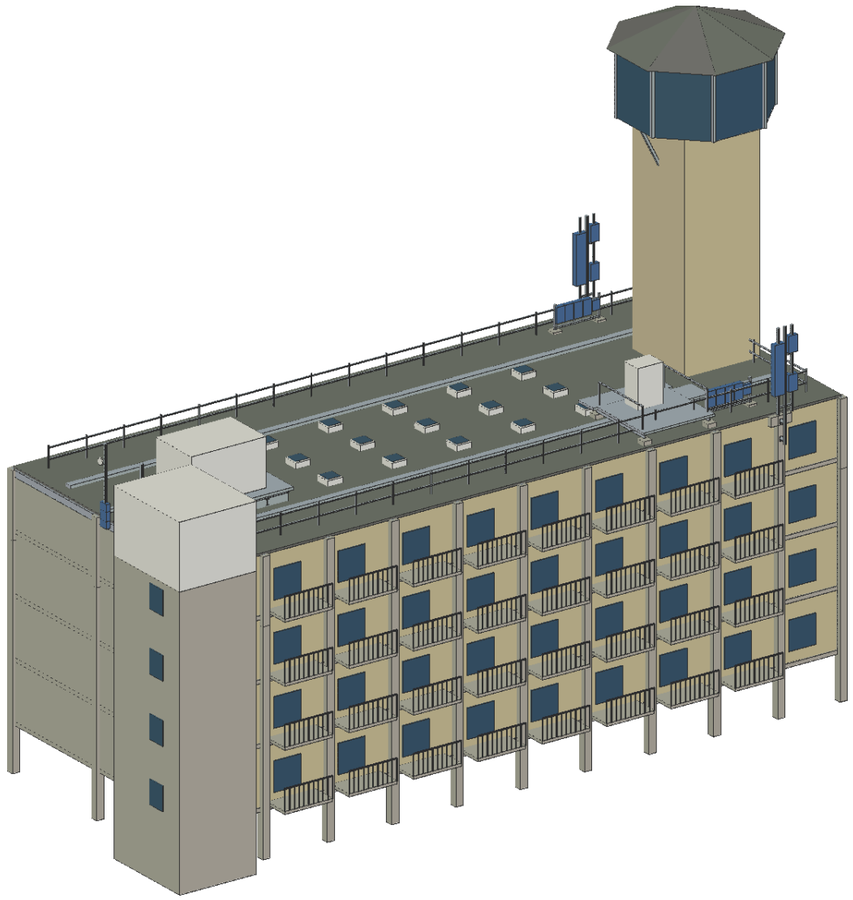

1 **Building - Retained / Proposed Equipment**

3D NTS

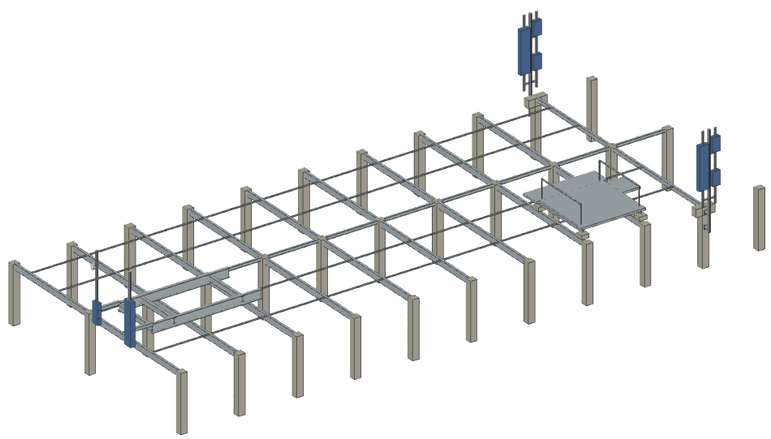

2 **Roof Steel / Antenna Support Locations**

3D NTS

DIMENSIONS IN mm

DRAWING NOTES

1. Existing retained equipment and proposed upgrades shown.

2. Main roof +24000; plant room +27000; tower +39000 AGL.

3. Building envelope and unmeasured details are visual representations.

4. Lower view omits roof covering to show supports.

VIEW KEY

Cream: tower / facade

Grey: roof / concrete

Blue-grey: glazing

Blue: proposed telecoms equipment

Rev	Issue	Drawn	Chkd	Date
1	REVIEW	AT	AF	11-11-26

Consultant:

KA ENGINEERING GROUP

Client: JetNSL

JET network solutions

Drawing title:

Building / Roof Supports

OASIS HOTEL


The Promenade, Great Yarmouth

Norfolk, NR30 2RB

Drawn: AT Checked: AF

7149-02 | Rev 1 NTS

EMA support connection - Sectors 1 and 2

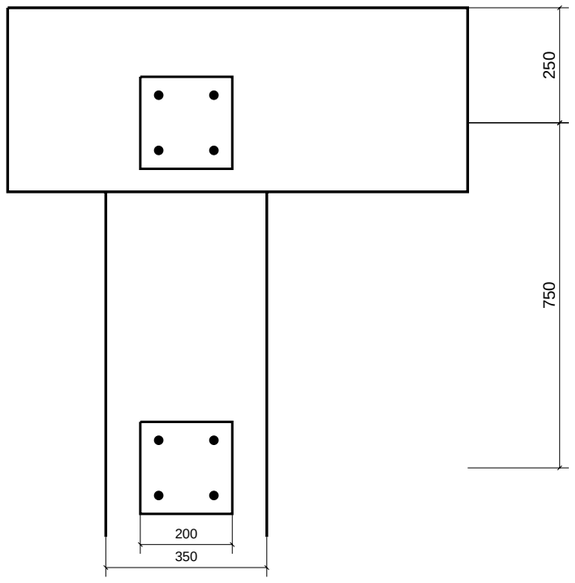

Two 200 x 200 plates

4 No. M16 bolts per plate

Fixings to concrete-encased

perimeter columns at S1 and S2.

Plate thickness and bolt centres

not specified in survey sketch.

(1) **EMA Connection - S1 / S2**

NTS

DIMENSIONS IN mm

DRAWING NOTES

1. Typical EMA support connection for Sectors 1 and 2.

2. Fixings to concrete-encased perimeter columns.

3. Plate dimensions and M16 bolt size from survey sketch.

4. 250 reference is to the upper plate centre; overall beam depth not specified.

CONNECTION KEY

Plates: 200 x 200

Bolts: M16, four per plate

Column face width: 350

Vertical reference spacing: 750

Rev	Issue	Drawn	Chkd	Date
1	REVIEW	AT	AF	11-11-26

Consultant:

KA ENGINEERING GROUP

Client: JetNSL

JET network solutions

Drawing title:

EMA Supports - Sectors 1 and 2

OASIS HOTEL

The Promenade, Great Yarmouth

Norfolk, NR30 2RB

Drawn: AT Checked: AF

7149-03 | Rev 1 NTS