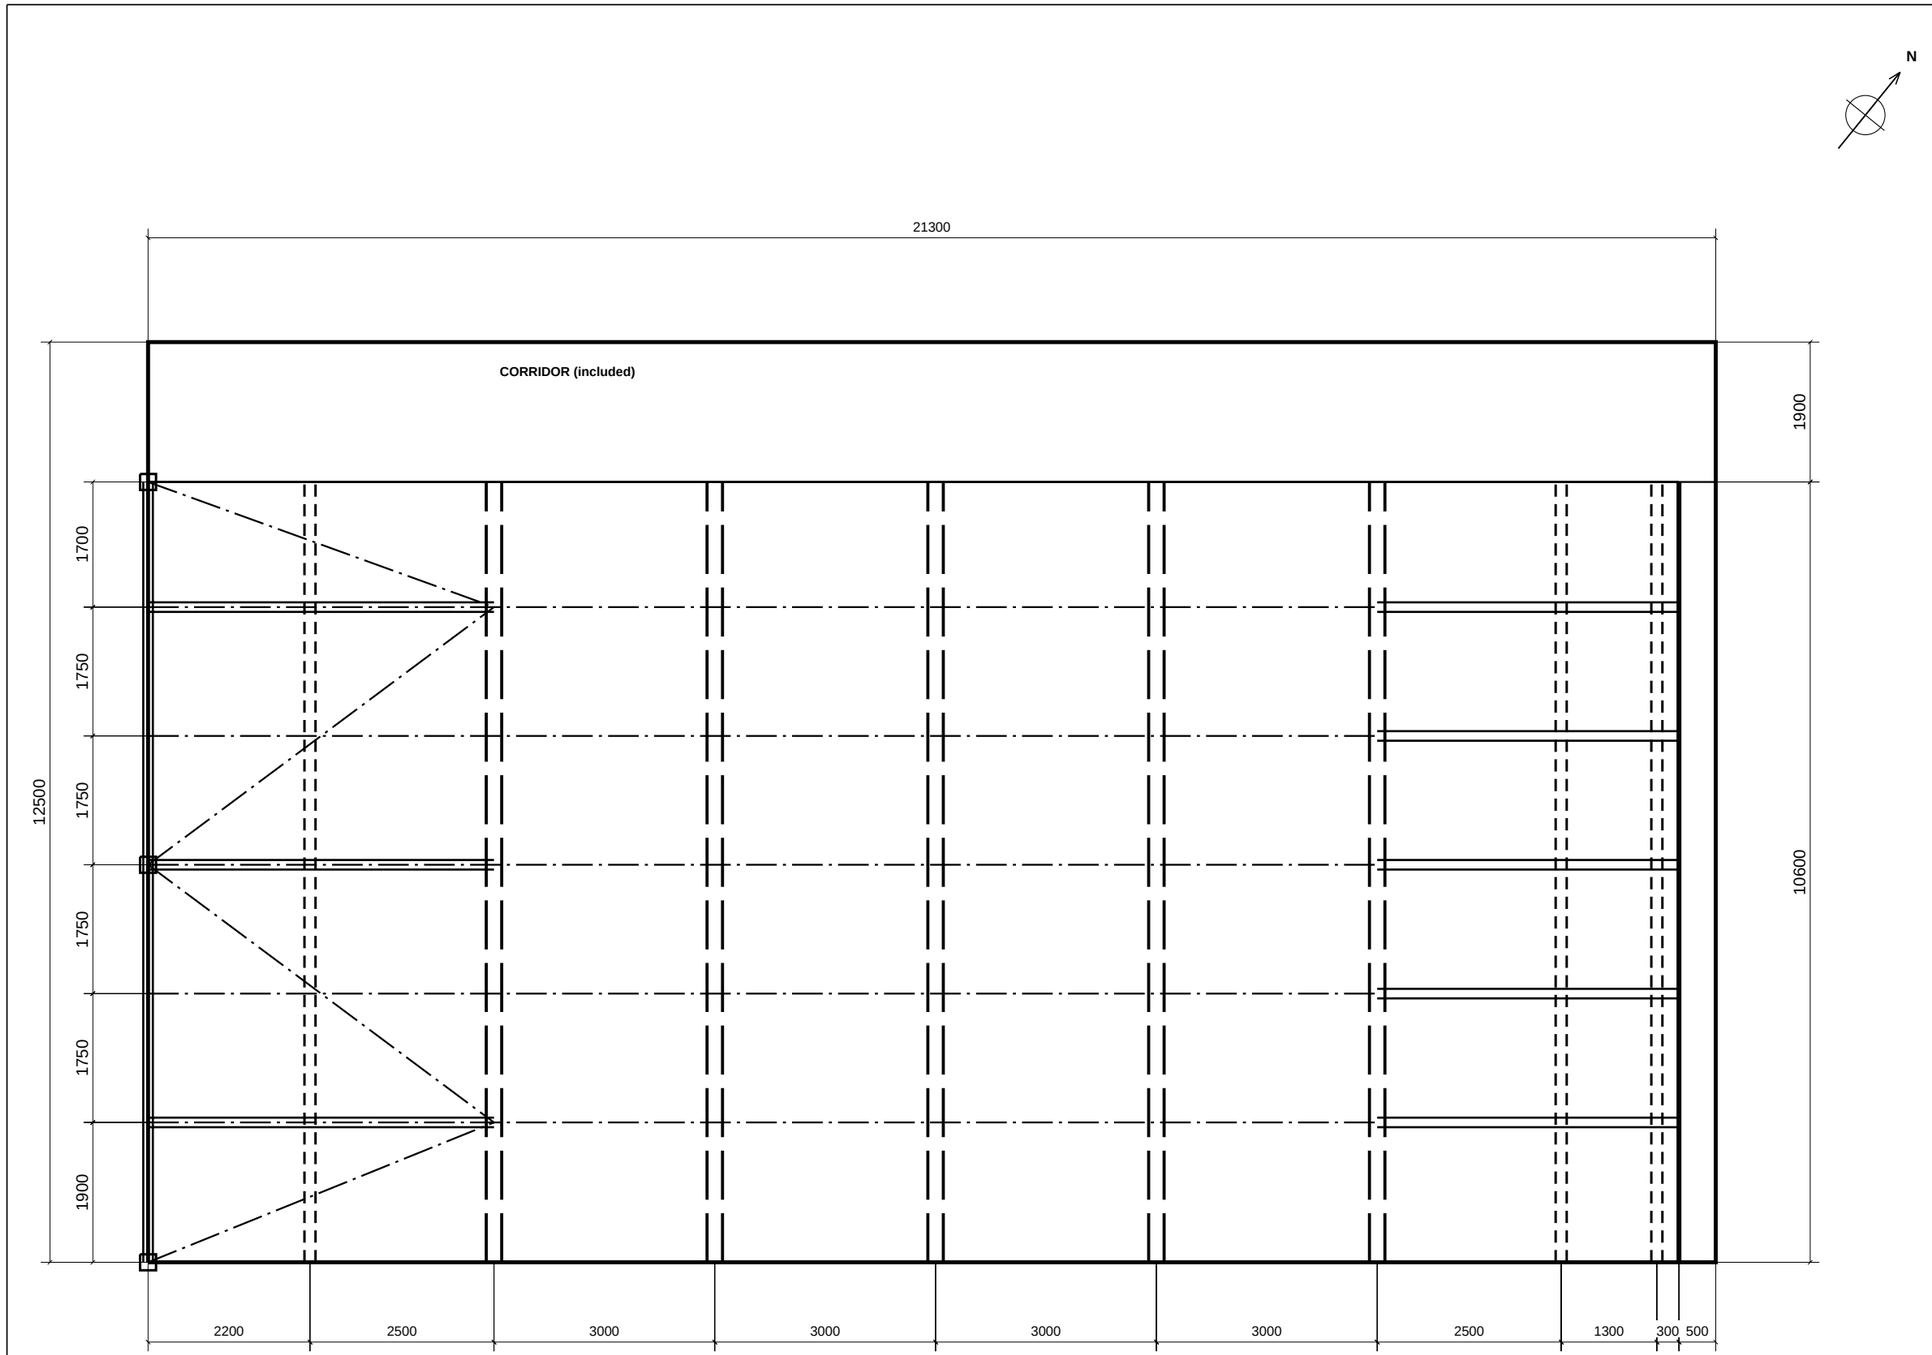


1 **Roof Support Layout**

NTS

DIMENSIONS IN mm

DRAWING NOTES

1. Metal deck roof; existing PV arrays in three rows.
2. Nominal overall depth includes the corridor strip.
3. Castellated beams 800 deep; flange 210 wide x 18 thick.
4. Equipment set-out is shown on sheet 71222-02.
5. CHS: upper in left diagonal bay; lower in central bays. Right bay: I-beams only.

MEMBER KEY

- CB 800 deep; flange 210 x 18
- B1 I-beam 200 x 250
- B2 I-beam 200 x 150
- CHS 90 dia; levels per note 5
- FW Full-web end beam

Rev	Issue	Drawn	Chkd	Date
1	REVIEW	S.T.	K.S.	08-11-26

Consultant:

KA ENGINEERING GROUP

Client:

Jansen SL

Drawing Title:

Roof Support Layout


JET 0231

Gala Theatre & Cinema

Millennium Square, Durham

Drawn: S.T. Checked: K.S.

71222-01 | Rev 1 NTS

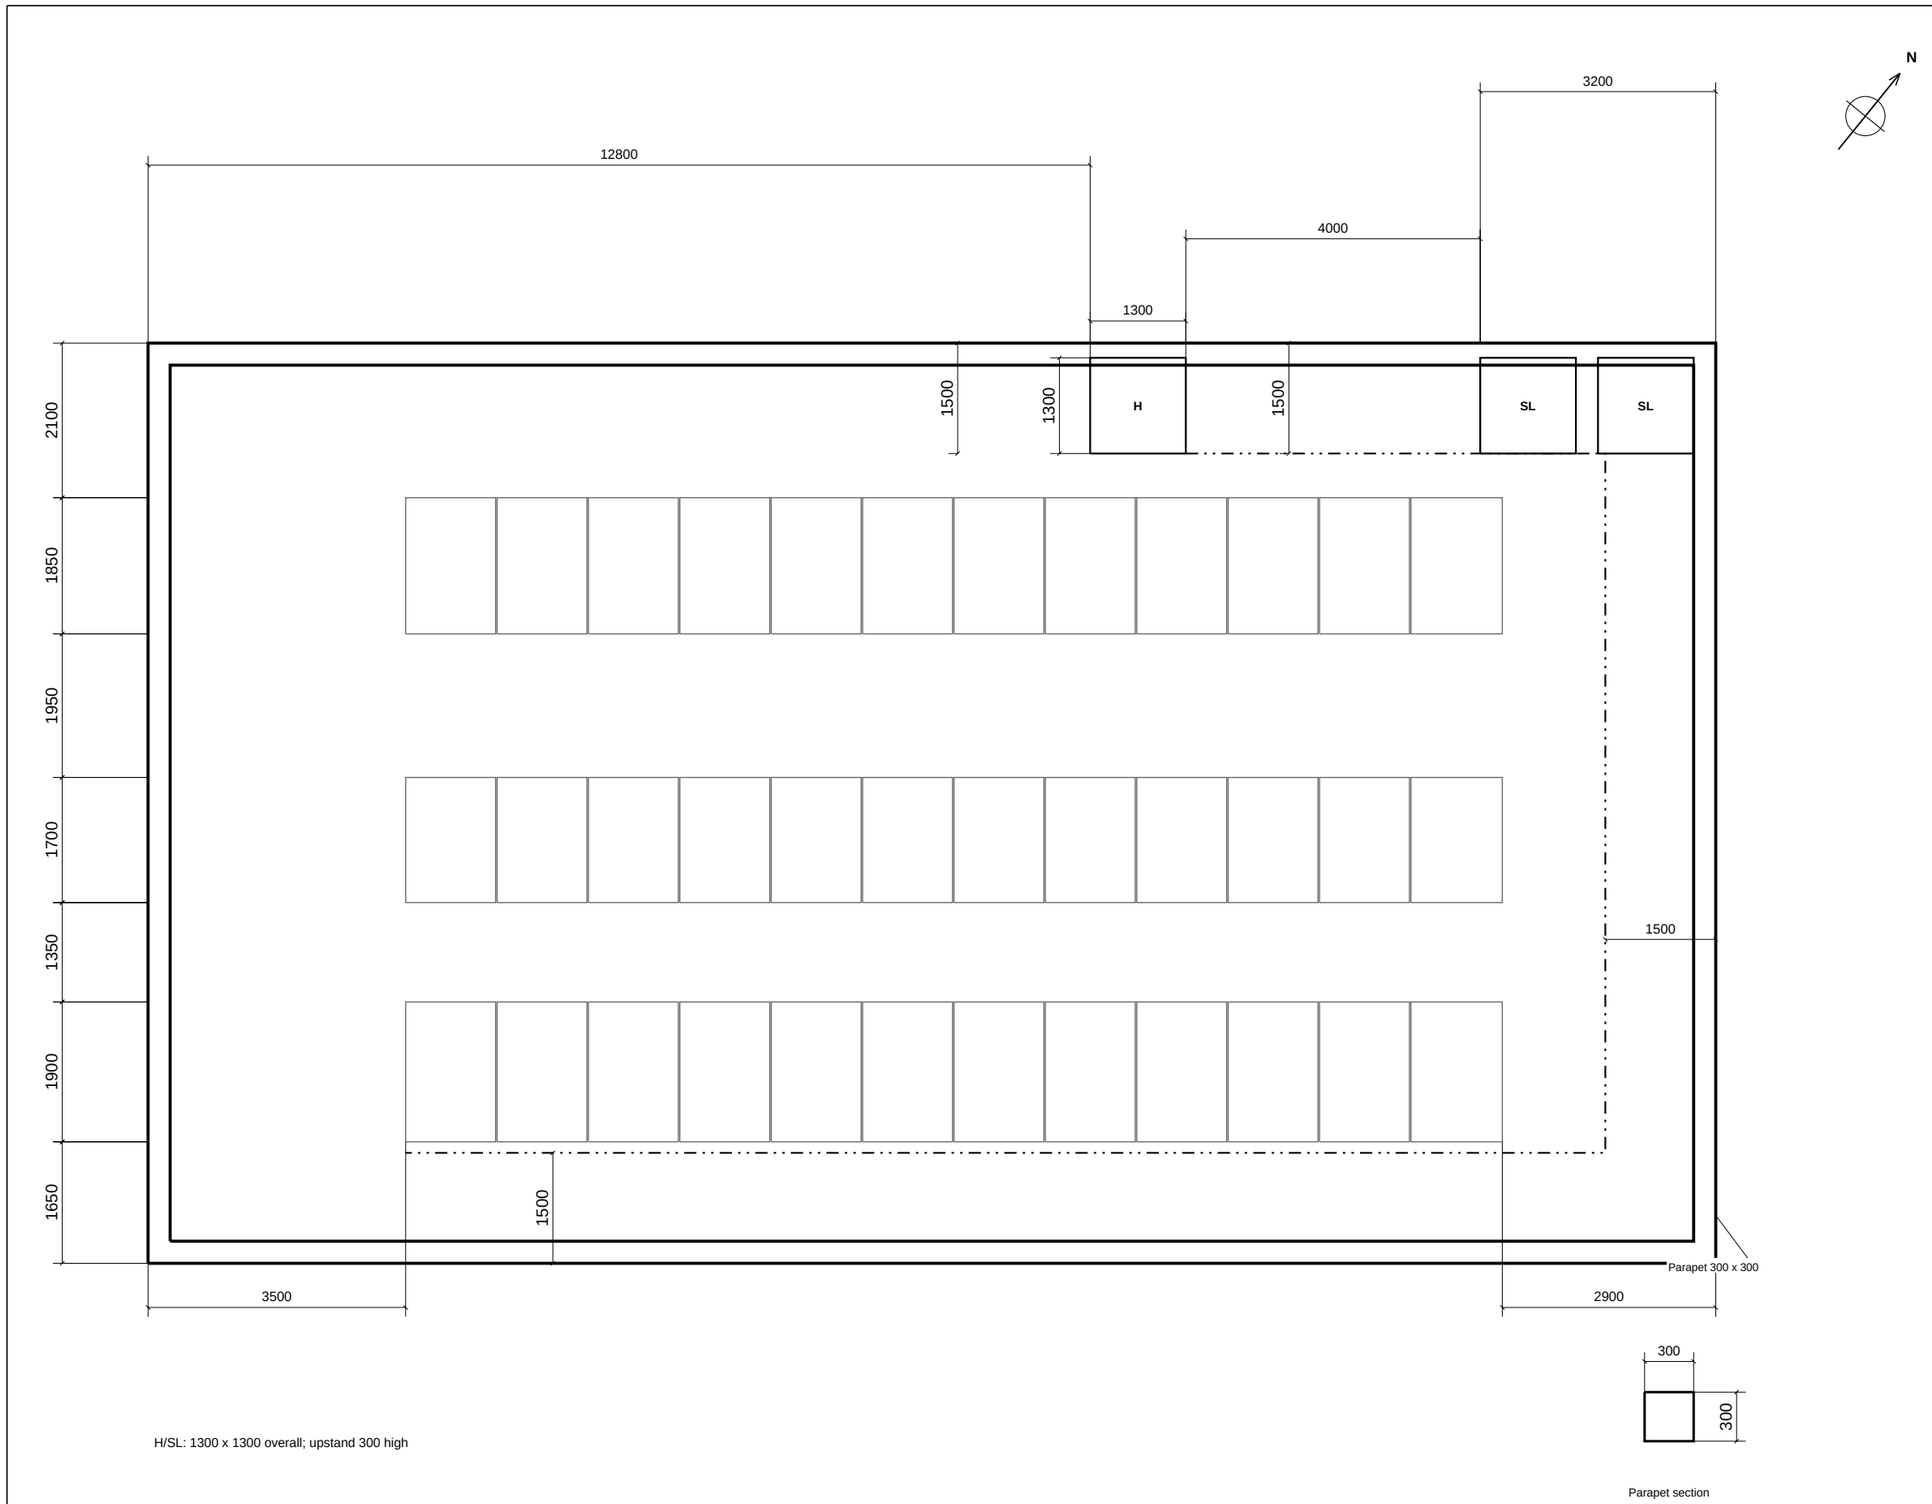

H/SL: 1300 x 1300 overall; upstand 300 high

Parapet section

1 **Roof Equipment Set-out**

NTS

DIMENSIONS IN mm

DRAWING NOTES

1. Existing PV arrays in three rows.
2. Hatch/skylight upstands: 1300 x 1300 x 300 high.
3. Safety line set back 1500 from building edge; parapet 300 x 300.
4. Setbacks are to outside building edges; opening gaps are face to face.

ROOF KEY

- PV arrays
- Safety line
- Parapet
- H hatch / SL skylight

Rev	Issue	Drawn	Chkd	Date
1	REVIEW	S.T.	K.S.	08-11-26

Consultant:

KA ENGINEERING GROUP

Client:

Jansen SL

Drawing Title:

Roof Equipment Layout


JET 0231

Gala Theatre & Cinema

Millennium Square, Durham


Drawn: S.T. Checked: K.S.

71222-02 | Rev 1 NTS

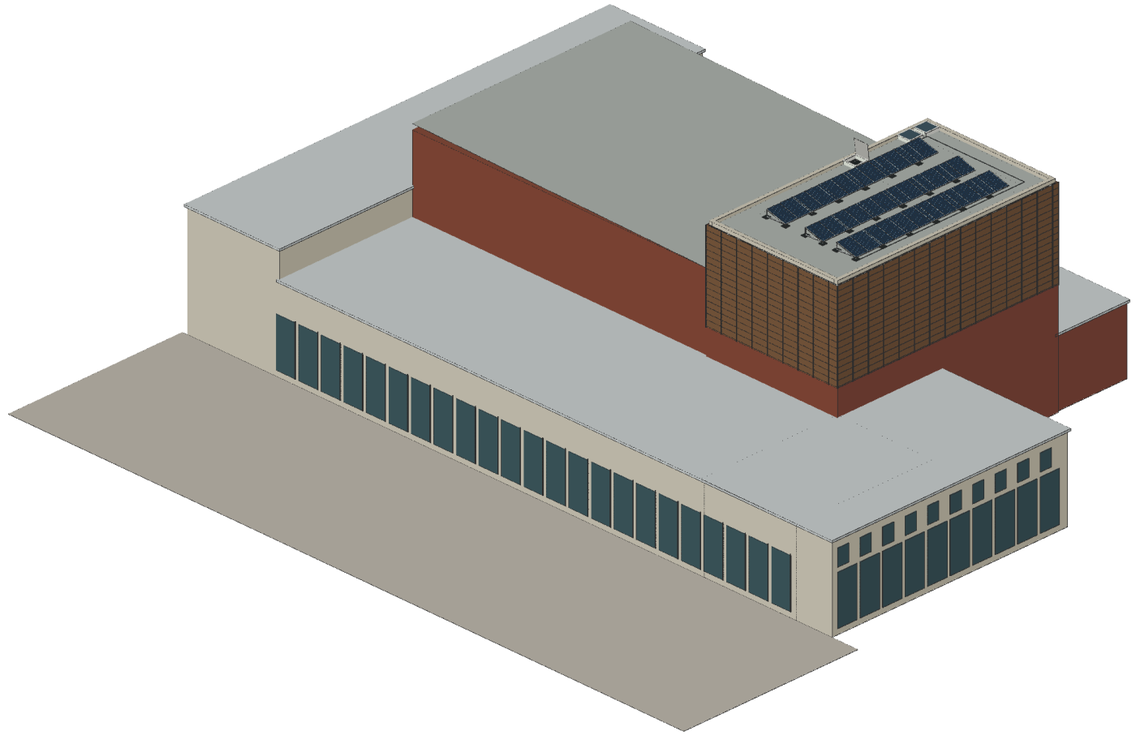


1 **Theatre Context - Target Fly Tower**

3D NTS

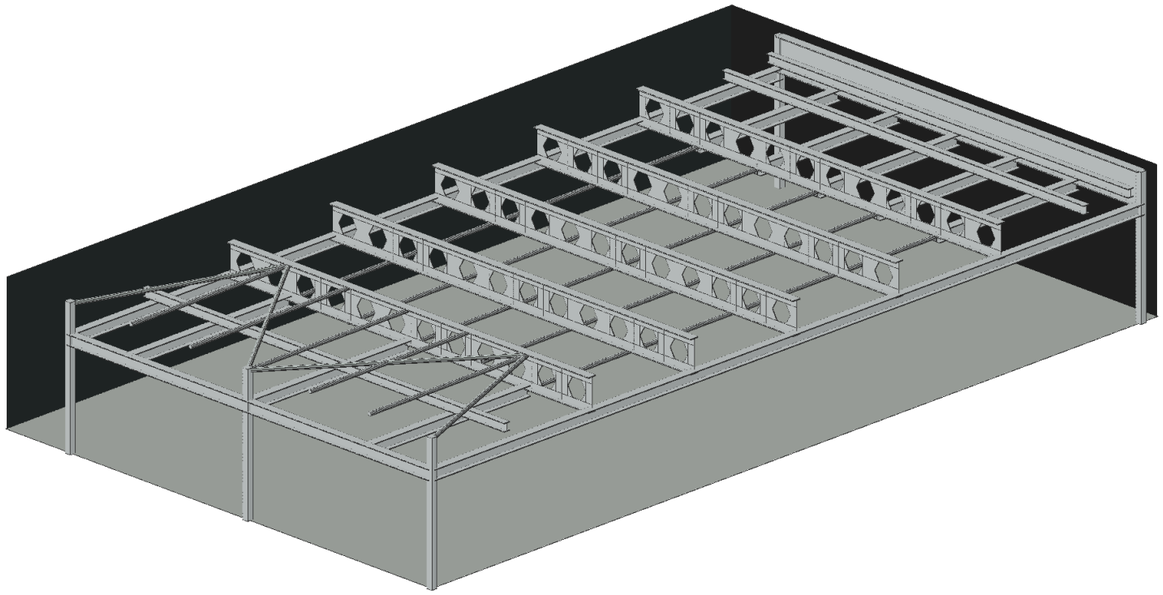

2 **Roof Supports - CHS Levels by Bay**

3D NTS

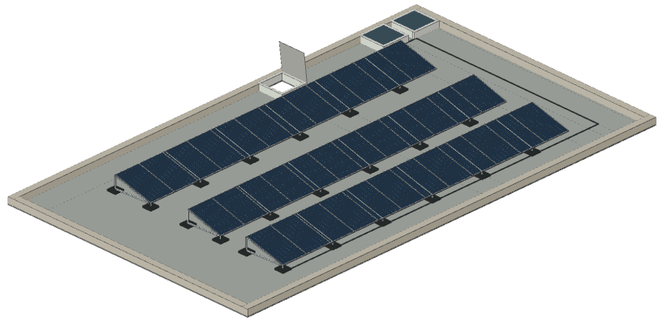

3 **Existing Roof**

3D NTS

DIMENSIONS IN mm

DRAWING NOTES

1. Raised timber-clad fly tower is the roof in scope.
2. Surrounding theatre is visual context; building heights unmeasured.
3. Lower view omits roof decking and PV arrays to expose supports.
4. Fly-system bars, pulleys and cables are excluded from roof-support members.

VIEW KEY

Brown: timber-clad fly tower

Blue-grey: existing PV arrays

White/grey: roof steel

Roof openings: hatch / skylights

CHS upper left / lower centre

Rev	Issue	Drawn	Chkd	Date
1	REVIEW	S.T.	K.S.	08-11-26

Consultant:

KA ENGINEERING GROUP

Client:

Jansen SL

Drawing Title:

3D Building / Roof Supports

JET 0231

Gala Theatre & Cinema

Millennium Square, Durham

Drawn: S.T. Checked: K.S.

71222-03 | Rev 1 NTS