
ROOF LAYOUT - REFERENCE OVERLAYS

FIRST REVIEW | WRITTEN SURVEY DIMENSIONS GOVERN | NTS | NOT FOR CONSTRUCTION

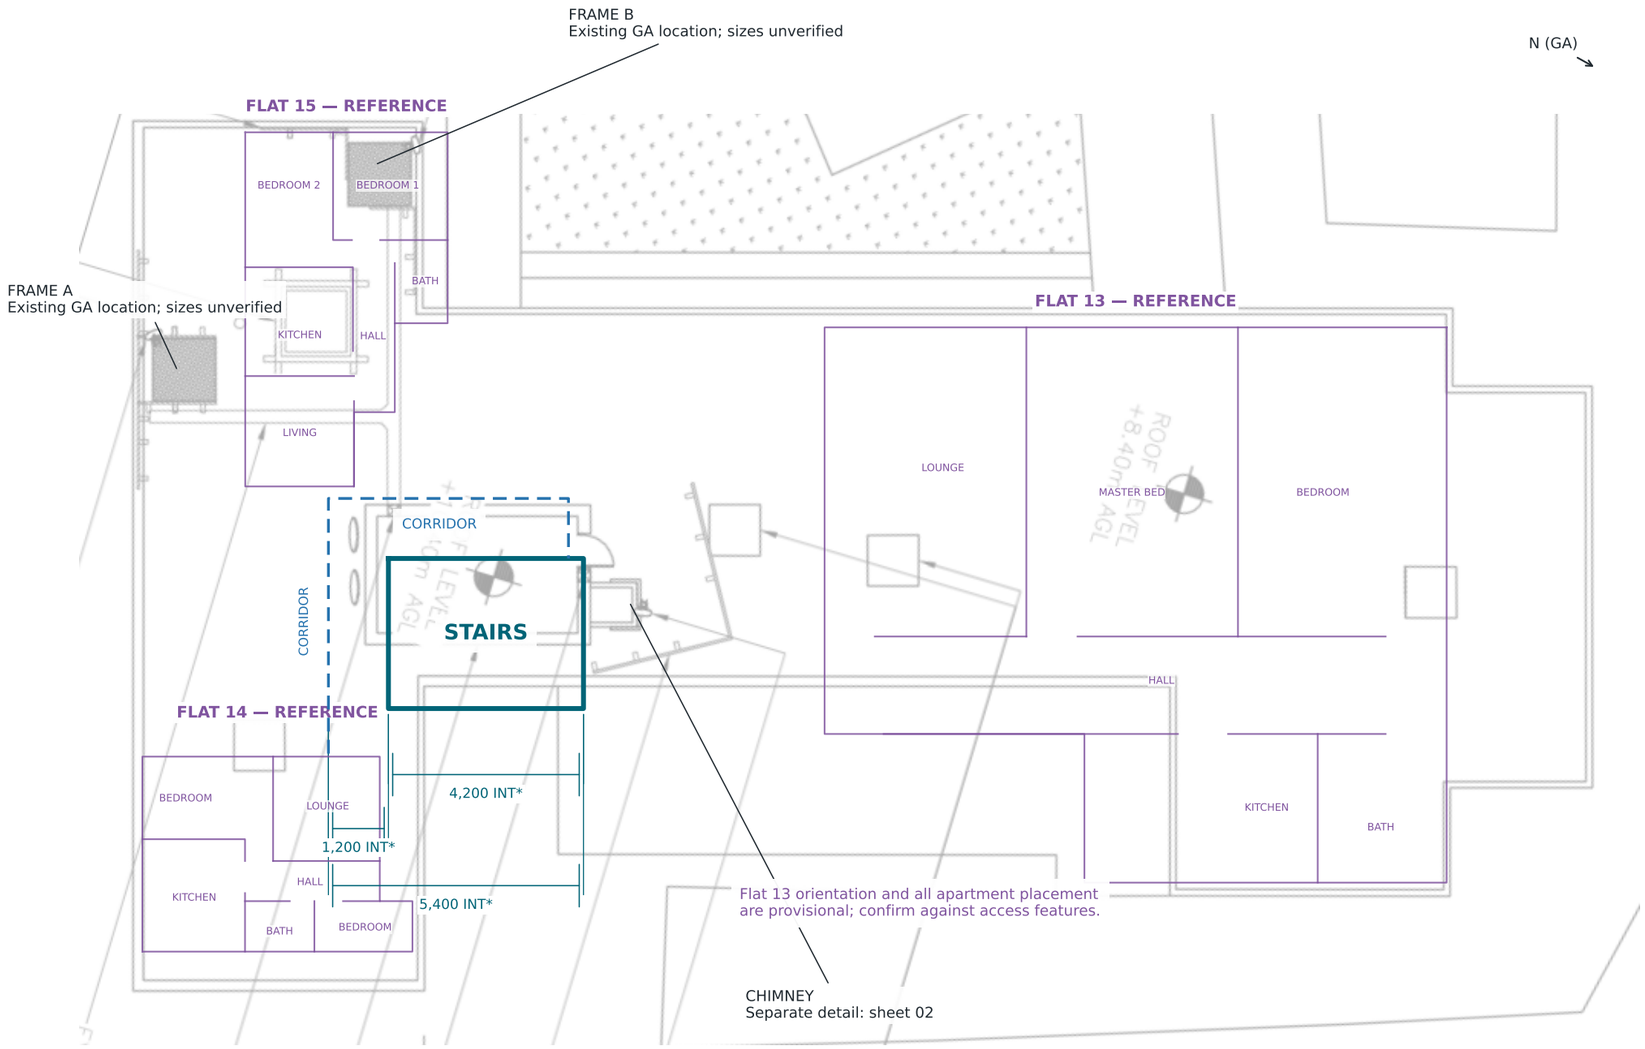

SURVEY READINGS FOR RECONCILIATION (source labels in metres; not all endpoints adopted):
Under-dot / EXT labels: 7.5; 4.6?; 4.2; 3.3; 4.2; 8.3. Other labels include 9.4?, 4.2, 5.4, 1.2 and an unclear stair depth.
Plant-room wall thickness noted as 0.28 m (280 mm); do not apply this to other walls. No PDF-scale dimensions inferred.

*Internal dimension readings / exact endpoints require review. Purple room lines are approximate traces of website plans, not surveyed partitions.

EXT = EXTERNAL WALL FACES (UNDER-DOT IN SOURCE). UNRESOLVED ENDPOINTS REMAIN FOR REVIEW.

Sources: Survey Notes pp2-3; GA 200 Rev 1A (PDF p5); supplied apartment snippets; engineering lead clarifications.

ALL DIMENSIONS IN mm UNLESS STATED OTHERWISE

NOTES:

1. Top-floor flats 13-15 were inaccessible. Apartment plans are third-party references, not surveyed structure.

2. Purple plans are approximate transcriptions of inline images. Graphic fitting and flat 13 orientation need review.

3. Flat 14 rotated 90 deg CCW; flat 15 unchanged, per engineer. Dashed corridors are non-load-bearing.

4. Under-dot dimensions are external face to face. Other readings/endpoints marked * need review.

5. Frame and pole sizes/anchors unverified. Chimney elevation is on sheet 02. No PDF-scale dimensions used.

STRUCTURAL MEMBER KEY

- Load-bearing stair walls / Engineer-described survey line
- Non-load-bearing corridors
- Apartment reference partitions / Structural status unverified
- Client GA / existing equipment

Apartments: reference only, not surveyed.

Rev:	Issue:	Drawn:	Chkd:	Date:
P01	FIRST REVIEW	TBC	TBC	21-10-2026

Consultant:

KA ENGINEERING GROUP

Client:

Connect44

Job Title:

ROOF STRUCTURAL SURVEY

Drawing Title:

ROOF LAYOUT - REFERENCE OVERLAYS

Address:

HONEYPOT HALL
HAROLD ROAD
CLACTON-ON-SEA, ESSEX
CO15 6AL


Drawn By:	Checked By:
TO CONFIRM	TO CONFIRM
Scale at A3:	**Date (reference sheet):**
NTS / DO NOT SCALE	21-10-2026

Project No:	Drawing No:	Rev:
7111	7111-01	P01


CHIMNEY - X / Y FACE ELEVATIONS

FIRST REVIEW | WRITTEN SURVEY DIMENSIONS GOVERN | NTS | NOT FOR CONSTRUCTION

X FACE ELEVATION

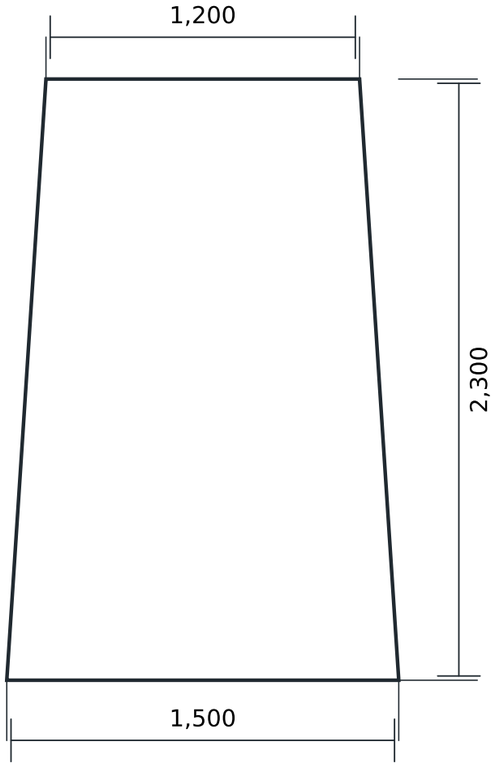

Y FACE ELEVATION

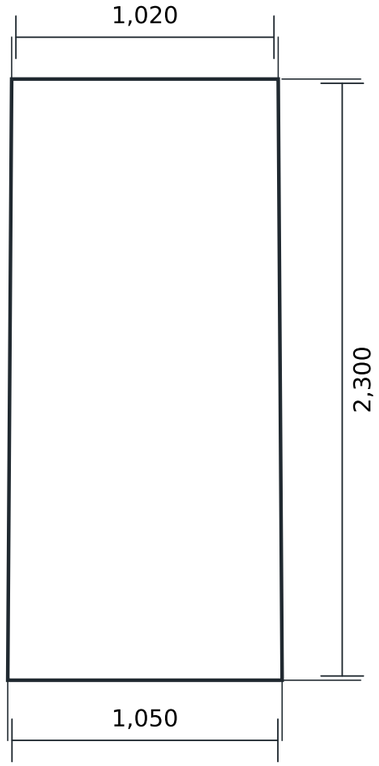

Confirmed dimensions: top 1,200 × 1,020; base 1,500 × 1,050; height 2,300 mm.
Faces shown centred for illustration. Taper distribution and X/Y orientation on GA are not established.
No steelwork, fixings, internal void, wall thickness or masonry strength inferred.

ALL DIMENSIONS IN mm. X / Y ARE THE TWO CHIMNEY FACES, NOT ASSUMED GA AXES.

Sources: Survey Notes pp2-3; GA 200 Rev 1A (PDF p5); supplied apartment snippets; engineering lead clarifications.

ALL DIMENSIONS IN mm UNLESS STATED OTHERWISE

NOTES:

1. Top: 1,200 x 1,020 mm. Base: 1,500 x 1,050 mm. Height: 2,300 mm. Engineer confirmed.

2. X and Y identify the rectangular faces. Their orientation on the GA remains unconfirmed.

3. Centred outlines are illustrative; taper eccentricity and face plumbness were not established.

4. Masonry thickness, internal voids, material strength and chimney-mounted steelwork are not established.

5. Dimensions show survey information, not capacity or anchor design. Roof layout is on sheet 01.

STRUCTURAL MEMBER KEY

— Chimney external outline
Survey dimensions confirmed

— Dimension / extension line

X / Y orientation on GA unconfirmed.

P01	FIRST REVIEW	TBC	TBC	21-10-2026
Rev:	Issue:	Drawn:	Chkd:	Date:

Consultant:

KA ENGINEERING GROUP

Client:

Connect44

Job Title:
ROOF STRUCTURAL SURVEY

Drawing Title:
CHIMNEY - X / Y FACE ELEVATIONS

Address:
HONEYPOT HALL
HAROLD ROAD
CLACTON-ON-SEA, ESSEX
CO15 6AL

Drawn By:	Checked By:
TO CONFIRM	TO CONFIRM
Scale at A3:	**Date (reference sheet):**
NTS / DO NOT SCALE	21-10-2026

Project No:	Drawing No:	Rev:
7111	7111-02	P01