cornerstone

CORNERSTONE – BEACON 4

Pack Issue:	Option:
A	–

CELL NAME: SOUTH WATER TOWER

circet UK

Unit 27F-G, Hartlebury Trading Estate, Crown Lane, Hartlebury, Worcestershire, DY10 4JD

✓ INDICATES MNO(S)/SHARER WITH LIVE DEMAND IN PROGRESS

CSID	–	VF	–	TEF
11482824		–		036507
PROJECT No.	–	TM Cell ID	–	N/A
–		–		–

PASSIVE SCOPE OF WORKS:

EXISTING ELTEK 4TH GEN PSU TO BE REMOVED AND REPLACED WITH ALLOCATED EFF1 CABINET AT GROUND LEVEL


ACTIVE SCOPE OF WORKS:

6No. EXISTING ANTENNAS TO BE REMOVED AND REPLACED WITH 9No. ALLOCATED ANTENNAS AND 15No. RRHS TO BE INSTALLED ON EXISTING FREESTANDERS

DRAWING TITLE	DRAWING No.	DATE OF ISSUE: 14.11.25	REV	REV	REV	REV	REV	REV	REV
Site Location Maps	100	1A							
Lease Agreement Plan	101	1A							
Code Agreement Elevation	102	1A							
Existing Site Plan	200	1A							
Proposed Site Plan	201	1A							
Existing Site Elevation	300	1A							
Proposed Site Elevation	301	1A							
Existing Antenna Plan	400	1A							
Allocated Antenna/RRU Plan	401	1A							
Allocated Equipment Plan	402	1A							
Occupational ICNIRP Zone Plan	450	1A							
Occupational ICNIRP Zone Elevation	451	1A							
Public ICNIRP Zone Plan	452	1A							
Public ICNIRP Zone Elevation	453	1A							
Existing TEF R.F. System	500	1A							
Allocated TEF R.F. System Schematic	550	1A							
Allocated TEF Antenna Schedule	551	1A							
Proposed Equipment Schedule	570	1A							

ROLE	EMAIL	ISSUED						
TEF Delivery Manager	peter.oshaughnessy@virginmediao2.co.uk	✓						
TEF TX Planner	reece.balmer2@virginmediao2.co.uk	✓						
TEF Radio Planner	stefan.prokopov@virginmediao2.co.uk	✓						

SITE LOCATION

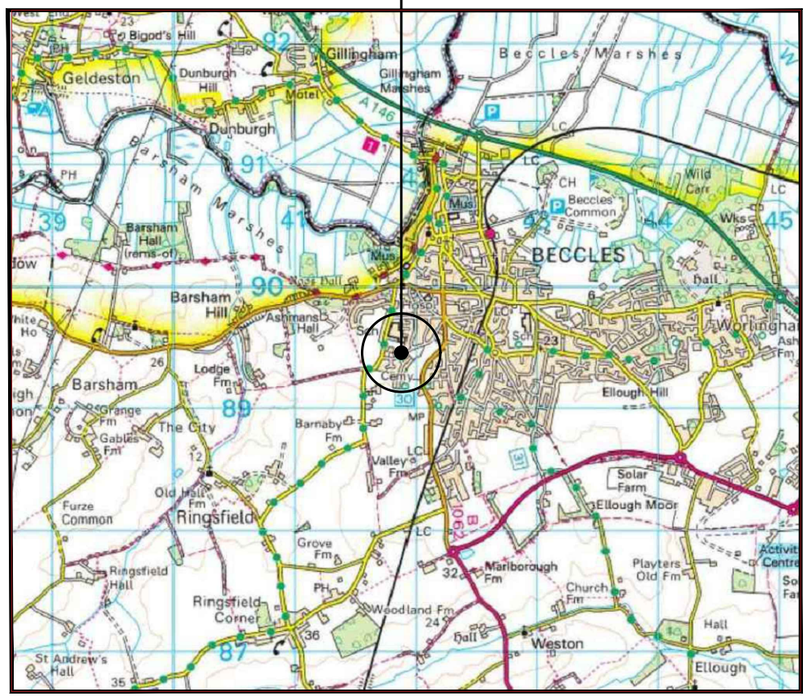

SITE LOCATION
(Scale 1:50000)

Ordnance Survey map extract based upon Landranger map series with the permission of the controller of His Majesty's Stationery Office Licence No. 100022432 Crown copyright.

0 500 1000 1500 2000 2500m
1:50000




SITE PHOTOGRAPH



= Right of Access

= Public Access Route

SITE LOCATION
W3W:
noun.narrating.shortcuts

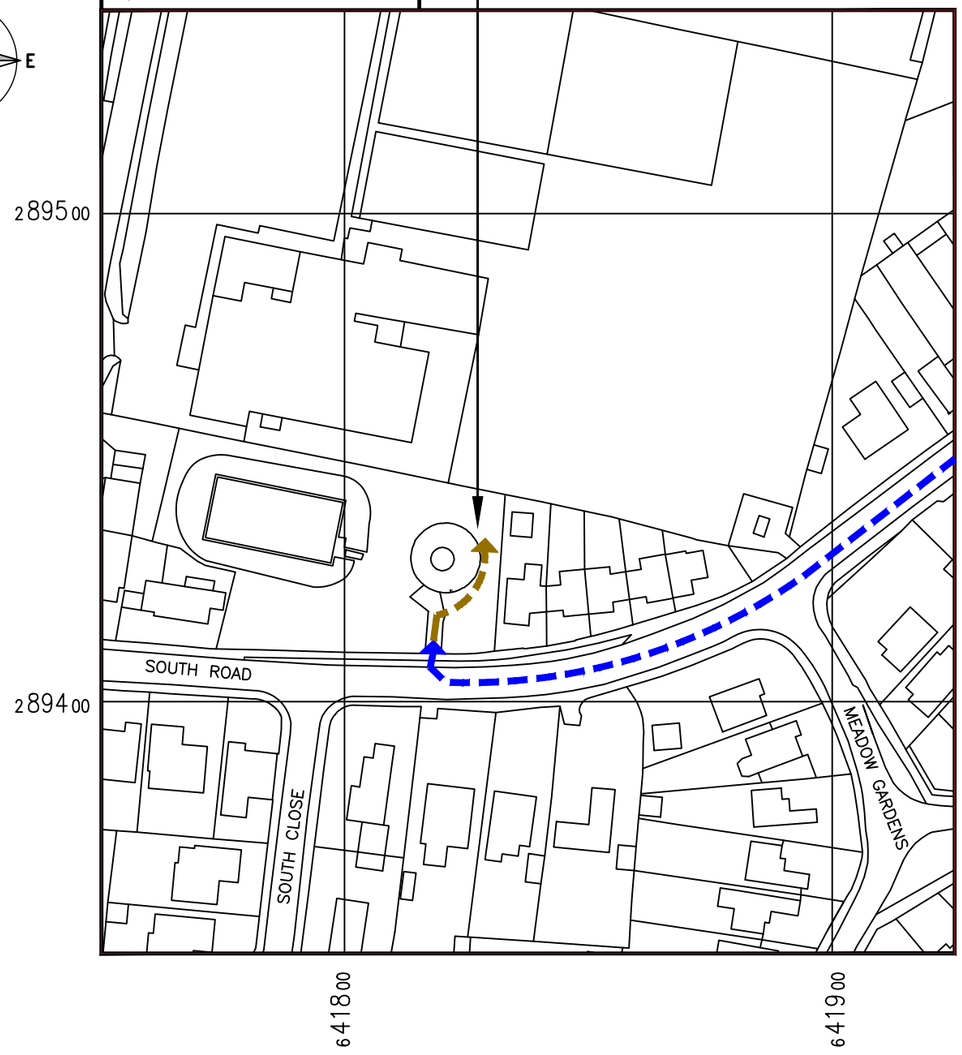

DETAILED SITE LOCATION
(Scale 1:1250)

Based upon Ordnance Survey map extract with the permission of the Controller of Her Majesty's Stationery Office. Crown copyright. Licence No. 100022432

0 25m 50m 75m
1:1250

ALL DIMENSIONS ARE IN mm UNLESS NOTED OTHERWISE

N.G.R	E: 641826	N: 289433	

NOTES:

DIRECTIONS TO SITE:
FROM A146 TURN LEFT ONTO A145 AND CONTINUE FOR APPROX 0.75km. TURN RIGHT ONTO A145 STATION ROAD AND CONTINUE TO END. TURN LEFT ONTO A145 LONDON ROAD AND CONTINUE FOR APPROX 1.0km BEFORE TURNING RIGHT ONTO SOUTH ROAD. WATER TOWER IS APPROX 500m FURTHER UP ON THE RIGHT.

REV	MODIFICATION	BY	CH	DATE
A	PLANNING ISSUE	BP	DCC	14.11.25

circet UK
Unit 27F-G, Hartlebury Trading Estate, Crown Lane, Hartlebury, Worcestershire, DY10 4JD

cornerstone

Cell Name	Opt.
SOUTH WATER TOWER	–

Cell ID No

CSID	– VF	– TEF
11482824	–	036507
Project No.	– TM Cell ID	– N/A
–	–	–

Site Address / Contact Details

WATER TOWER
SOUTH ROAD
BECCLES
NORFOLK
NR34 9NZ

Drawing Title: SITE LOCATION MAPS


Purpose of issue: PLANNING — Dwg Rev: A

Drawing Number: 100

Surveyed By: CIRCET — Original Sheet Size: A3 — Pack Issue: A

Drawn:	Date:	Checked:	Date:
BP	14.11.25	DCC	14.11.25


SITE LOCATION
W3W:
noun.narrating.shortcuts

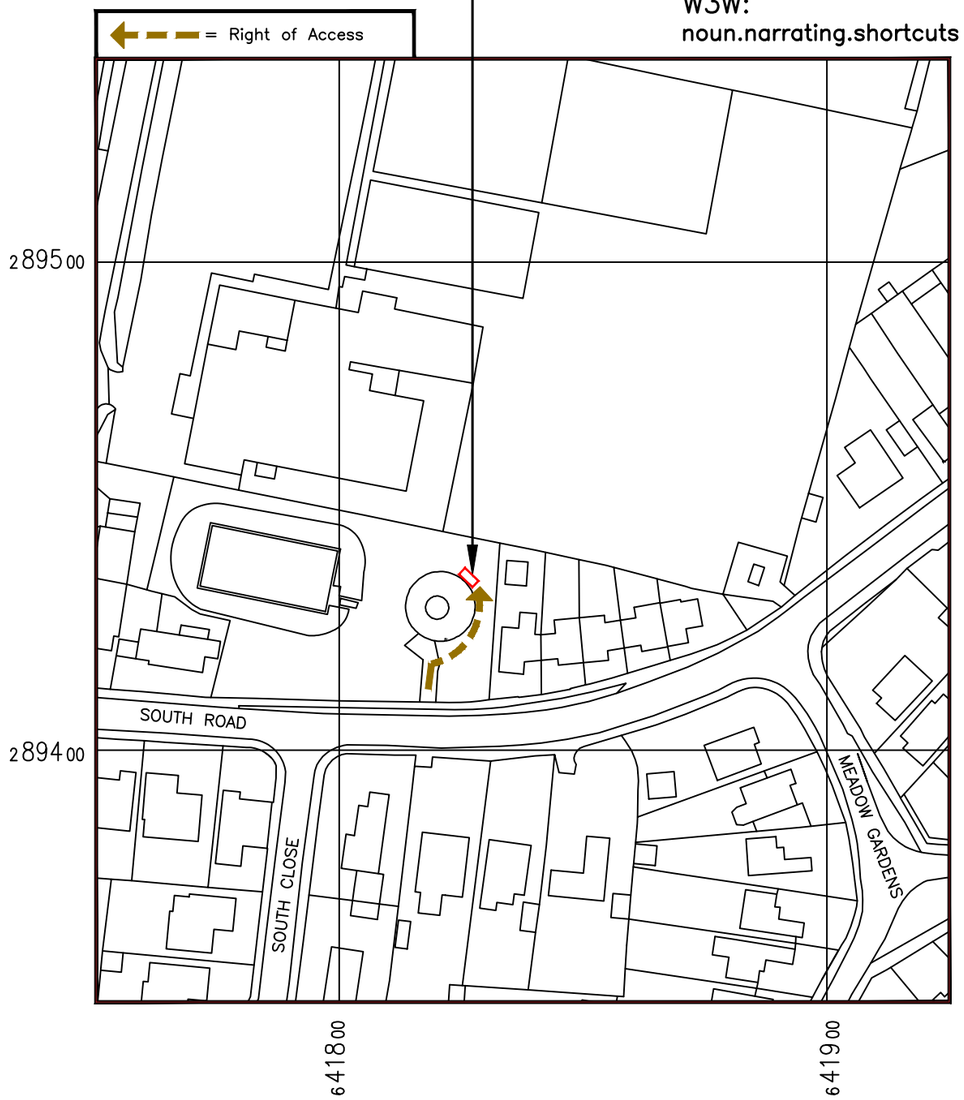

DETAILED SITE LOCATION
(Scale 1:1250)

Based upon Ordnance Survey map extract with the permission of the Controller of Her Majesty's Stationery Office. Crown copyright. Licence No. 100022432

0 25m 50m 75m
1:1250

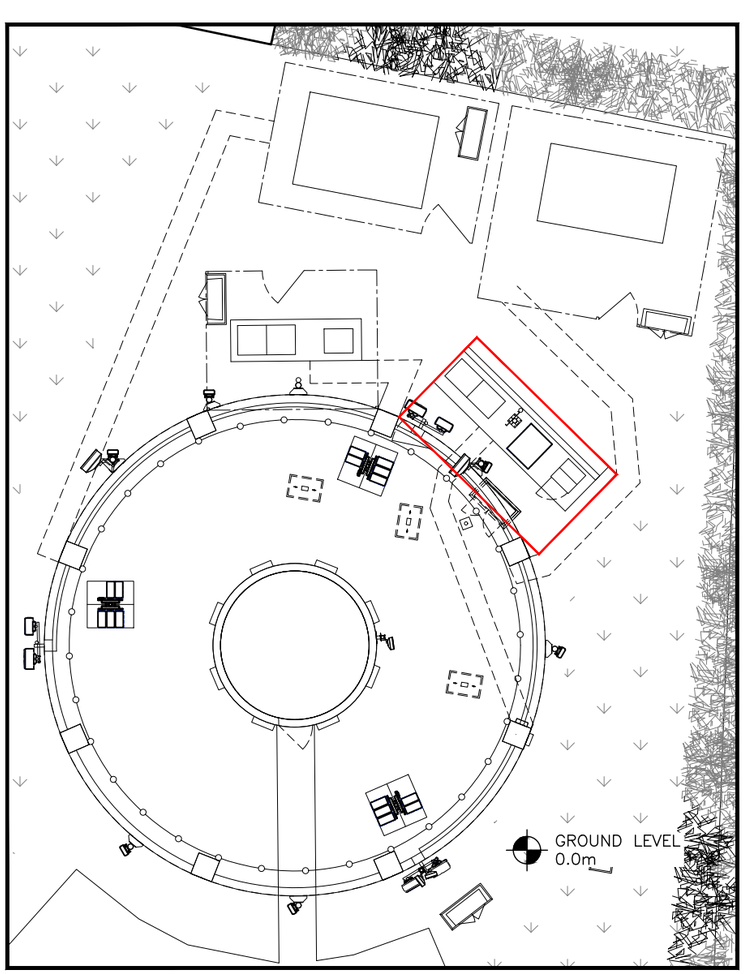

SITE PLAN
(Scale 1:150)

0 1.5 3 4.5 6 7.5m
1:150

ALL DIMENSIONS ARE IN mm UNLESS NOTED OTHERWISE

N.G.R | E: 641826 | N: 289433

NOTES:

REV	MODIFICATION	BY	CH	DATE
A	PLANNING ISSUE	BP	DCC	14.11.25

circet UK
Unit 27F-G, Hartlebury Trading Estate, Crown Lane, Hartlebury, Worcestershire, DY10 4JD

cornerstone

Cell Name	Opt.
SOUTH WATER TOWER	–

Cell ID No

CSID	– VF	– TEF
11482824	–	036507
Project No.	– TM Cell ID	– N/A
–	–	–

Site Address / Contact Details

WATER TOWER
SOUTH ROAD
BECCLES
NORFOLK
NR34 9NZ


Drawing Title: LEASE AGREEMENT PLAN

Purpose of issue: PLANNING — Dwg Rev: A

Drawing Number: 101

Surveyed By:	Original Sheet Size:	Pack Issue:
CIRCET	A3	A

Drawn:	Date:	Checked:	Date:
BP	14.11.25	DCC	14.11.25

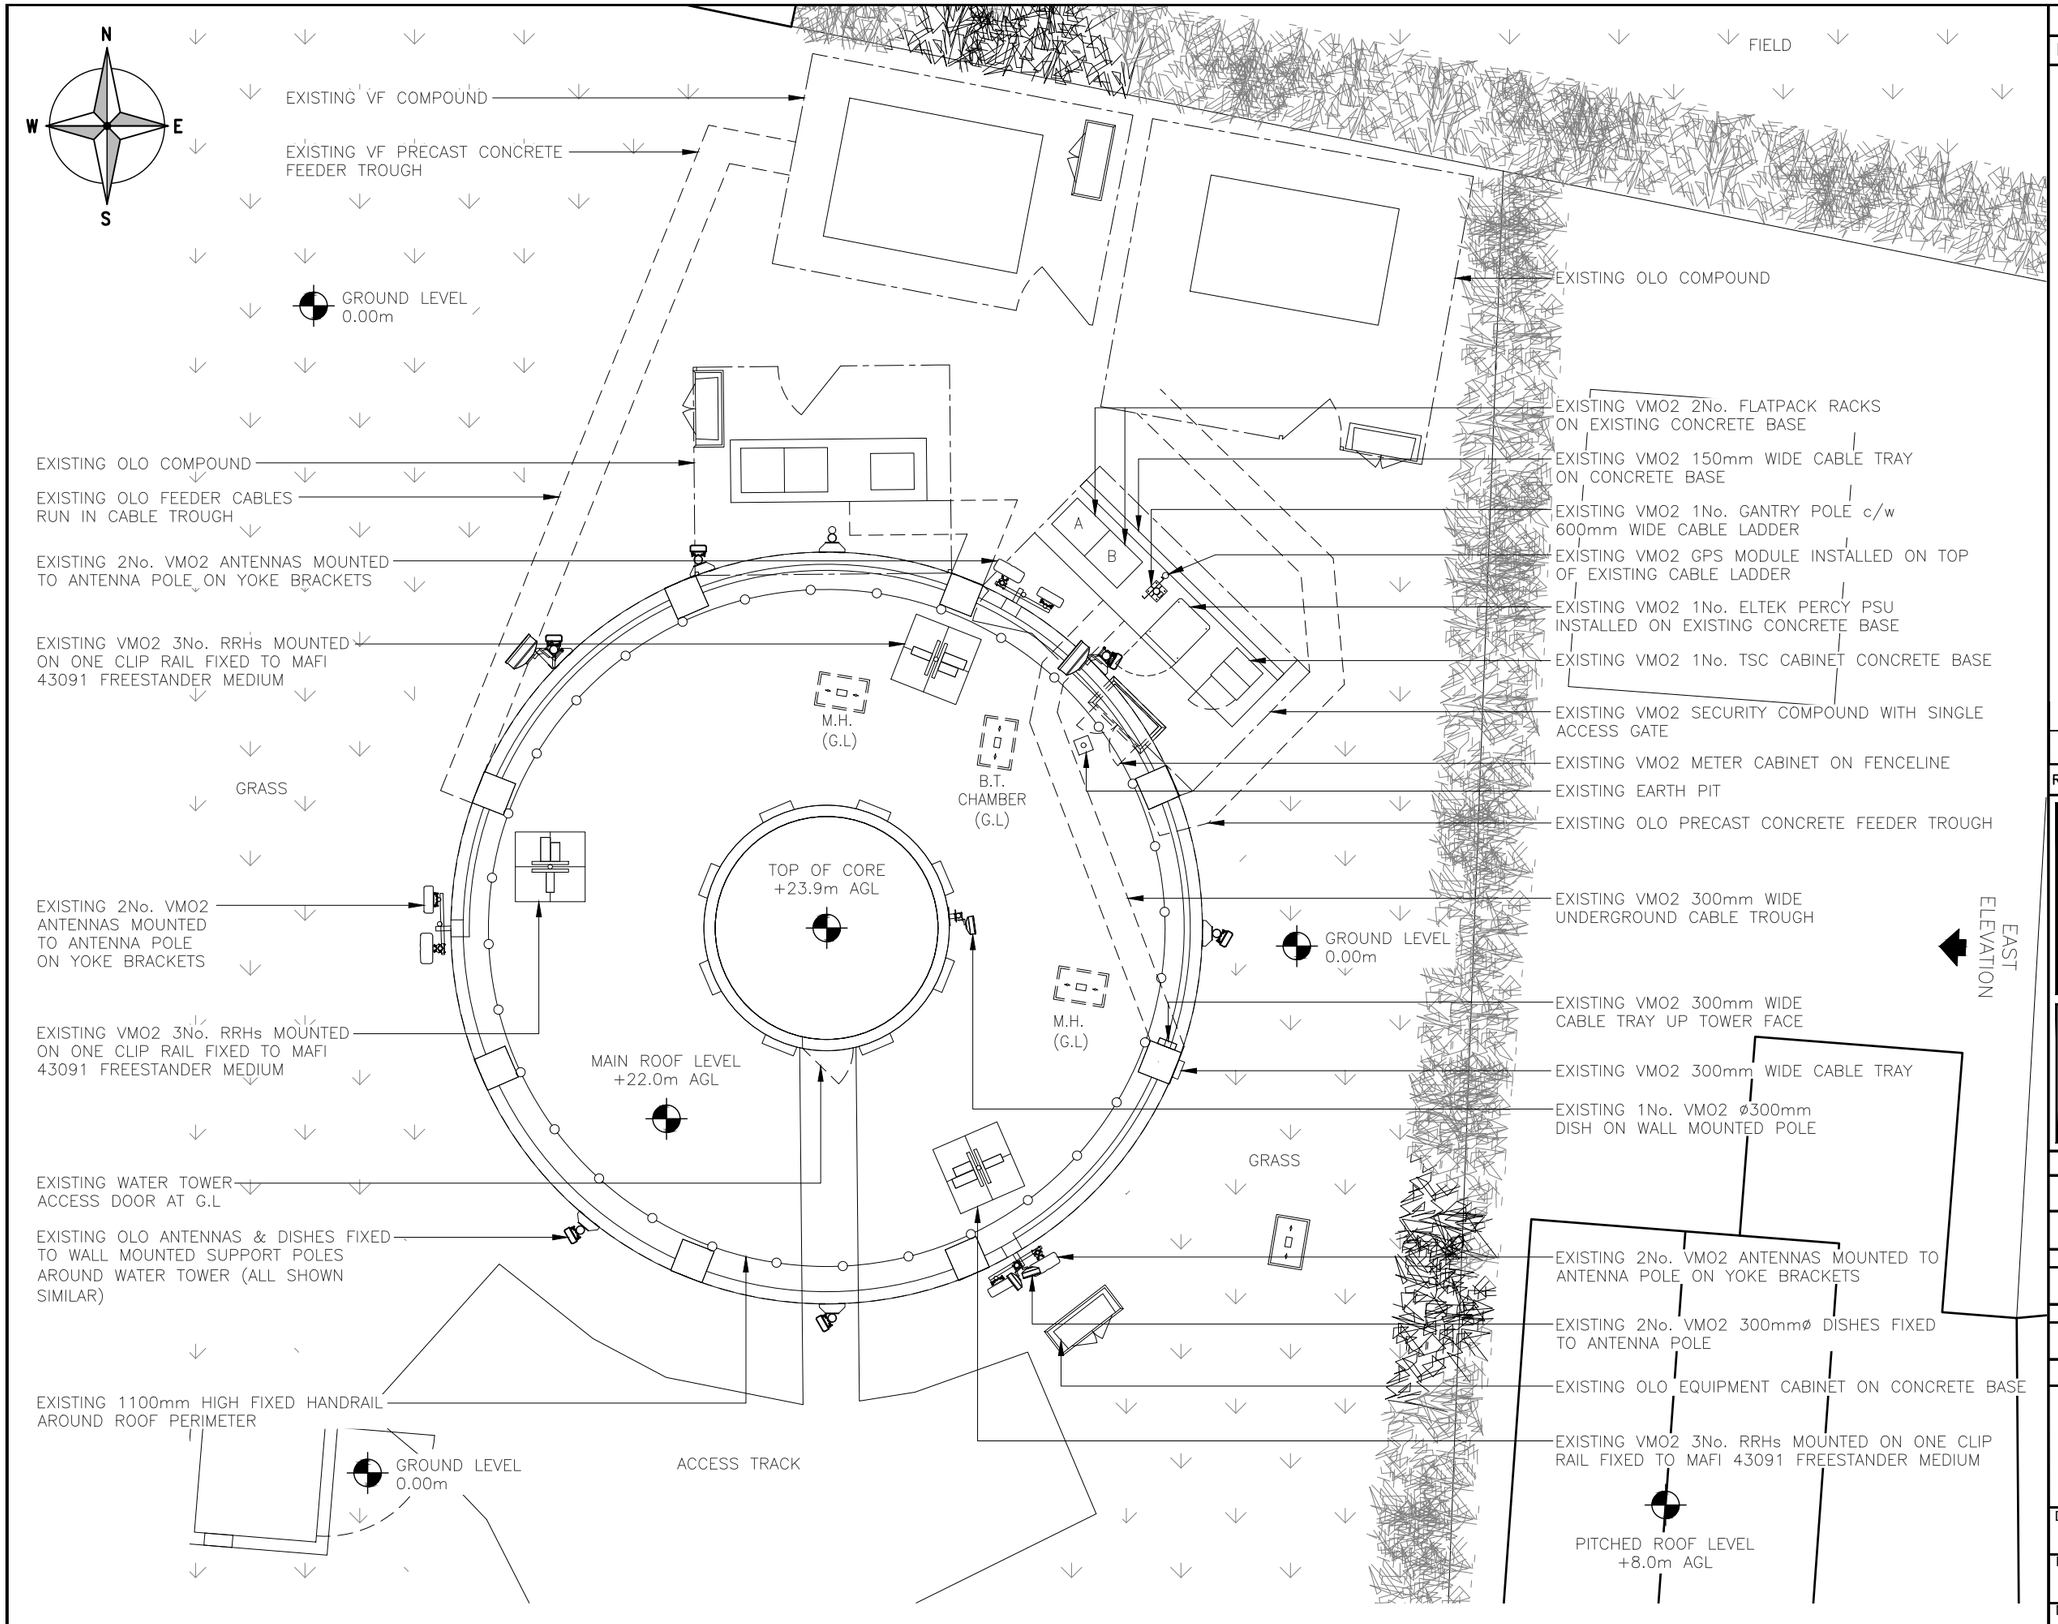

EXISTING SITE PLAN

(1:100)

0 1 2 3 4 5m

1:100

ALL DIMENSIONS ARE IN mm UNLESS NOTED OTHERWISE

N.G.R | E: 641826 | N: 289433

NOTES:

REV	MODIFICATION	BY	CH	DATE
A	PLANNING ISSUE	BP	DCC	14.11.25

circet UK
Unit 27F-G, Hartlebury Trading Estate, Crown Lane, Hartlebury, Worcestershire, DY10 4JD

cornerstone

Cell Name	Opt.
SOUTH WATER TOWER	–

Cell ID No

CSID	– VF	– TEF
11482824	–	036507
Project No.	– TM Cell ID	– N/A
–	–	–

Site Address / Contact Details


WATER TOWER
SOUTH ROAD
BECCLES
NORFOLK
NR34 9NZ

Drawing Title: EXISTING SITE PLAN

Purpose of issue:	Dwg Rev:
PLANNING	A

Drawing Number:	Original Sheet Size:	Pack Issue:
200	A3	A

Surveyed By:	Drawn:	Date:	Checked:	Date:
CIRCET	BP	14.11.25	DCC	14.11.25

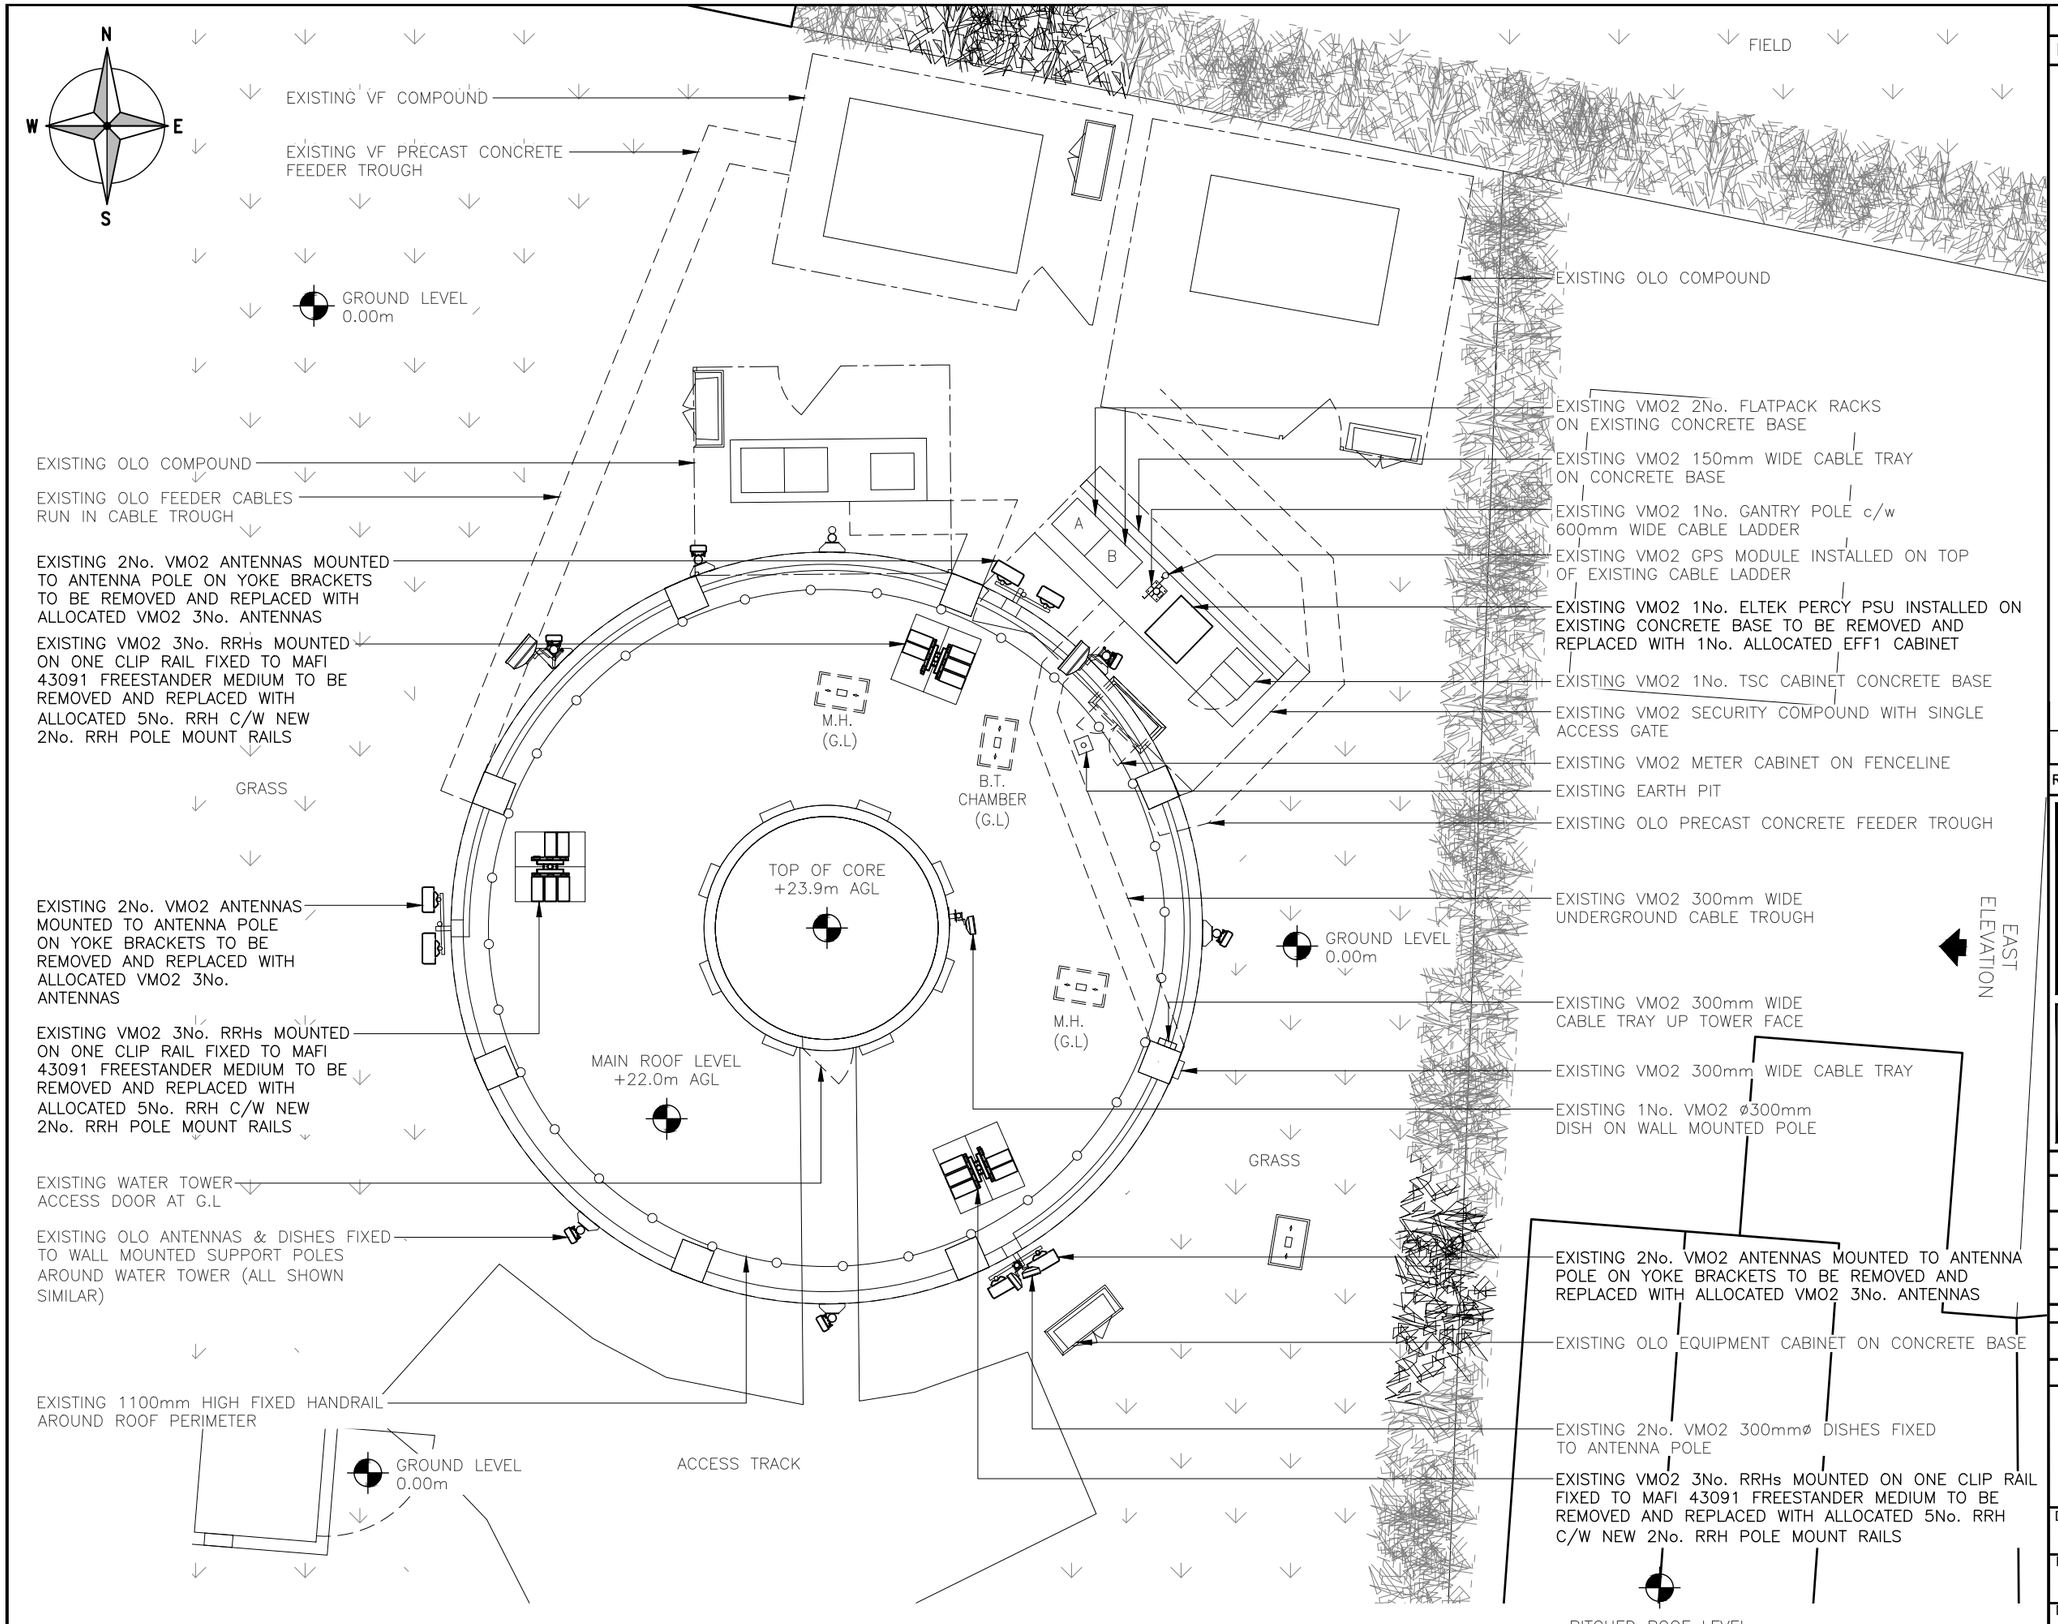

PROPOSED SITE PLAN
(1:100)

ALL DIMENSIONS ARE IN mm UNLESS NOTED OTHERWISE

N.G.R | E: 641826 | N: 289433

NOTES:

REV	MODIFICATION	BY	CH	DATE
A	PLANNING ISSUE	BP	DCC	14.11.25

circet UK
Unit 27F-G, Hartlebury Trading Estate, Crown Lane, Hartlebury, Worcestershire, DY10 4JD

cornerstone

Cell Name	Opt.
SOUTH WATER TOWER	–

Cell ID No

CSID	– VF	– TEF
11482824	–	036507
Project No.	– TM Cell ID	– N/A
–	–	–

Site Address / Contact Details


WATER TOWER
SOUTH ROAD
BECCLES
NORFOLK
NR34 9NZ

Drawing Title: PROPOSED SITE PLAN

Purpose of issue:	Dwg Rev:
PLANNING	A

Drawing Number:	Original Sheet Size:	Pack Issue:
201	A3	A

Surveyed By:		Drawn:	Date:	Checked:	Date:
CIRCET		BP	14.11.25	DCC	14.11.25

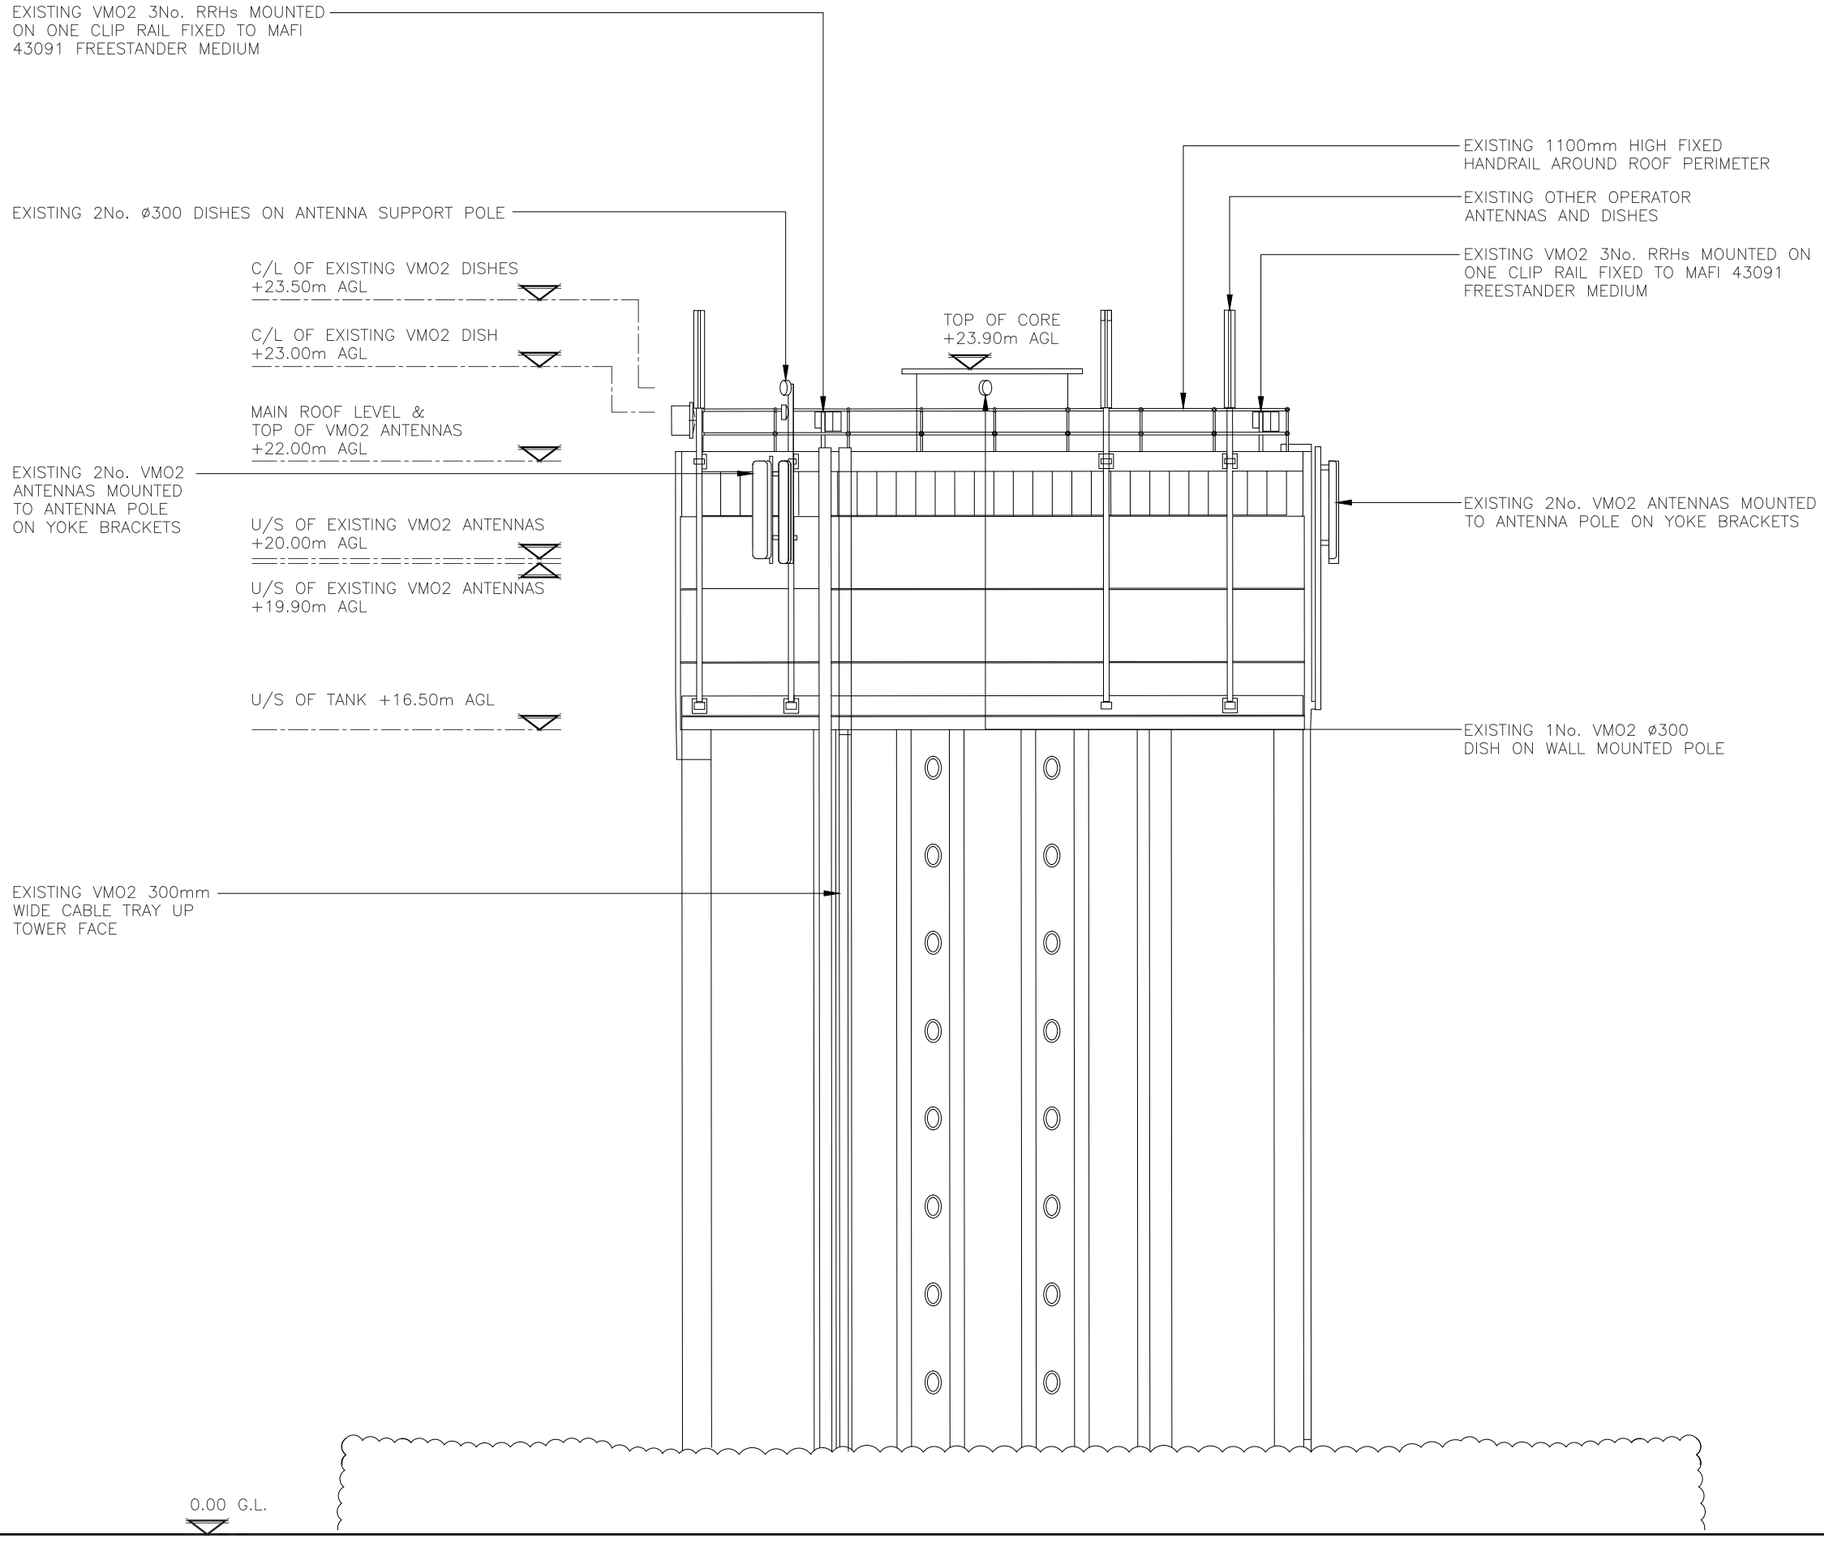

EXISTING SITE EAST ELEVATION

(1:125)

0 1.25 2.5 3.75 5 6.25m
1:125

ALL DIMENSIONS ARE IN mm UNLESS NOTED OTHERWISE

N.G.R E: 641826 N: 289433

NOTES:

REV	MODIFICATION	BY	CH	DATE
A	PLANNING ISSUE	BP	DCC	14.11.25

circet UK
Unit 27F-G, Hartlebury Trading Estate, Crown Lane, Hartlebury, Worcestershire, DY10 4JD

cornerstone

Cell Name	Opt.
SOUTH WATER TOWER	–

Cell ID No

CSID	– VF	– TEF
11482824	–	036507
Project No.	– TM Cell ID	– N/A
–	–	–

Site Address / Contact Details

WATER TOWER
SOUTH ROAD
BECCLES
NORFOLK
NR34 9NZ


Drawing Title: EXISTING ELEVATION

Purpose of issue: PLANNING — Dwg Rev: A

Drawing Number: 300

Surveyed By:	Original Sheet Size:	Pack Issue:
CIRCET	A3	A

Drawn:	Date:	Checked:	Date:
BP	14.11.25	DCC	14.11.25

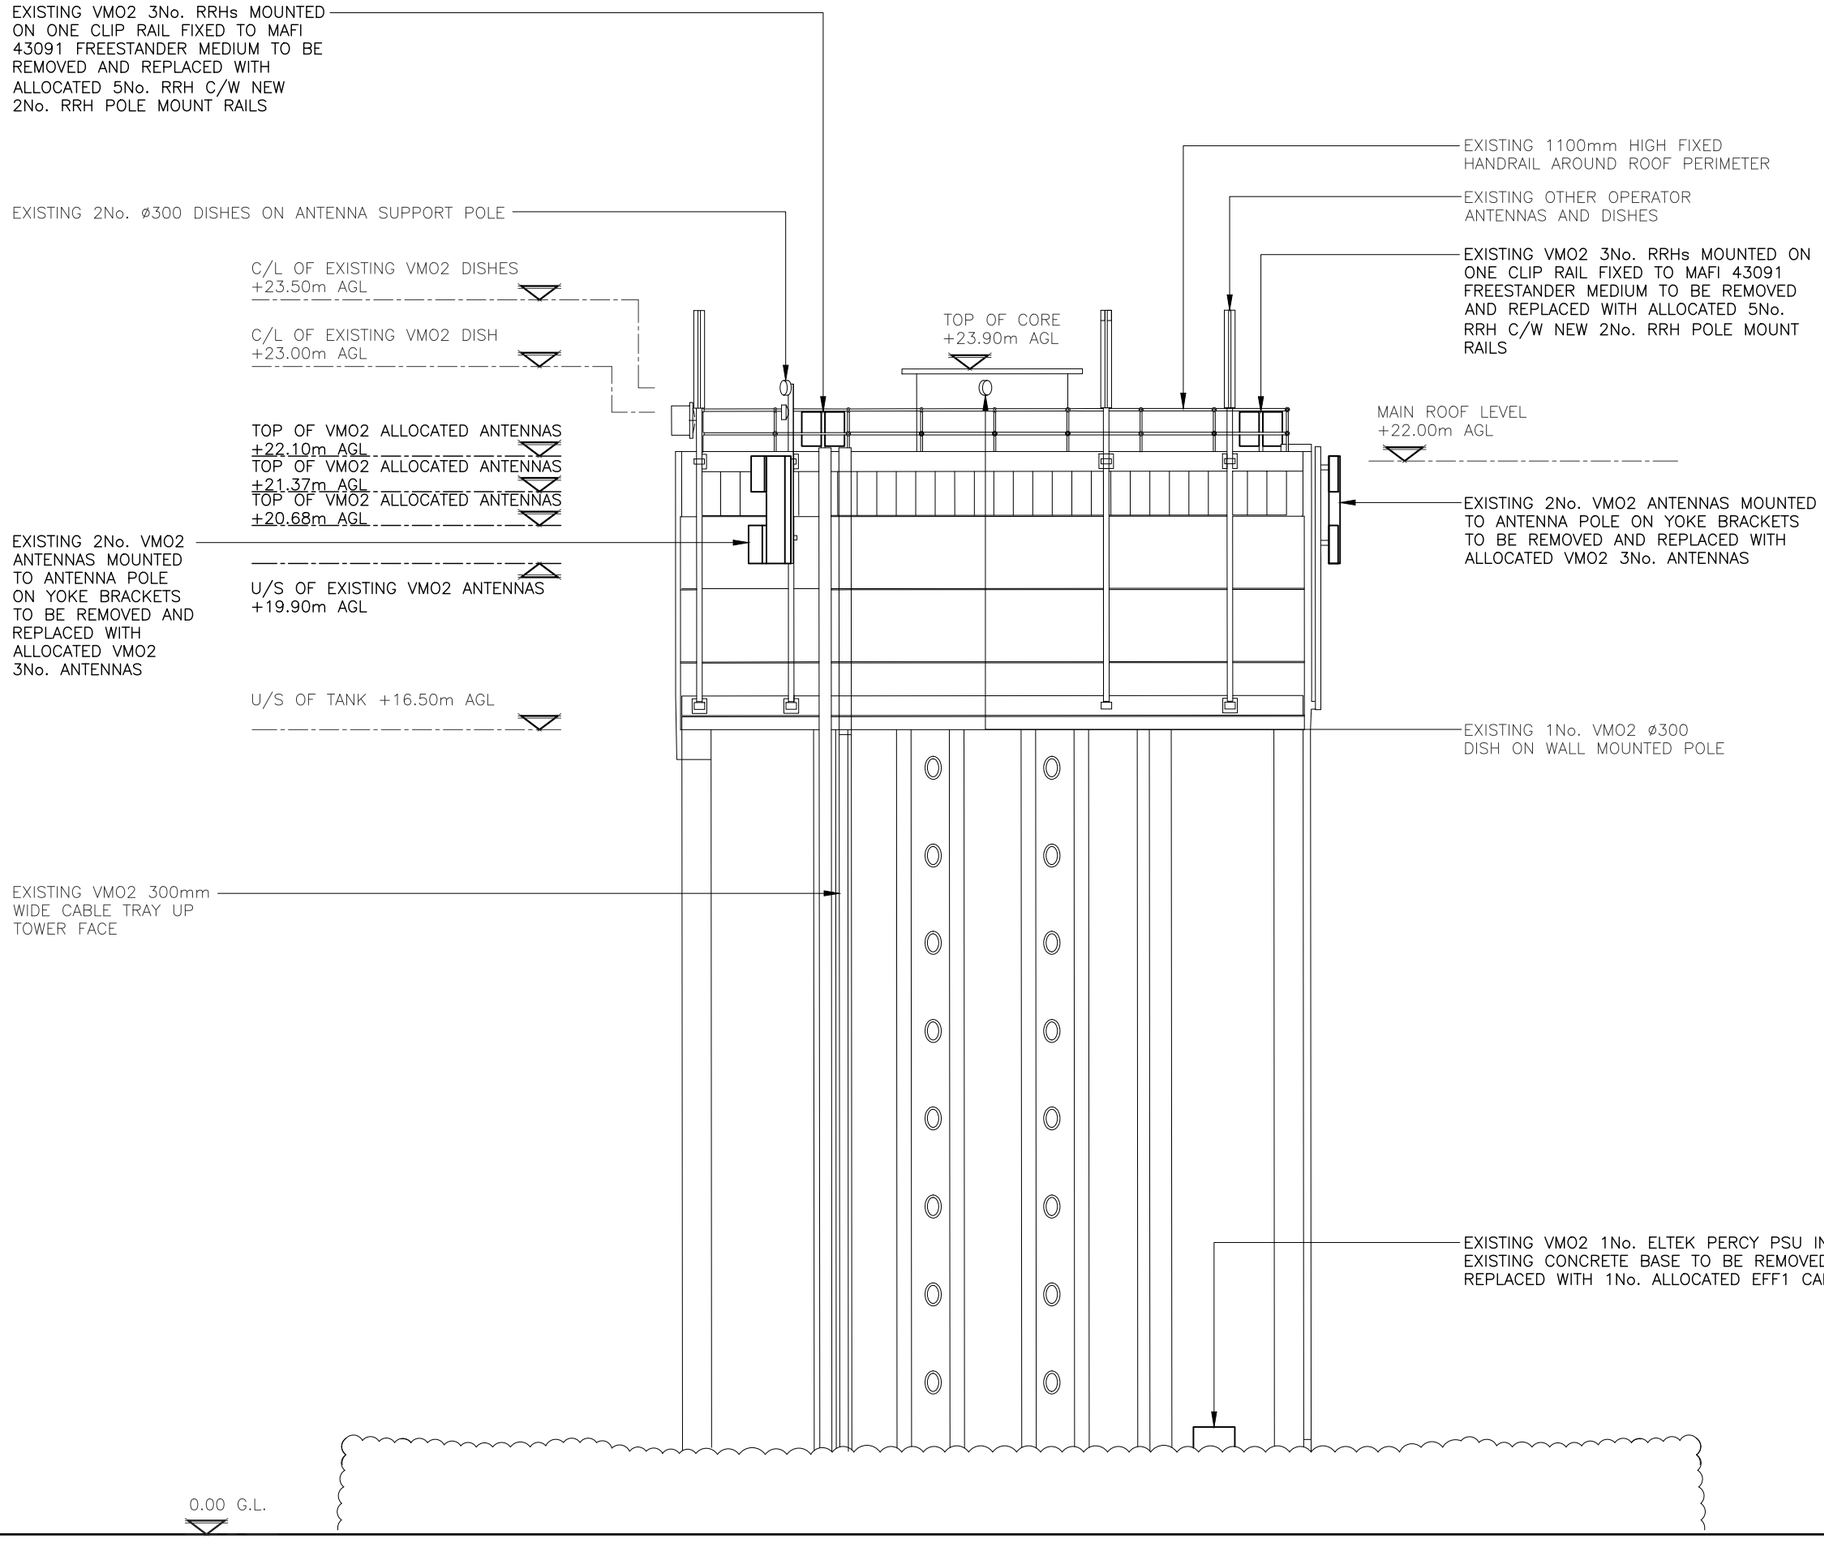

PROPOSED SITE EAST ELEVATION

(1:125)

0 1.25 2.5 3.75 5 6.25m
1:125

ALL DIMENSIONS ARE IN mm UNLESS NOTED OTHERWISE

N.G.R E: 641826 N: 289433

NOTES:

REV	MODIFICATION	BY	CH	DATE
A	PLANNING ISSUE	BP	DCC	14.11.25

circet UK
Unit 27F-G, Hartlebury Trading Estate, Crown Lane, Hartlebury, Worcestershire, DY10 4JD

cornerstone

Cell Name	Opt.
SOUTH WATER TOWER	–

Cell ID No

CSID	– VF	– TEF
11482824	–	036507
Project No.	– TM Cell ID	– N/A
–	–	–

Site Address / Contact Details

WATER TOWER
SOUTH ROAD
BECCLES
NORFOLK
NR34 9NZ


Drawing Title: PROPOSED SITE ELEVATION

Purpose of issue:	Dwg Rev:
PLANNING	
Drawing Number: 301	A


Surveyed By:	Original Sheet Size:	Pack Issue:
CIRCET	A3	

Drawn:	Date:	Checked:	Date:	
BP	14.11.25	DCC	14.11.25	A


ITEM DESCRIPTION	QTY
EXISTING ANTENNAS	6
ITEM DESCRIPTION	QTY
EXISTING RRU	9

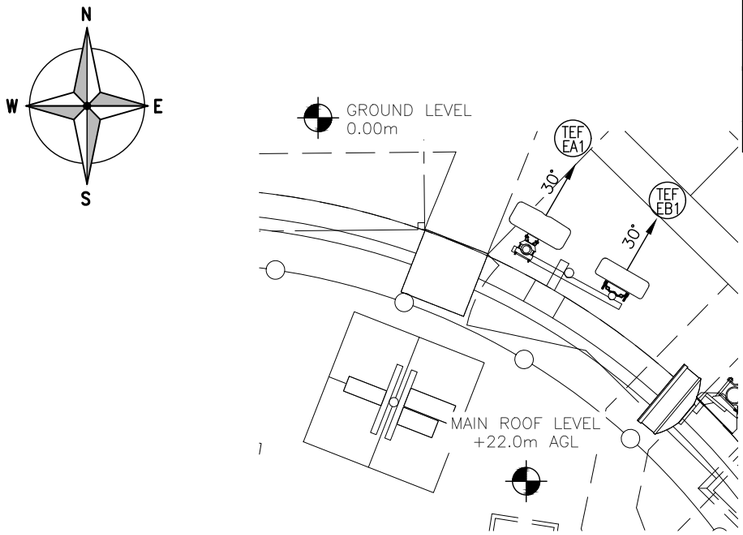

EXISTING S1 ANTENNA/RRU PLAN @19.9m/22.6m AGL
(1:50)

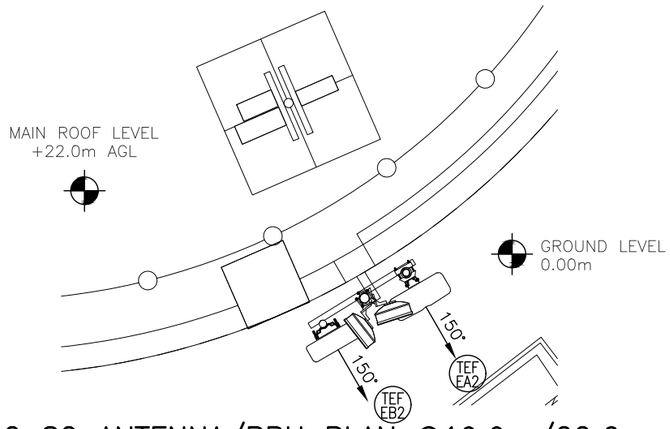

EXISTING S2 ANTENNA/RRU PLAN @19.9m/22.6m AGL
(1:50)

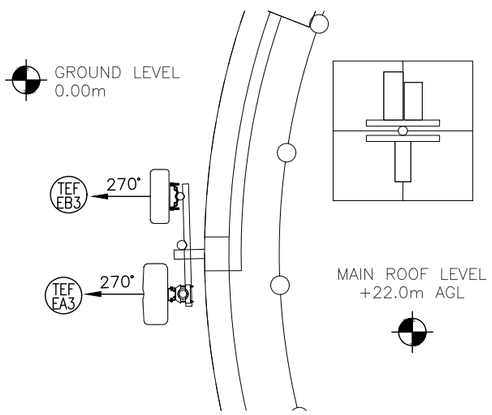


EXISTING S3 ANTENNA/RRU PLAN @19.9m/22.6m AGL
(1:50)


0 0.5 1 1.5 2 2.5m
1:50

ITEM DESCRIPTION	QTY
EXISTING DISH	3



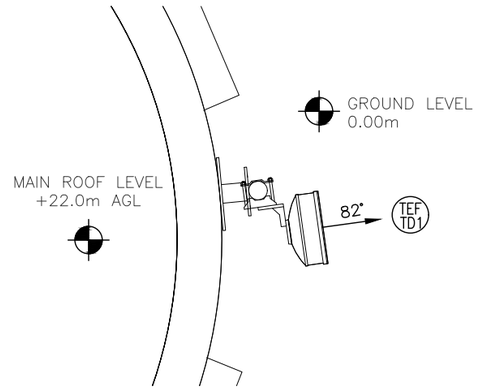

EXISTING DISH PLAN @23.5m AGL
(1:25)

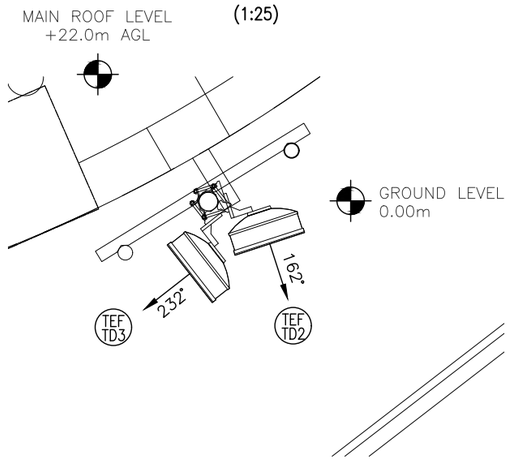

EXISTING DISH PLAN @23.0m AGL
(1:25)

0 0.25 0.5 0.75 1 1.25m
1:25

EXISTING DISH SCHEDULE

STATUS	OPERATOR	DISH REF	DESIGN REFERENCE	DIMENSIONS (ØxD)	DISH BEARING (°)	LOCATION	HEIGHT (C/L)
EXISTING	VM02	TD1	–	300mmØ	82°	DISH POLE	+23.5m
EXISTING	VM02	TD2	–	300mmØ	162°	ANTENNA POLE	+23.5m
EXISTING	VM02	TD3	–	300mmØ	232°	ANTENNA POLE	+23.0m

ALL DIMENSIONS ARE IN mm UNLESS NOTED OTHERWISE

N.G.R E: 641826 N: 289433

EQUIPMENT COLOUR KEY

EXISTING EQUIPMENT	
TEF EQUIPMENT ALLOCATED	
TEF PROPOSED EQUIPMENT	
NEUTRAL FOOTPRINT	

REV	MODIFICATION	BY	CH	DATE
A	PLANNING ISSUE	BP	DCC	14.11.25

circet UK
Unit 27F-G, Hartlebury Trading Estate, Crown Lane, Hartlebury, Worcestershire, DY10 4JD

cornerstone

Cell Name	Opt.
SOUTH WATER TOWER	–

Cell ID No

CSID	– VF	– TEF
11482824	–	036507
Project No.	– TM Cell ID	– N/A
–	–	–

Site Address / Contact Details

WATER TOWER
SOUTH ROAD
BECCLES
NORFOLK
NR34 9NZ

Drawing Title: EXISTING ANTENNA PLAN

Purpose of issue:	Dwg Rev:
PLANNING	A


Drawing Number:	Pack Issue:
400	A

Surveyed By:	Original Sheet Size:	
CIRCET	A3	

Drawn:	Date:	Checked:	Date:
BP	14.11.25	DCC	14.11.25

ITEM DESCRIPTION	QTY	ITEM DESCRIPTION	QTY
RFF1n	4	AFF3	3
RFF2n	1	AFF1	3
		AFF6	3



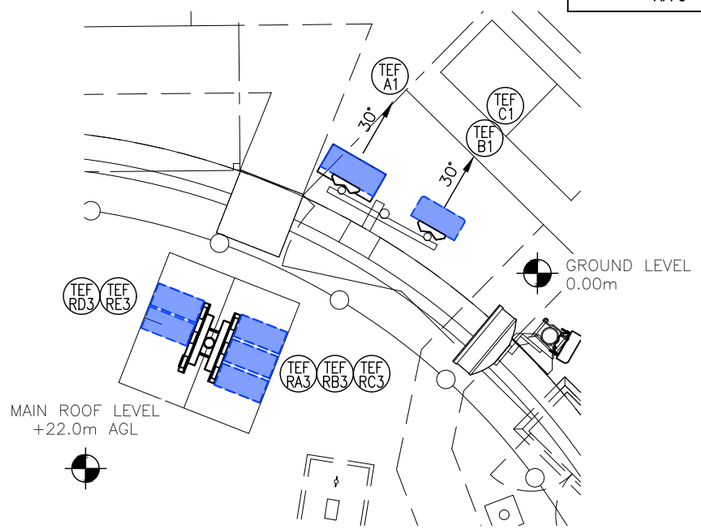


ALLOCATED S1 ANTENNA/RRU PLAN @19.9m/22.6m AGL

(1:50)

0 0.5 1 1.5 2 2.5m
1:50

ITEM DESCRIPTION	QTY	ITEM DESCRIPTION	QTY
RFF1n	4	AFF3	3
RFF2n	1	AFF1	3
		AFF6	3



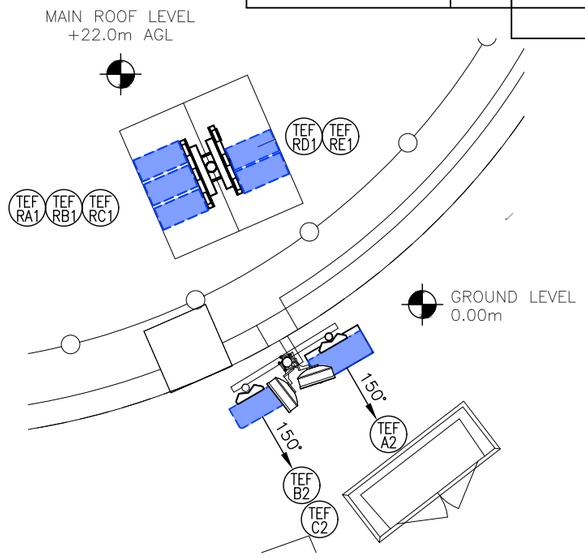


ALLOCATED S2 ANTENNA/RRU PLAN @19.9m/22.6m AGL

(1:50)

0 0.5 1 1.5 2 2.5m
1:50

ITEM DESCRIPTION	QTY	ITEM DESCRIPTION	QTY
RFF1n	4	AFF3	3
RFF2n	1	AFF1	3
		AFF6	3



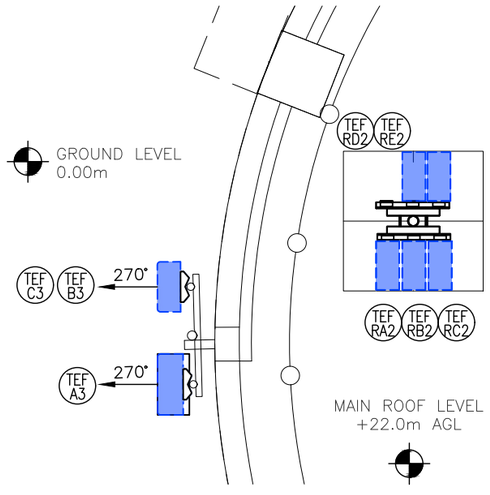

ALLOCATED S1 ANTENNA/RRU PLAN @19.9m/22.6m AGL

(1:50)

0 0.5 1 1.5 2 2.5m
1:50

ALL DIMENSIONS ARE IN mm UNLESS NOTED OTHERWISE

N.G.R E: 641826 N: 289433

EQUIPMENT COLOUR KEY

EXISTING EQUIPMENT	
TEF EQUIPMENT ALLOCATED	
TEF PROPOSED EQUIPMENT	
NEUTRAL FOOTPRINT	

REV	MODIFICATION	BY	CH	DATE
A	PLANNING ISSUE	BP	DCC	14.11.25

circet UK
Unit 27F-G, Hartlebury Trading Estate, Crown Lane, Hartlebury, Worcestershire, DY10 4JD

cornerstone

Cell Name	Opt.
SOUTH WATER TOWER	–

Cell ID No

CSID	– VF	– TEF
11482824	–	036507
Project No.	– TM Cell ID	– N/A
–	–	–

Site Address / Contact Details

WATER TOWER
SOUTH ROAD
BECCLES
NORFOLK
NR34 9NZ

Drawing Title: ALLOCATED ANTENNA/RRU PLAN

Purpose of issue:	Dwg Rev:
PLANNING	A
Drawing Number: 401	

Surveyed By:	Original Sheet Size:	Pack Issue:
CIRCET	A3	A

Drawn:	Date:	Checked:	Date:
BP	14.11.25	DCC	14.11.25


ITEM	DESCRIPTION	QTY
	EFF1	1

ALL DIMENSIONS ARE IN mm UNLESS NOTED OTHERWISE

N.G.R E: 641826 N: 289433

EQUIPMENT COLOUR KEY

EXISTING EQUIPMENT	
TEF EQUIPMENT ALLOCATED	
TEF PROPOSED EQUIPMENT	
NEUTRAL FOOTPRINT	

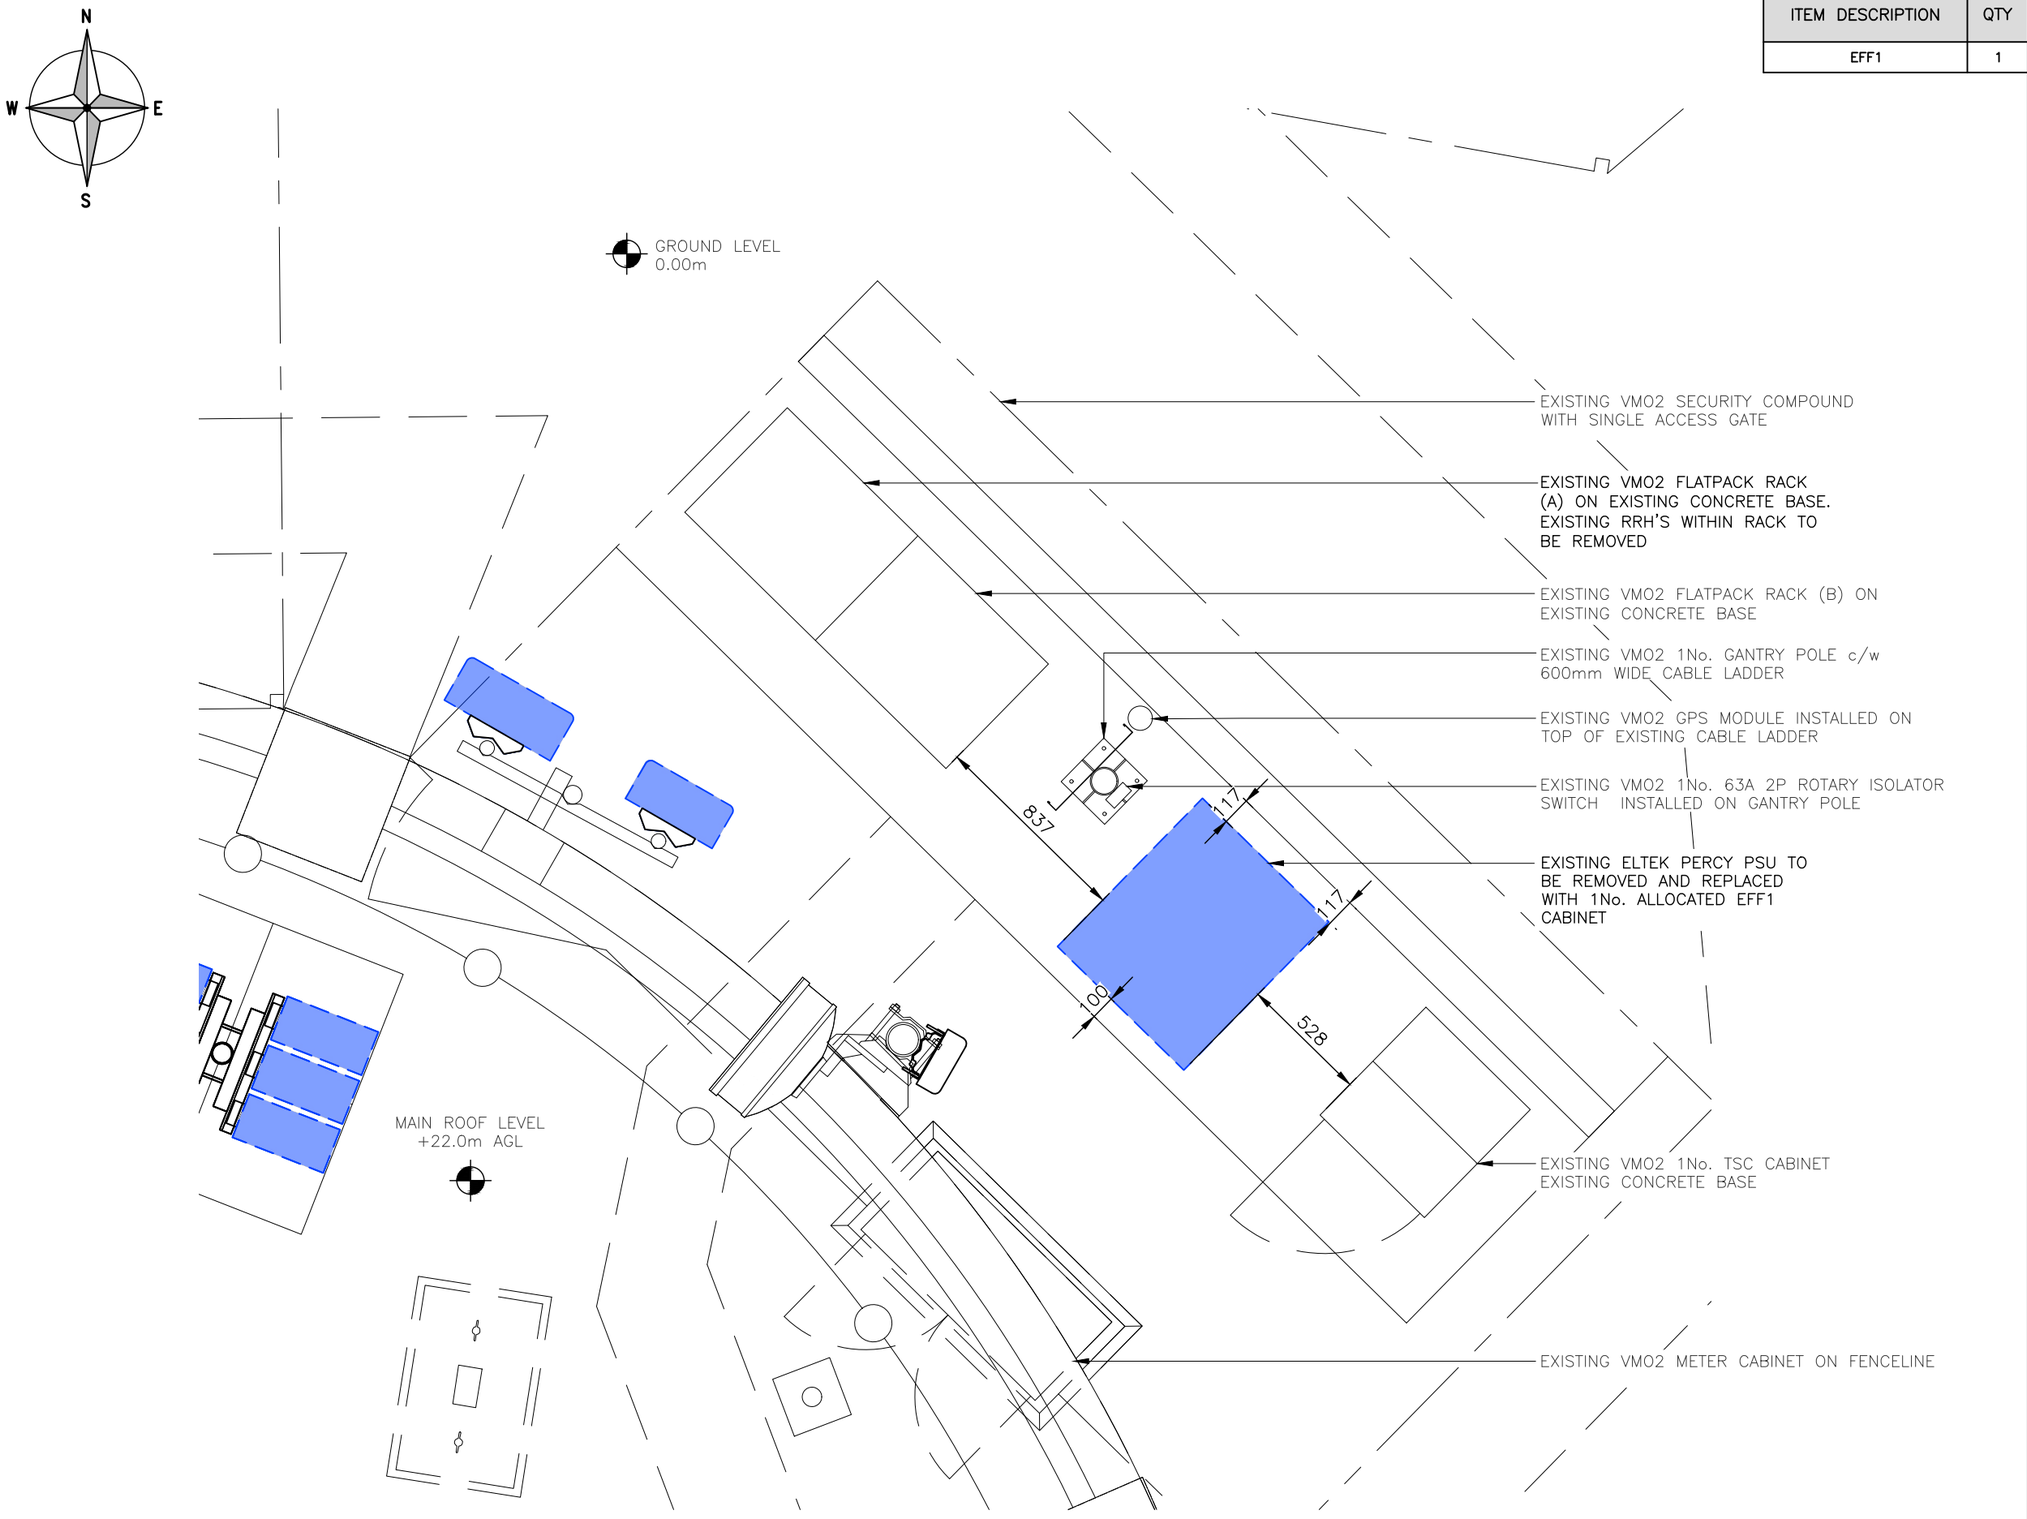

ALLOCATED EQUIPMENT
(1:25)

0 0.25 0.5 0.75 1 1.25m
1:25

REV	MODIFICATION	BY	CH	DATE
A	PLANNING ISSUE	BP	DCC	14.11.25

circet UK
Unit 27F-G, Hartlebury Trading Estate, Crown Lane, Hartlebury, Worcestershire, DY10 4JD

cornerstone

Cell Name	Opt.
SOUTH WATER TOWER	–

Cell ID No

CSID	VF	TEF
11482824	–	036507
Project No.	TM Cell ID	N/A
–	–	–

Site Address / Contact Details

WATER TOWER
SOUTH ROAD
BECCLES
NORFOLK
NR34 9NZ


Drawing Title: ALLOCATED EQUIPMENT PLAN

Purpose of issue:	Dwg Rev:
PLANNING	A

Drawing Number: 402

Surveyed By:	Original Sheet Size:	Pack Issue:
CIRCET	A3	A

Drawn:	Date:	Checked:	Date:
BP	14.11.25	DCC	14.11.25

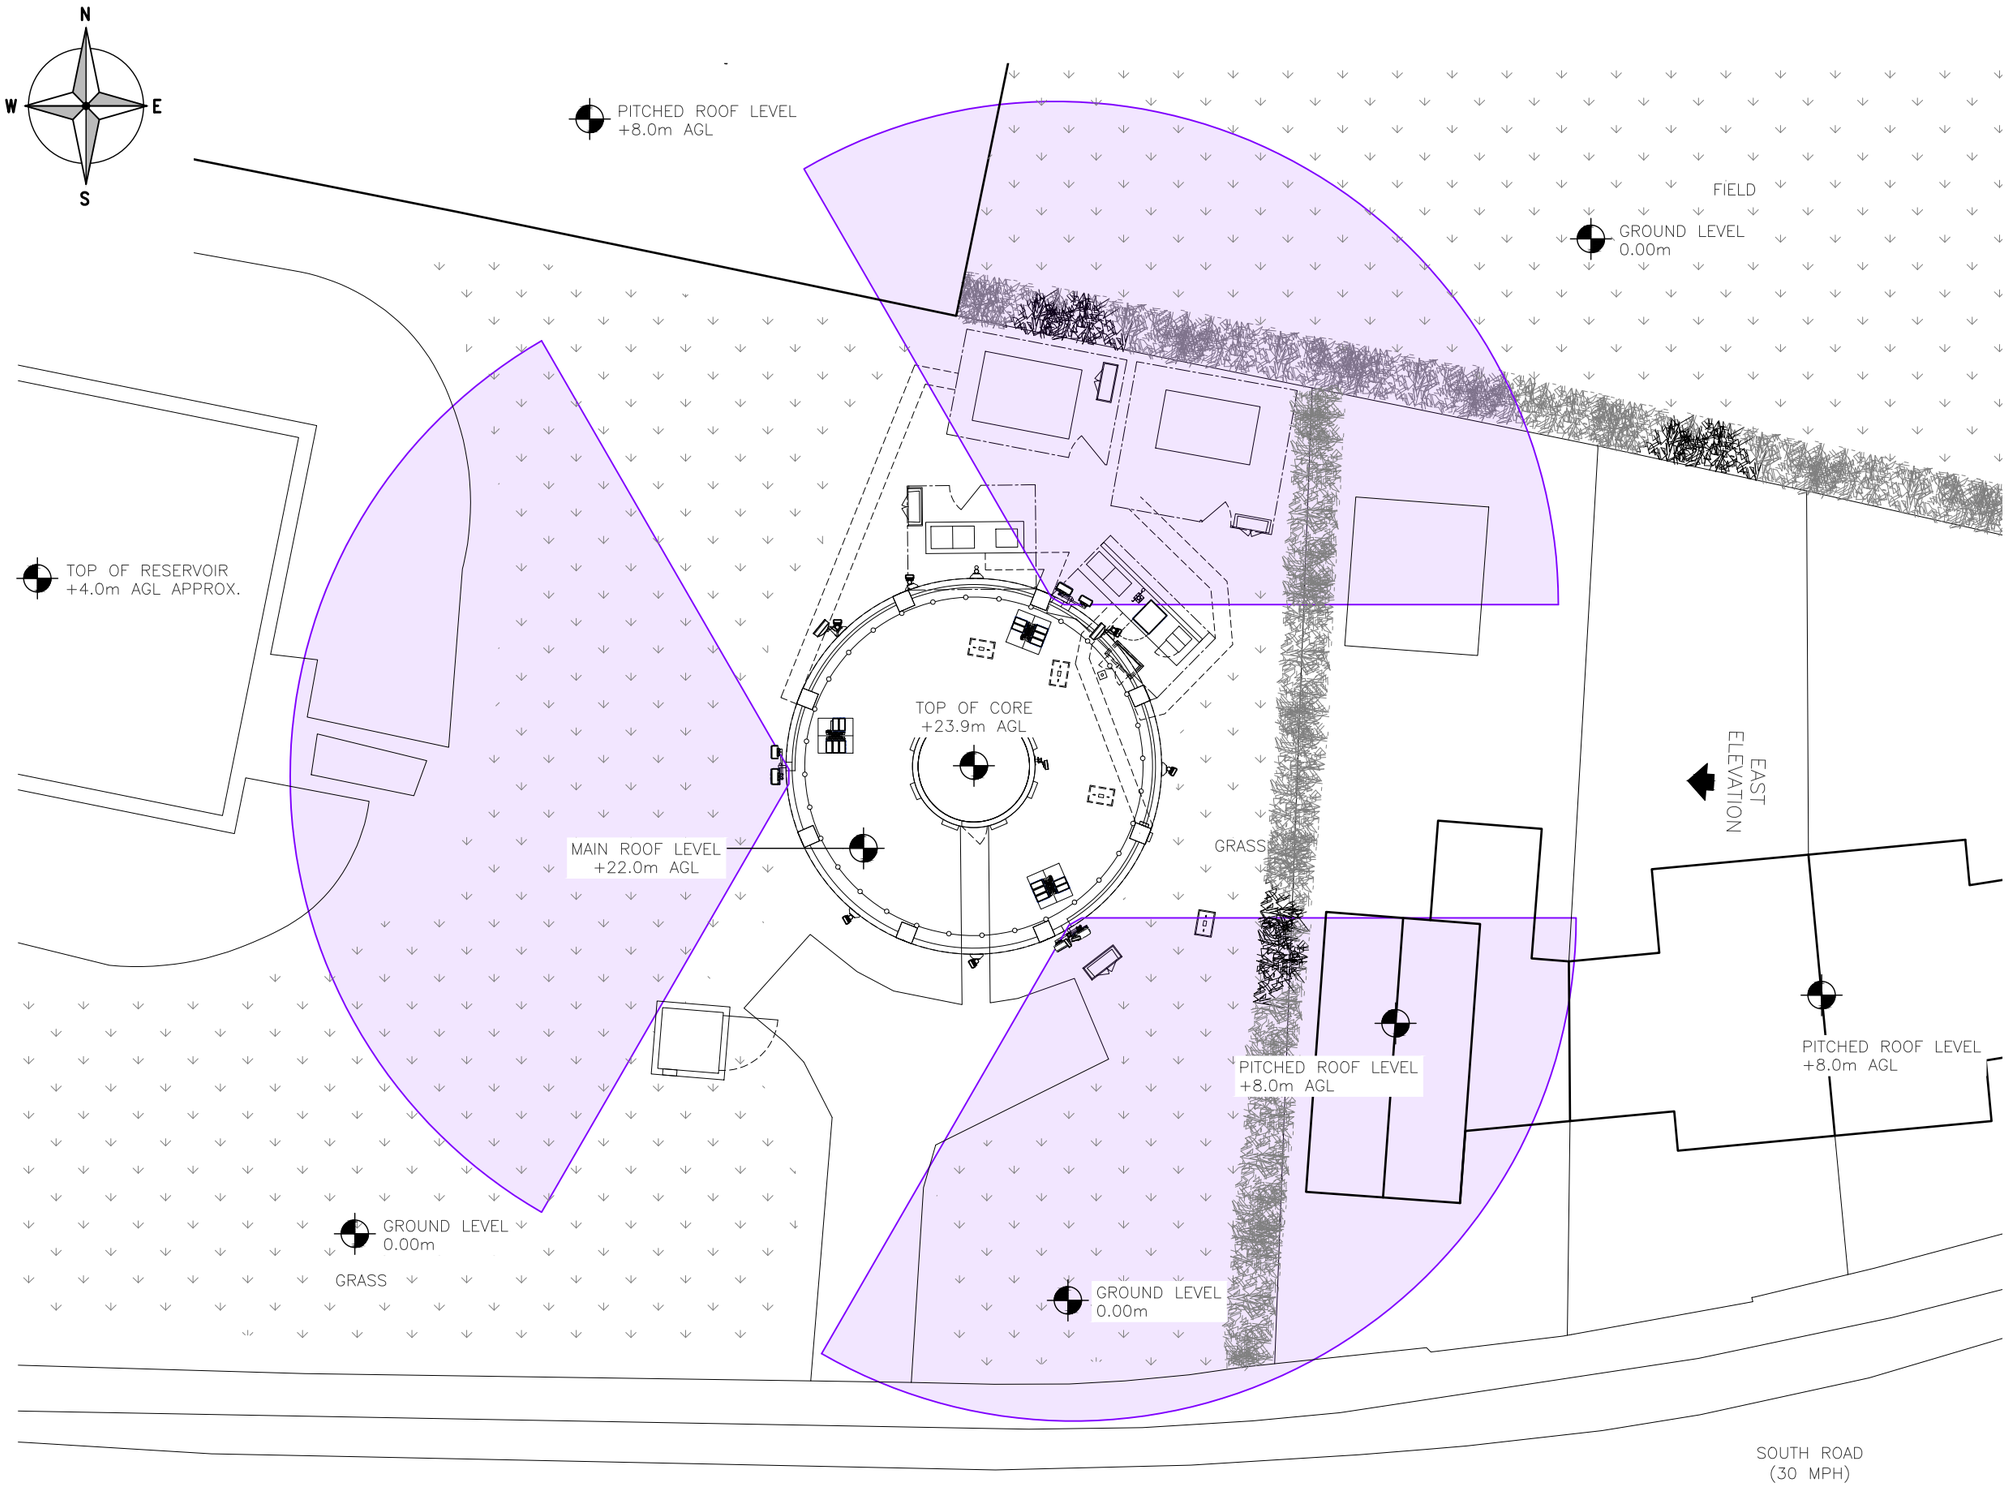

OCCUPATIONAL EXCLUSION ZONE PLAN

(1:200)

0 2 4 6 8 10m

1:200

These drawings comply with TEF Standard ICNIRP guidelines,
Designed in accordance with Cornerstone documents: SDN0006 v2.0

Notes
MITIGATION NOTES/ ACCEPTANCE CORRESPONDANCE

ALL DIMENSIONS ARE IN mm UNLESS NOTED OTHERWISE

N.G.R	E: 641826	N: 289433

ICNIRP ZONE INFORMATION


DOCUMENT REF.	SDN0006 (TEF)	v2.0
ICNIRP DOCUMENT SECTION	8.15	

ICNIRP CONFIG:
OLO
15–VM–V4.8–GR–BM–F–0

SECTOR(S)	ALL	ANGLE(∠)	18°

OCCUPATIONAL ICNIRP ZONE

OCCUPATIONAL EXCL. ZONE (A)	16.50m
OCCUPATIONAL BUILD HGT. (B)	4.03m

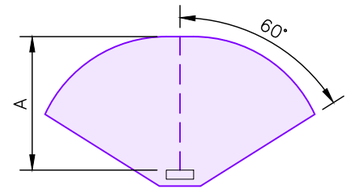

REV	MODIFICATION	BY	CH	DATE
A	PLANNING ISSUE	BP	DCC	14.11.25

circet UK
Unit 27F-G, Hartlebury Trading Estate, Crown Lane, Hartlebury, Worcestershire, DY10 4JD

cornerstone

Cell Name	Opt.
SOUTH WATER TOWER	–

Cell ID No

CSID	– VF	– TEF
11482824	–	036507
Project No.	– TM Cell ID	– N/A
–	–	–

Site Address / Contact Details


WATER TOWER
SOUTH ROAD
BECCLES
NORFOLK
NR34 9NZ

Drawing Title:
OCCUPATIONAL ICNIRP PLAN

Purpose of issue:	Dwg Rev:
PLANNING	A

Drawing Number:	Pack Issue:
450	A

Surveyed By:	Original Sheet Size:		
CIRCET	A3		
Drawn: BP	Date: 14.11.25	Checked: DCC	Date: 14.11.25

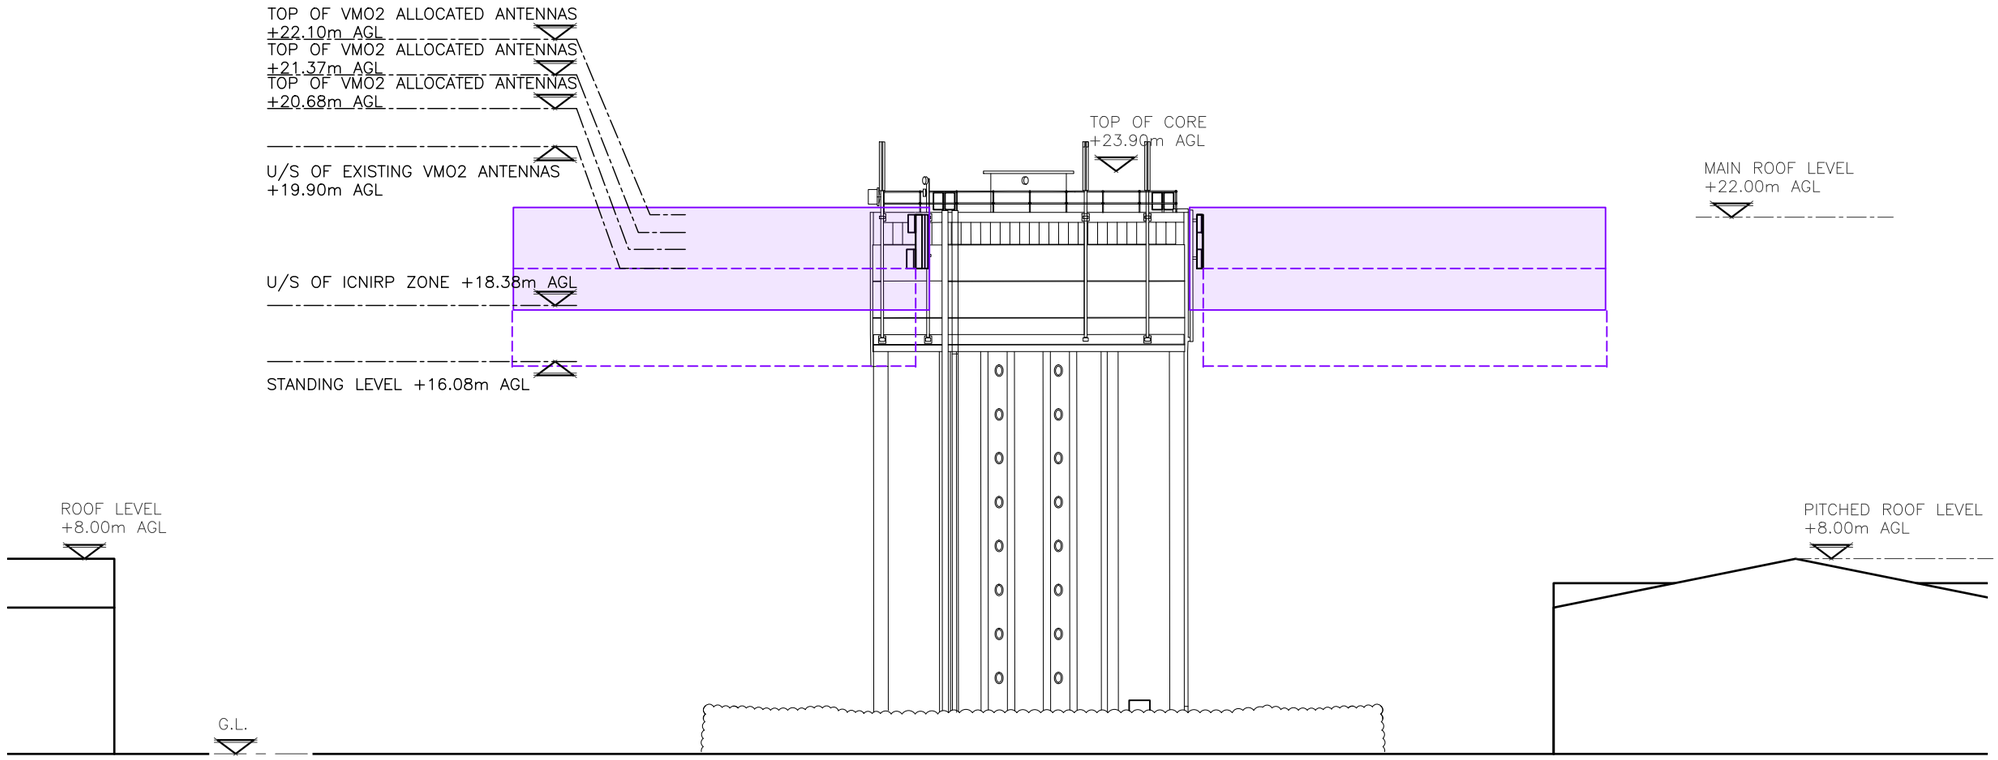

OCCUPATIONAL EXCLUSION ZONE EAST ELEVATION

(1:250)

0 2.5 5 7.5 10 12.5m

1:250

These drawings comply with TEF Standard ICNIRP guidelines,
Designed in accordance with Cornerstone documents: SDN0006 v2.0

Notes
MITIGATION NOTES/ ACCEPTANCE CORRESPONDANCE

ALL DIMENSIONS ARE IN mm UNLESS NOTED OTHERWISE


N.G.R	E: 641826	N: 289433

ICNIRP ZONE INFORMATION

DOCUMENT REF.	SDN0006 (TEF)	v2.0
ICNIRP DOCUMENT SECTION	8.15	
ICNIRP CONFIG:		
OLO		
15–VM–V4.8–GR–BM–F–0		
SECTOR(S) ALL	ANGLE(∠)	18°

OCCUPATIONAL ICNIRP ZONE

OCCUPATIONAL EXCL. ZONE (A)	16.50m
OCCUPATIONAL BUILD HGT. (B)	4.03m

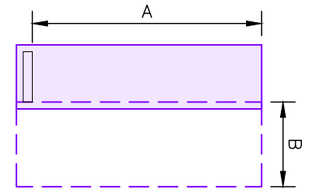

REV	MODIFICATION	BY	CH	DATE
A	PLANNING ISSUE	BP	DCC	14.11.25

circet UK
Unit 27F-G, Hartlebury Trading Estate, Crown Lane, Hartlebury, Worcestershire, DY10 4JD

cornerstone

Cell Name	Opt.
SOUTH WATER TOWER	–

Cell ID No

CSID	– VF	– TEF
11482824	–	036507
Project No.	– TM Cell ID	– N/A
–	–	–

Site Address / Contact Details

WATER TOWER
SOUTH ROAD
BECCLES
NORFOLK
NR34 9NZ

Drawing Title:
OCCUPATIONAL ICNIRP ELEVATION


Purpose of issue:	Dwg Rev:
PLANNING	
Drawing Number: 451	A

Surveyed By:	Original Sheet Size:	Pack Issue:
CIRCET	A3	

Drawn:	Date:	Checked:	Date:	
BP	14.11.25	DCC	14.11.25	A

N
W E
S

FOR INTERNAL USE ONLY
DO NOT ISSUE EXTERNALLY UNDER ANY CIRCUMSTANCES

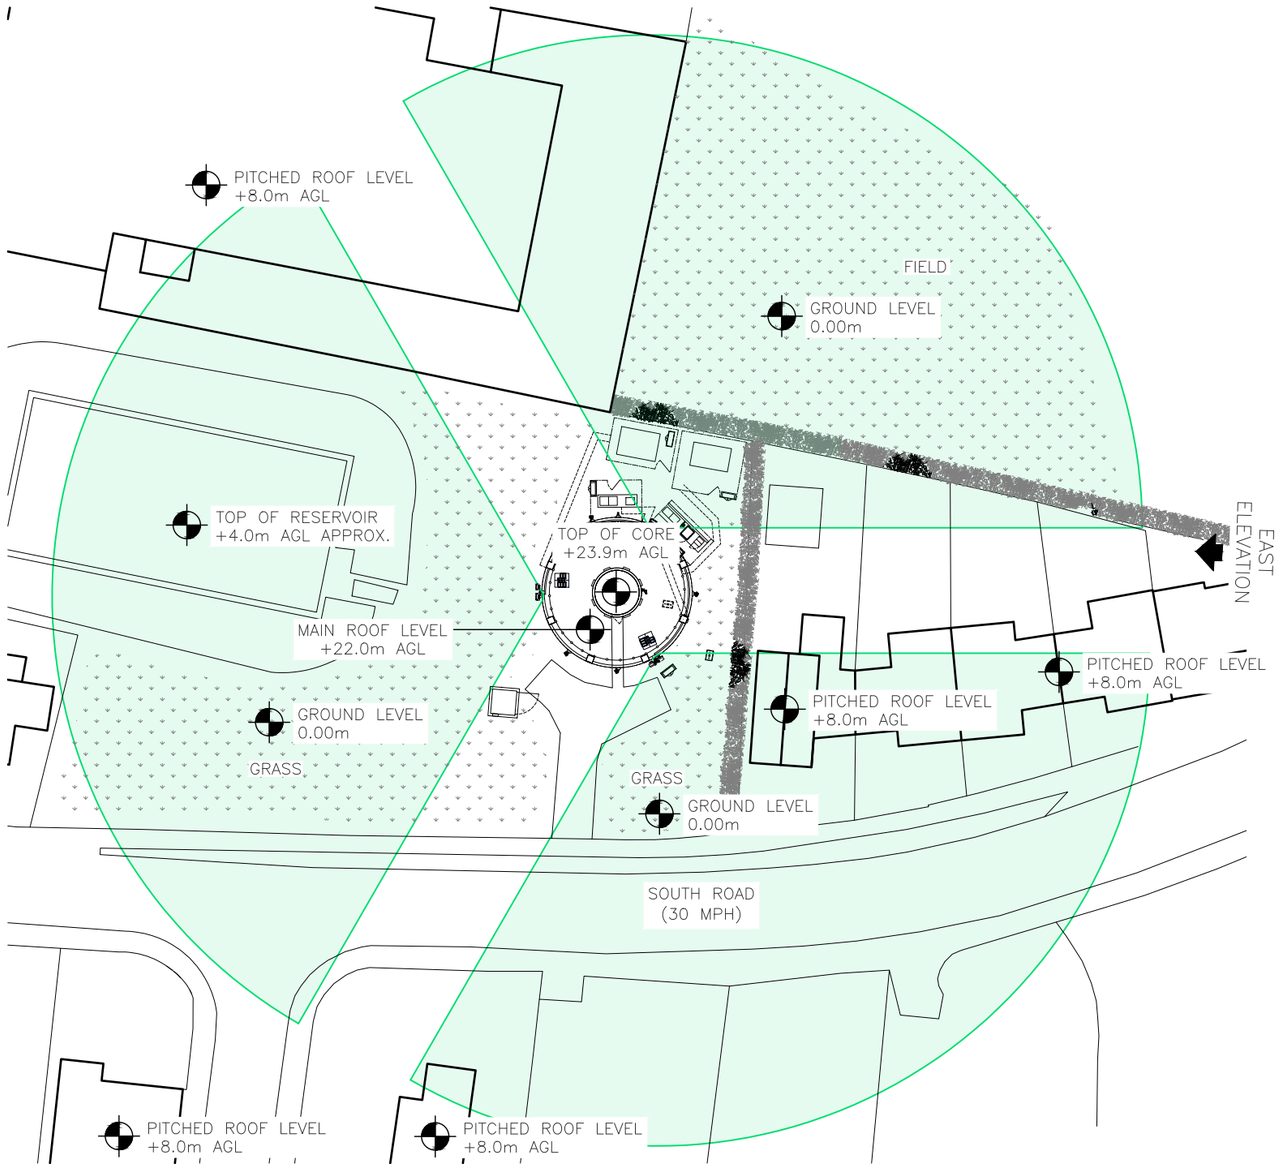

PUBLIC EXCLUSION ZONE PLAN
(1:500)

0 5 10 15 20 25m
1:500

These drawings comply with TEF Standard ICNIRP guidelines,
Designed in accordance with Cornerstone documents: SDN0006 v2.0


Notes
MITIGATION NOTES/ ACCEPTANCE CORRESPONDANCE

ALL DIMENSIONS ARE IN mm UNLESS NOTED OTHERWISE

N.G.R	E: 641826	N: 289433

ICNIRP ZONE INFORMATION

DOCUMENT REF.	SDN0006 (TEF)	v2.0
ICNIRP DOCUMENT SECTION	8.15	
ICNIRP CONFIG:		
OLO		
15–VM–V4.8–GR–BM–F–0		
SECTOR(S) ALL	ANGLE(∠)	18°
PUBLIC ICNIRP ZONE		
PUBLIC EXCL. ZONE (C)		40.40m
PUBLIC BUILD HGT. (D)		11.13m

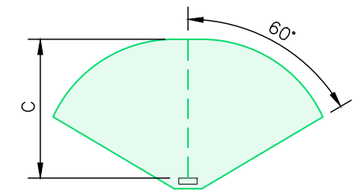

REV	MODIFICATION	BY	CH	DATE
A	PLANNING ISSUE	BP	DCC	14.11.25

circet UK
Unit 27F-G, Hartlebury Trading Estate, Crown Lane, Hartlebury, Worcestershire, DY10 4JD

cornerstone

Cell Name	Opt.
SOUTH WATER TOWER	–

Cell ID No

CSID	– VF	– TEF
11482824	–	036507
Project No.	– TM Cell ID	– N/A
–	–	–

Site Address / Contact Details

WATER TOWER
SOUTH ROAD
BECCLES
NORFOLK
NR34 9NZ


Drawing Title:
PUBLIC ICNIRP PLAN

Purpose of issue:	Dwg Rev:
PLANNING	A
Drawing Number: 452	

Surveyed By:	Original Sheet Size:	Pack Issue:
CIRCET	A3	A

Drawn:	Date:	Checked:	Date:
BP	14.11.25	DCC	14.11.25

FOR INTERNAL USE ONLY
DO NOT ISSUE EXTERNALLY UNDER ANY CIRCUMSTANCES

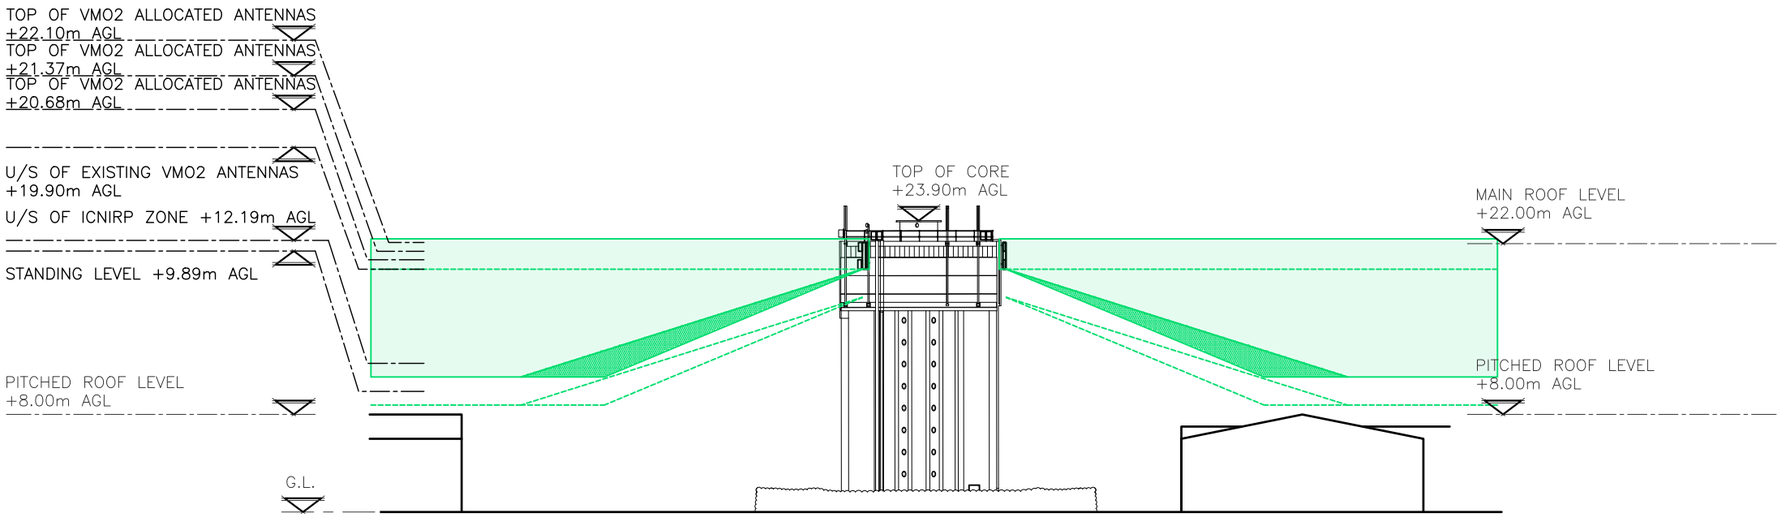

PUBLIC EXCLUSION ZONE EAST ELEVATION

(1:500)

0 5 10 15 20 25m
1:500

These drawings comply with TEF Standard ICNIRP guidelines,
Designed in accordance with Cornerstone documents: SDN0006 v2.0

Notes
MITIGATION NOTES/ ACCEPTANCE CORRESPONDANCE

ALL DIMENSIONS ARE IN mm UNLESS NOTED OTHERWISE


N.G.R	E: 641826	N: 289433

ICNIRP ZONE INFORMATION

DOCUMENT REF.	SDN0006 (TEF)	v2.0
ICNIRP DOCUMENT SECTION	8.15	
ICNIRP CONFIG:		
OLO		
15–VM–V4.8–GR–BM–F–0		
SECTOR(S)	ALL	ANGLE(∠) 18°

PUBLIC ICNIRP ZONE

PUBLIC EXCL. ZONE (C)	40.40m
PUBLIC BUILD HGT. (D)	11.13m

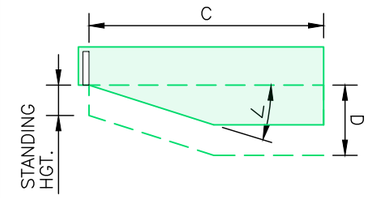

REV	MODIFICATION	BY	CH	DATE
A	PLANNING ISSUE	BP	DCC	14.11.25

circet UK
Unit 27F-G, Hartlebury Trading Estate, Crown Lane, Hartlebury, Worcestershire, DY10 4JD

cornerstone

Cell Name	Opt.
SOUTH WATER TOWER	–

Cell ID No

CSID	– VF	– TEF
11482824	–	036507
Project No.	– TM Cell ID	– N/A
–	–	–

Site Address / Contact Details

WATER TOWER
SOUTH ROAD
BECCLES
NORFOLK
NR34 9NZ

Drawing Title: PUBLIC ICNIRP ELEVATION

Purpose of issue: PLANNING — Dwg Rev: A

Drawing Number: 453

Surveyed By:	Original Sheet Size:	Pack Issue:
CIRCET	A3	

Drawn:	Date:	Checked:	Date:	
BP	14.11.25	DCC	14.11.25	A

EXISTING ANTENNA SCHEDULE

R.F. CONFIG CODE:	SECTOR 1 BEARING (DEG)						SECTOR 2 BEARING (DEG)						SECTOR 3 BEARING (DEG)						SECTOR 4 BEARING (DEG)					
NSHS2Fv01 (A)	EA1	30°	EB1	30°	–	–	EA2	150°	EB2	150°	–	–	EA3	270°	EB3	270°	–	–	–	–	–	–	–	–

ANTENNA DETAILS	SECTOR (SELECT ALL THAT APPLY)	SECTOR 1/2/3		
	ANTENNA REFERENCE	EA	EB	–
	ANTENNA CENTER (m)	20.85	20.95	–
	STATUS	REMOVE	REMOVE	–

EXISTING ANTENNA SCHEMATIC

LEGACY DUMMY ANTENNA

ANTENNA
SUA-7

COMBINER

RRH

RRH

RRH

RRU ABOVE THIS LINE REMOTE

RRU BELOW THIS LINE LOCAL

COMBINER

X07

ALL DIMENSIONS ARE IN mm UNLESS NOTED OTHERWISE

N.G.R E: 641826 N: 289433

NOTES:

EQUIPMENT COLOUR KEY

EXISTING EQUIPMENT	
TEF EQUIPMENT ALLOCATED	
TEF PROPOSED EQUIPMENT	
NEUTRAL FOOTPRINT	

REV	MODIFICATION	BY	CH	DATE
A	PLANNING ISSUE	BP	DCC	14.11.25

circet UK
Unit 27F-G, Hartlebury Trading Estate, Crown Lane, Hartlebury, Worcestershire, DY10 4JD

cornerstone

Cell Name	Opt.
SOUTH WATER TOWER	–

Cell ID No

CSID	– VF	– TEF
11482824	–	036507
Project No.	– TM Cell ID	– N/A
–	–	–

Site Address / Contact Details

WATER TOWER
SOUTH ROAD
BECCLES
NORFOLK
NR34 9NZ

Drawing Title: EXISTING TEF R.F. SYSTEM

Purpose of issue:	Dwg Rev:
PLANNING	A
Drawing Number: 500	

Surveyed By:	Original Sheet Size:	Pack Issue:
CIRCET	A3	A

Drawn:	Date:	Checked:	Date:
BP	14.11.25	DCC	14.11.25

ALLOCATED SCHEMATIC – DOC REF: UKDBS_BAU_0705_ALL REGIONS V4.0

AFF3

AFF6

AFF1

RFF1n

RFF1n

RFF1n

RFF1n

RFF2n

RRU ABOVE THIS LINE REMOTE

RRU BELOW THIS LINE LOCAL

DESIGN CODES

The Actual Code reflects the positions in which each operator has reserved the right to install equipment as shown in the Allocated schematic

ACTUAL: 03H(5+0)v4

Allocated = Operator acquired rights, Position reserved for future equipment

ALL DIMENSIONS ARE IN mm UNLESS NOTED OTHERWISE

N.G.R E: 641826 N: 289433

NOTES:

EQUIPMENT COLOUR KEY

EXISTING EQUIPMENT	
VF ALLOCATED EQUIPMENT	
VF PROPOSED EQUIPMENT	
TEF ALLOCATED EQUIPMENT	
TEF PROPOSED EQUIPMENT	
SHARED EQUIPMENT	
NEUTRAL FOOTPRINT (ACCESS)	

REV	MODIFICATION	BY	CH	DATE
A	PLANNING ISSUE	BP	DCC	14.11.25

circet UK

Unit 27F-G, Hartlebury Trading Estate, Crown Lane, Hartlebury, Worcestershire, DY10 4JD

cornerstone

Cell Name	Opt.
SOUTH WATER TOWER	–

Cell ID No

CSID	– VF	– TEF
11482824	–	036507
Project No.	– TM Cell ID	– N/A
–	–	–

Site Address / Contact Details

WATER TOWER
SOUTH ROAD
BECCLES
NORFOLK
NR34 9NZ

Drawing Title:
ALLOCATED TEF R.F. SYSTEM SCHEMATIC

Purpose of issue:	Dwg Rev:
PLANNING	A
Drawing Number: 550	

Surveyed By:	Original Sheet Size:	Pack Issue:
CIRCET	A3	

Drawn:	Date:	Checked:	Date:	
BP	14.11.25	DCC	14.11.25	A

ALLOCATED SCHEDULE – DOC REF: UKDBS_BAU_0705_ALL REGIONS Version ?

R.F. CONFIG CODE:	SECTOR 1 BEARING (DEG)						SECTOR 2 BEARING (DEG)						SECTOR 3 BEARING (DEG)						SECTOR 4 BEARING (DEG)					
–	A1	30°	B1	30°	C1	30°	A2	150°	B2	150°	C2	150°	A3	270°	B3	270°	C3	270°						

ANTENNA DETAILS	SECTOR (SELECT ALL THAT APPLY)	SECTOR 1/2/3		
	ANTENNA REFERENCE	A	B	C
	ANTENNA CENTER (m)	21.0	21.74	20.29
	STATUS	ALLOCATED	ALLOCATED	ALLOCATED

STATUS KEY		
	ALLOCATED	RESERVED/ ASSIGNED LOCATION FOR FUTURE EQUIPMENT
	PROPOSED	NEW
	REMAIN	EXISTING TO BE REUSED
	RELOCATE	EXISTING TO BE RE-PURPOSED, REDIRECTED ECT..
	REMOVE	EXISTING TO BE REMOVED

ALL DIMENSIONS ARE IN mm UNLESS NOTED OTHERWISE

N.G.R E: 641826 N: 289433

NOTES:

REV	MODIFICATION	BY	CH	DATE
A	PLANNING ISSUE	BP	DCC	14.11.25

circet UK
Unit 27F-G, Hartlebury Trading Estate, Crown Lane, Hartlebury, Worcestershire, DY10 4JD

cornerstone

Cell Name	Opt.
SOUTH WATER TOWER	–

Cell ID No

CSID	– VF	– TEF
11482824	–	036507
Project No.	– TM Cell ID	– N/A
–	–	–

Site Address / Contact Details

WATER TOWER
SOUTH ROAD
BECCLES
NORFOLK
NR34 9NZ

Drawing Title: ALLOCATED TEF ANTENNA SCHEDULE

Purpose of issue:	Dwg Rev:
PLANNING	A

Drawing Number:				Pack Issue:
551				A
Surveyed By: CIRCET		Original Sheet Size: A3		
Drawn: BP	Date: 14.11.25	Checked: DCC	Date: 14.11.25	

SUPPORT STRUCTURE SCHEDULE

EXISTING/ PROPOSED	OWNER	MANUFACTURER	MODEL	STRUCTURE HEIGHT	FOUNDATION TYPE (ROOT/PAD/GRILLAGE)	FOUNDATION DIMENSIONS (WxDxH)	COLOUR/ FINISH	STATUS	COMMENTS
EXISTING	VMO2	–	YOKE BRACKETS	–	–	–	RAL7035	REMAIN	3No.
EXISTING	VMO2	–	600mm AIRESCALE ONE CLIP RRH RAILS	–	–	–	RAL7035	REMOVE	6No.
EXISTING	VMO2	–	AMRB – RRH CLIP	–	–	–	RAL7035	REMOVE	9No.
EXISTING	VMO2	–	FPKC RRH POLE BRACKETS	–	–	–	RAL7035	REMOVE	6No.
EXISTING	VMO2	–	FLATPACK RACK RRH BRACKET	–	–	–	–	REMOVE	3No.
EXISTING	VMO2	–	43091 FREESTANDER MEDIUM	–	–	–	GALV.	REMAIN	3No. (1000mm LONG CHS POLE)
ALLOCATED	VMO2	NOKIA	AMRC RAIL	–	–	–	GALV.	NEW	6No. REQUIRED FOR RRHs

ENCLOSURE SCHEDULE

EXISTING/ PROPOSED	OPERATOR	MANUFACTURER	MODEL	DIMENSIONS (WxDxH)	LOCATION	COLOUR/ FINISH	STATUS	COMMENTS
EXISTING	VMO2	TYRONE	METER CABINET	1000x450x1200	CONCRETE BASE	RAL7035	REMAIN	–
EXISTING	VMO2	NOKIA	FLATPACK RACK (A)	750x600x1980	CONCRETE BASE	RAL7035	REMAIN	–
EXISTING	VMO2	NOKIA	FLATPACK RACK (B)	750x600x1980	CONCRETE BASE	RAL7035	REMAIN	–
EXISTING	VMO2	ELTEK	PERCY PSU (OUTDOOR)	705x831x2068	CONCRETE BASE	RAL7035	REMOVE	–
EXISTING	VMO2	ALIFABS	TSC	600x620x1420	CONCRETE BASE	RAL7035	REMAIN	–
ALLOCATED	VMO2	–	EFF1	725x850x2100	CONCRETE BASE	RAL7035	NEW	–

AC POWER SUPPLY SCHEDULE

EXISTING/ PROPOSED	OPERATOR	LOCATION	SUPPLY TYPE (LL/DNO/LOCAL THIRD PARTY)	PHASE (SINGLE/THREE/TWO)	SOURCE OCPD RATING (A)	EARTHING SYSTEM TYPE (TN-C-S/TT)	2nd SUPPLY TO BUILDING (Y/N)	LPS (ADDITION/NEW)	COMMENTS
EXISTING	VMO2	METER CABINET	DNO	SINGLE	100A	TN-C-S (PME)	–	–	–

DC POWER SUPPLY UNIT SCHEDULE

EXISTING/ PROPOSED	OPERATOR	MANUFACTURER	MODEL	LOCATION	AC SUPPLY TO PSU BREAKER SIZE (AMPS)	RECTIFIER SIZE (kW)	RECTIFIER QUANTITY	UPGRADE REQUIRED (Y/N)	COMMENTS
EXISTING	VMO2	ELTEK	PERCY PSU	CONCRETE BASE	63A	3.0kW	6	–	TO BE REMOVED
ALLOCATED	VMO2	TBD	TBD	EFF1	–	–	–	–	–

TRANSMISSION SUPPLY SCHEDULE

EXISTING/ PROPOSED (ENCLOSURE)	OPERATOR		TRANSMISSION ENCLOSURE	TRANSMISSION SOLUTION (MICROWAVE ONLY/FIBRE ONLY/ MICROWAVE+FIBRE (WITH PROVIDER NAME))	U SPACE AVAILABLE	CURRENT TRANSMISSION EQUIPMENT LOCATION	PROPOSED TRANSMISSION EQUIPMENT LOCATION	COMMENTS
	HOST	SHARER						
EXISTING	VMO2	–	TSC	MICROWAVE ONLY	1U	X	–	–

ALLOCATED RF EQUIPMENT SCHEDULE

STATUS	OPERATOR	ALLOCATED POSITION REF	DESIGN REFERENCE	DIMENSIONS (WxDxH)	WEIGHT (kg)	LOCATION	HEIGHT (C/L)	QUANTITY
ALLOCATED	VMO2	A1,2,3	AFF3	500x230x2200	55	HEADFRAME	16.5	3
ALLOCATED	VMO2	B1,2,3	AFF6	410x190x730	40	HEADFRAME	17.23	3
ALLOCATED	VMO2	C1,2,3	AFF1	410x190x730	40	HEADFRAME	15.96	3
ALLOCATED	VMO2	–	RFF1o	400x190x700	38	HEADFRAME	15.95	12
ALLOCATED	VMO2	–	RFF2o	400x190x450	25	HEADFRAME	14.95	3

ANCILLARY RF EQUIPMENT
(COMBINER/BBU/MHA/FILTER/GPS)

STATUS	OPERATOR	MANUFACTURER	MODEL	LOCATION	HEIGHT (C/L)	QUANTITY	COMMENTS
EXISTING	VMO2	NOKIA	GPS MODULE	CABIN	3.25m	1	–

STATUS KEY		
	ALLOCATED	RESERVED/ ASSIGNED LOCATION FOR FUTURE EQUIPMENT
	PROPOSED	NEW
	REMAIN	EXISTING TO BE REUSED
	RELOCATE	EXISTING TO BE RE-PURPOSED, REDIRECTED ECT..
	REMOVE	EXISTING TO BE REMOVED

ALL DIMENSIONS ARE IN mm UNLESS NOTED OTHERWISE

N.G.R E: 641826 N: 289433

REFER TO THE SITE SPECIFIC DRAWING SUBMISSION CHECKLIST (SDN0020) FOR A COMPREHENSIVE LIST AND INSTRUCTION ON WHERE TO FIND ALL ACCOMPANYING DESIGN DOCUMENTATION.

DESIGN DEPENDENCIES		COMPLETED DATE
DRA	✓	14.11.2025
STRUCTURAL CACLS	✓	XX.XX.XXXX
IBD	✓	15.10.2025
PANs	✓	29.10.2025
ELECTRICAL CALCS	✓	XX.XX.XXXX

REV	MODIFICATION	BY	CH	DATE
A	PLANNING ISSUE	BP	DCC	14.11.25

circet UK
Unit 27F-G, Hartlebury Trading Estate, Crown Lane, Hartlebury, Worcestershire, DY10 4JD

cornerstone

Cell Name	Opt.
SOUTH WATER TOWER	–

Cell ID No

CSID	– VF	– TEF
11482824	–	036507
Project No.	– TM Cell ID	– N/A
–	–	–

Site Address / Contact Details

WATER TOWER
SOUTH ROAD
BECCLES
NORFOLK
NR34 9NZ

Drawing Title:
PROPOSED EQUIPMENT SCHEDULE

Purpose of issue:	Dwg Rev:
PLANNING	A

Drawing Number:			
570			A
Surveyed By: CIRCET		Original Sheet Size: A3	Pack Issue:
Drawn: BP	Date: 14.11.25	Checked: DCC	Date: 14.11.25