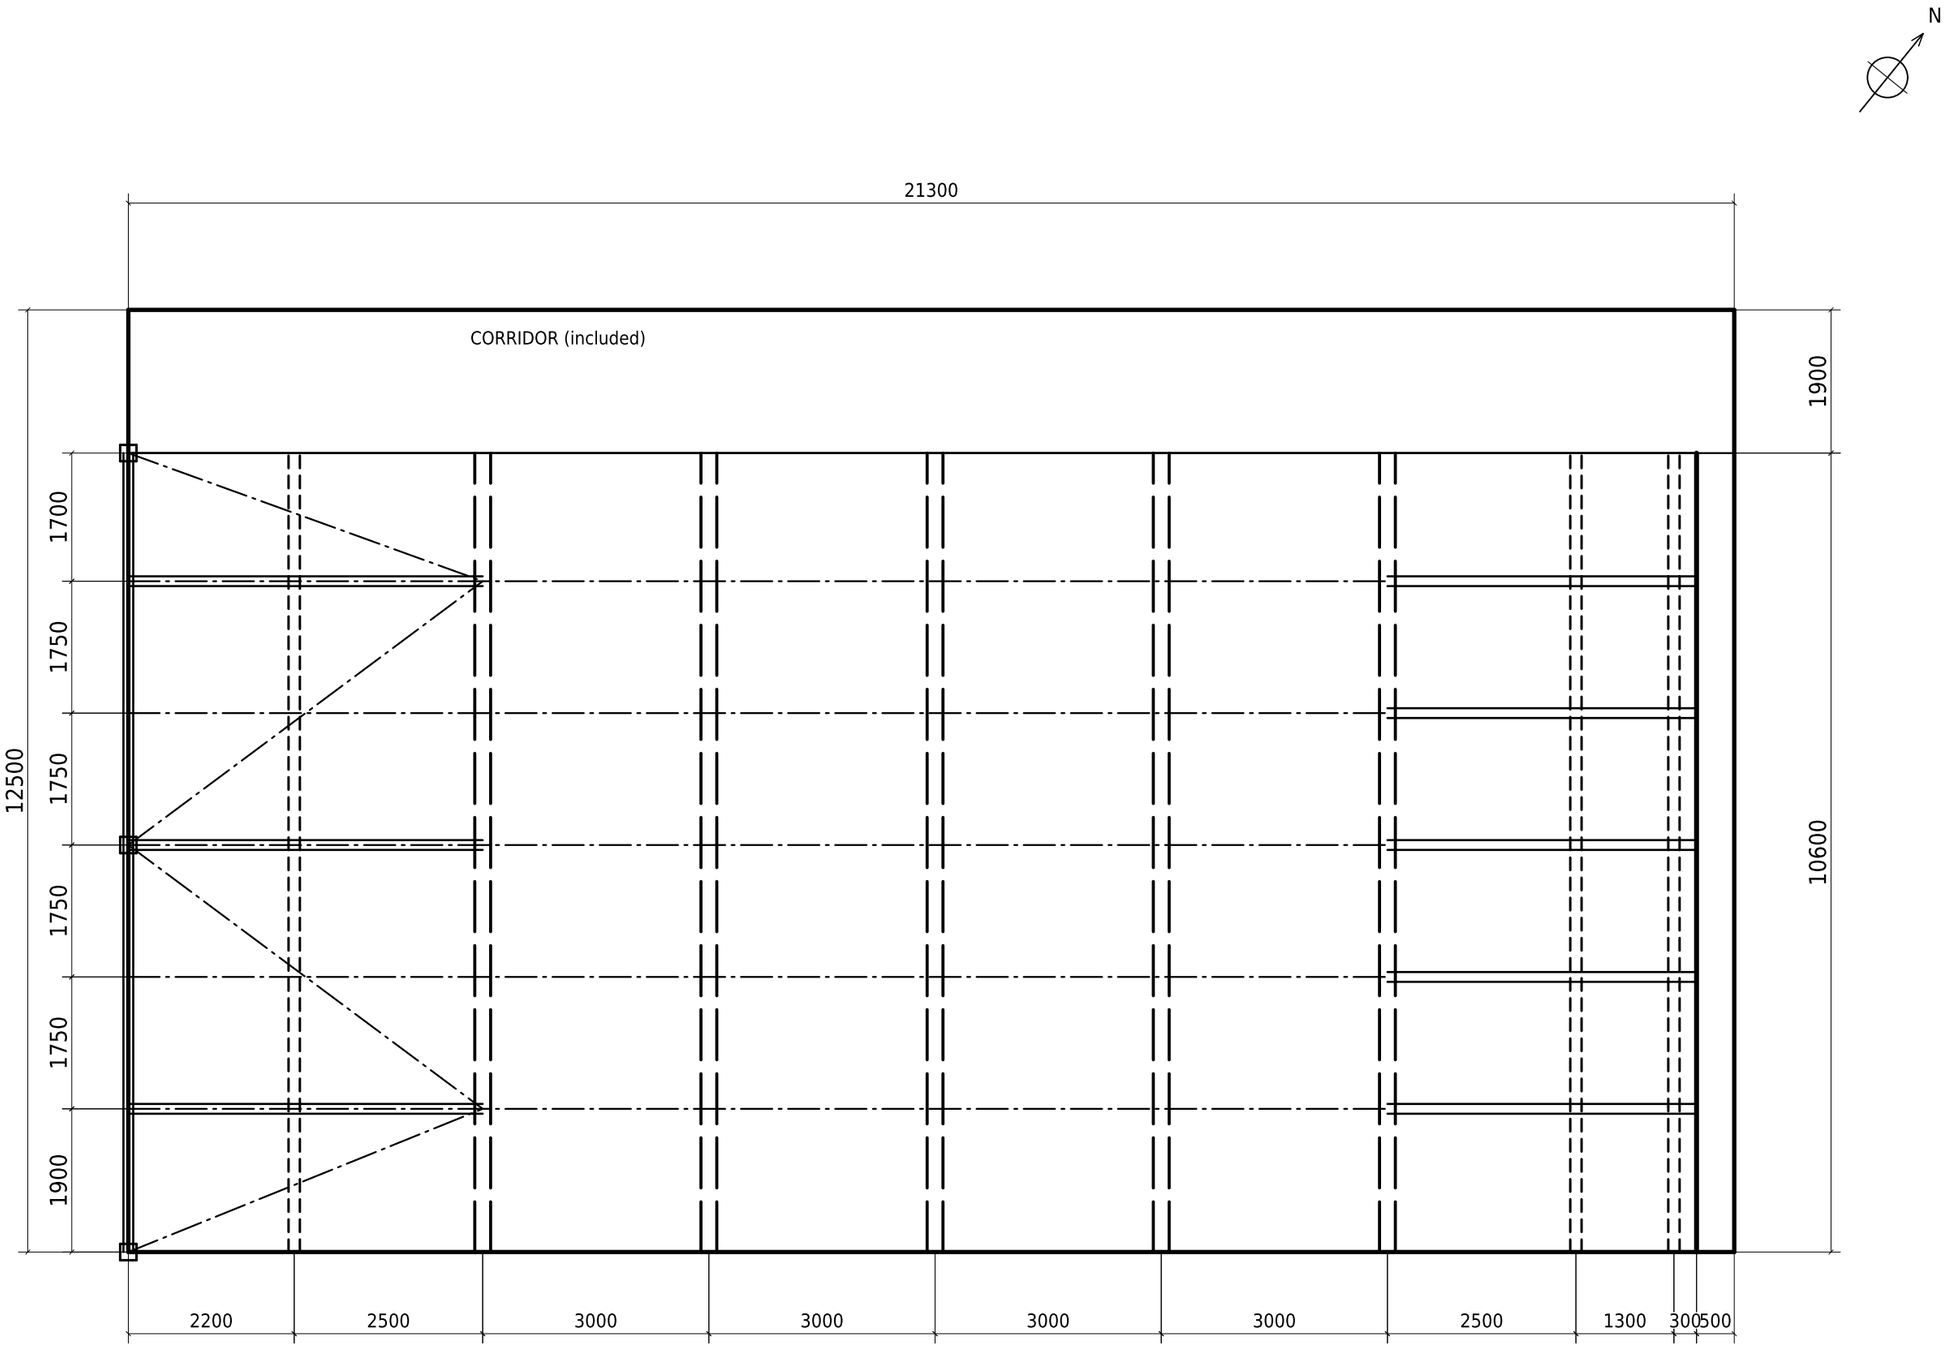


① Roof Support Layout

NTS

DIMENSIONS IN mm

DRAWING NOTES

1. Metal deck roof; existing PV arrays in three rows.
2. Nominal overall depth includes the corridor strip.
3. Castellated beams 800 deep; flange 210 wide x 18 thick.
4. Equipment set-out is shown on sheet 71222-02.
5. CHS: upper in left diagonal bay; lower in central bays. Right bay: I-beams only.

MEMBER KEY

- CB 800 deep; flange 210 x 18
- B1 I-beam 200 x 250
- B2 I-beam 200 x 150
- CHS 90 dia; levels per note 5
- FW Full-web end beam

Rev	Issue	Drawn	Chkd	Date
1	REVIEW	S.T.	K.S.	08-11-26

Consultant:

KA ENGINEERING GROUP

Client:

Jansen SL

Drawing Title:

Roof Support Layout

JET 0231

Gala Theatre & Cinema

Millennium Square, Durham

Drawn: S.T. Checked: K.S.

71222-01 | Rev 1 NTS