
DIMENSIONS IN mm; LEVELS ABOVE GROUND

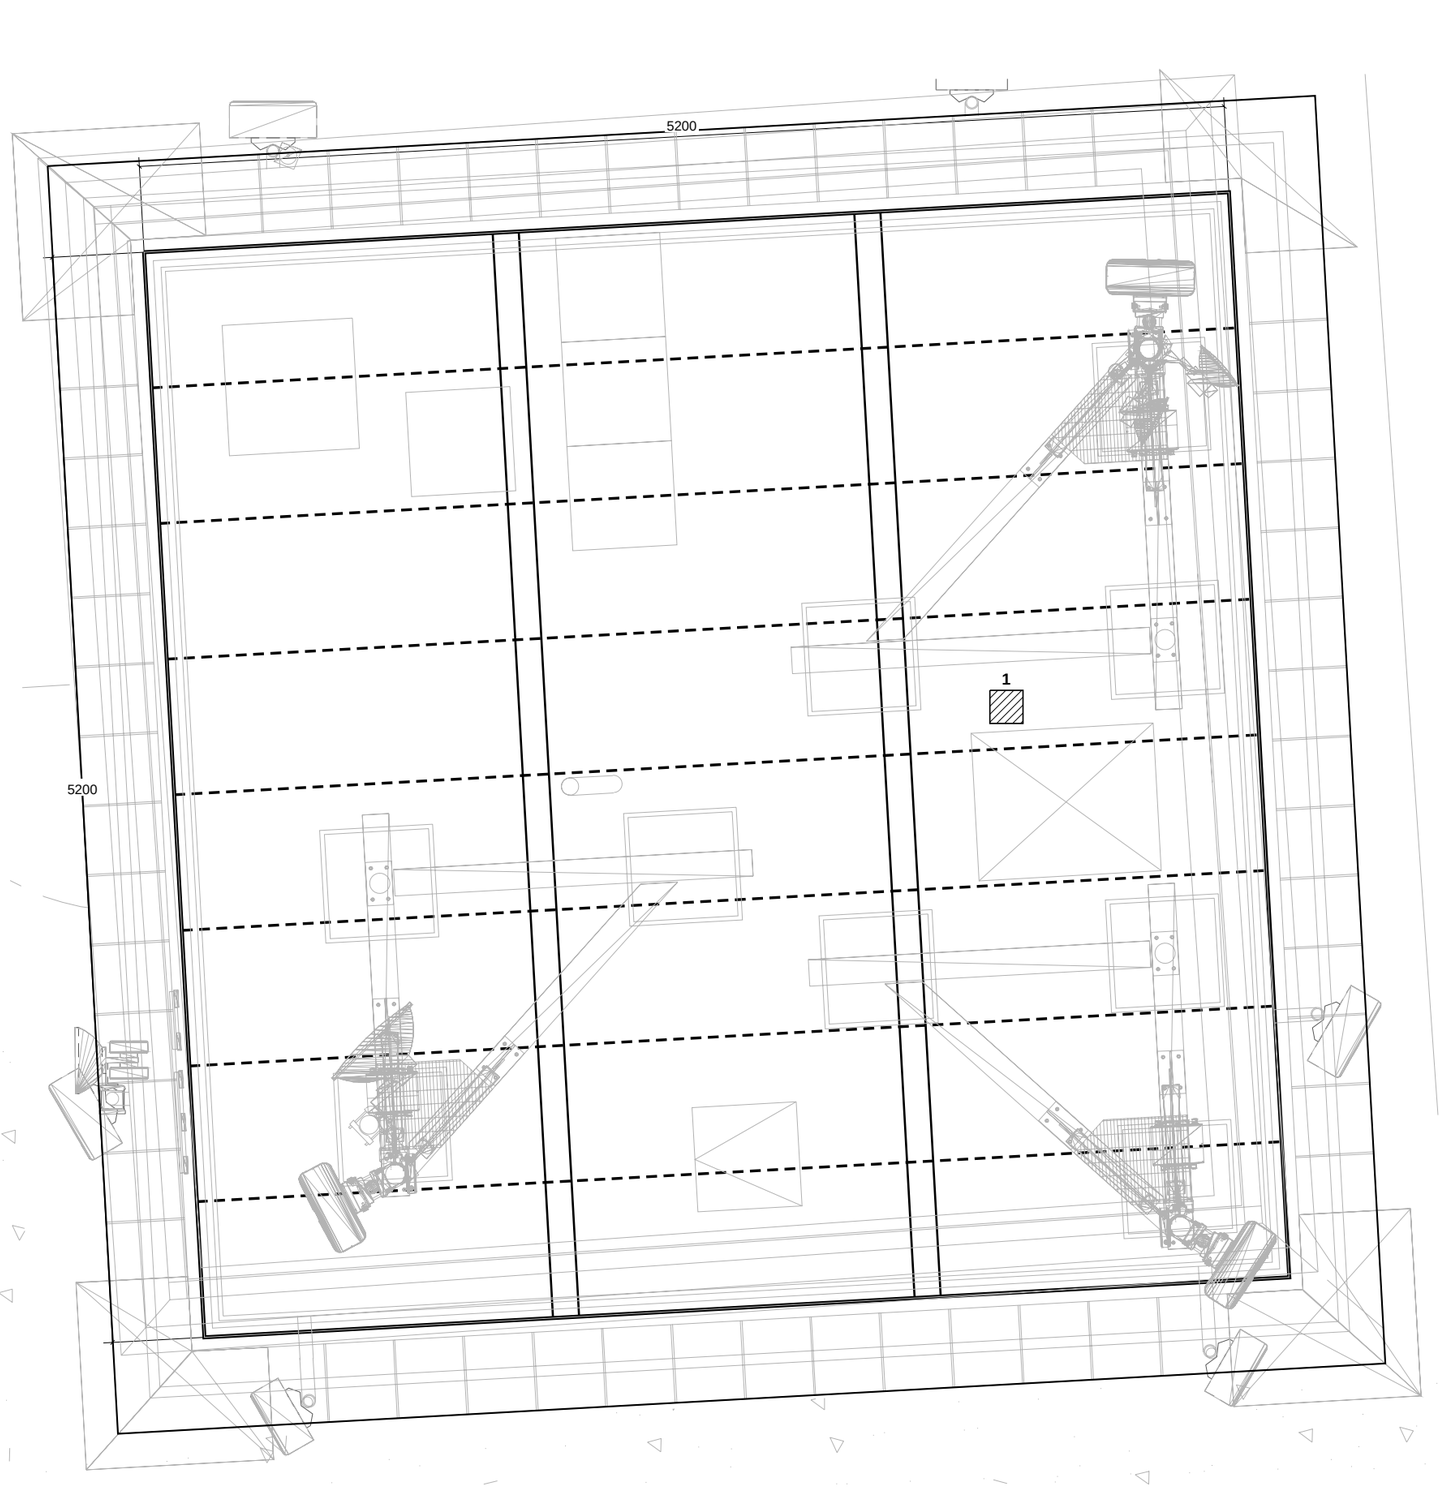


1 **Roof Support Layout / Scan Location**

NTS

## DRAWING NOTES

1. Roof over fourth floor: slab 175 thick; parapet 550 high.

2. Exposed roof members: measured 152 x 125; flange 9.

3. Scan 1: soffit of roof over fourth floor.

## ELEMENT KEY

- Masonry wall faces
- Embedded roof beams
- Exposed roof members
- Soffit scan - location 1

| Rev | Issue | Drawn | Chkd | Date |
|---|---|---|---|---|
| 1 | REVIEW | AT | AF | 04-11-26 |

Consultant:

KA ENGINEERING GROUP

Client: JetNSL

JET network solutions

Drawing Title:

**Roof Support Layout**

**SAFFRON WALDEN TOWER**

Mount Pleasant Road, Saffron Walden

Essex CB11 4GA

Drawn: AT Checked: AF

**7145-01 | Rev 1** NTS