
DIMENSIONS IN mm; LEVELS ABOVE GROUND

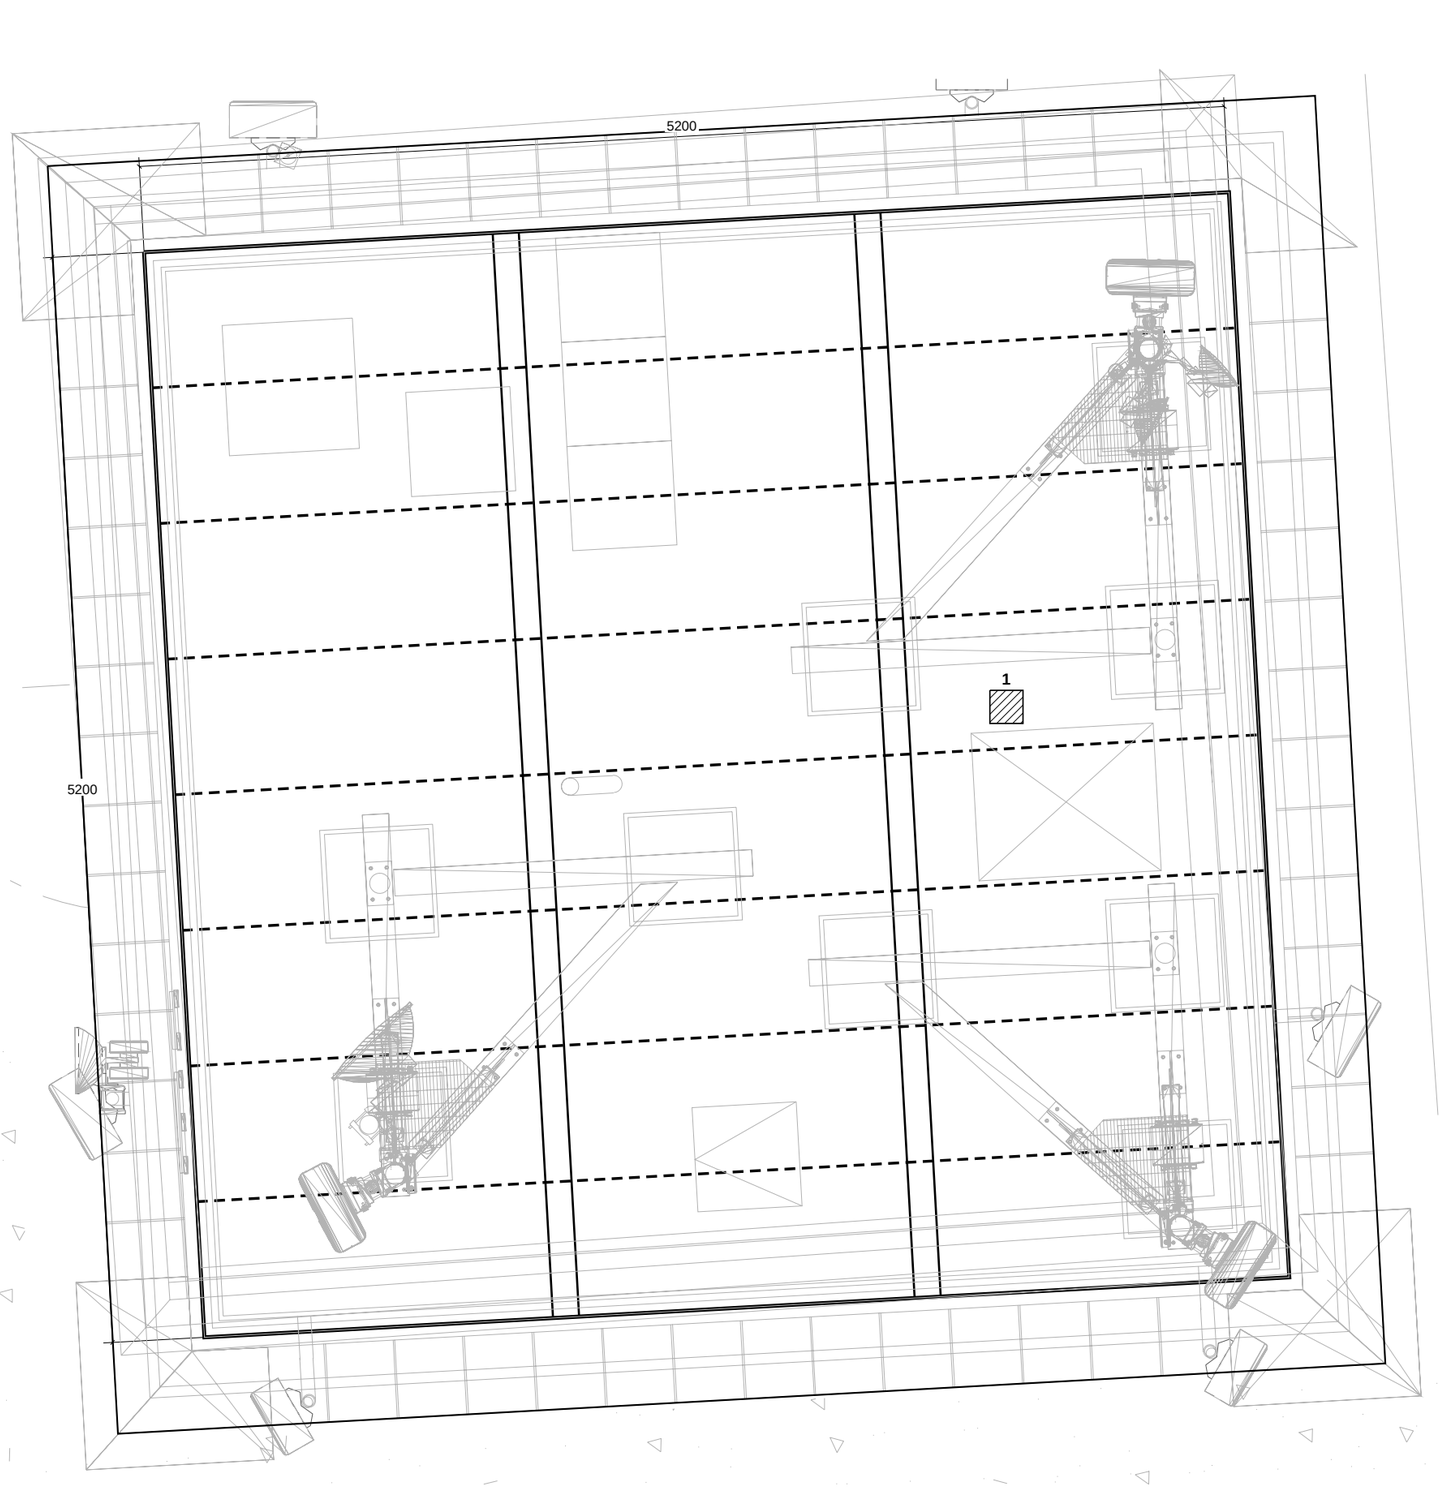

1 **Roof Support Layout / Scan Location**

NTS

DRAWING NOTES

1. Roof over fourth floor: slab 175 thick; parapet 550 high.

2. Exposed roof members: measured 152 x 125; flange 9.

3. Scan 1: soffit of roof over fourth floor.

ELEMENT KEY

- Masonry wall faces
- Embedded roof beams
- Exposed roof members
- Soffit scan - location 1

Rev	Issue	Drawn	Chkd	Date
1	REVIEW	AT	AF	04-11-26

Consultant:

KA ENGINEERING GROUP

Client: JetNSL

JET network solutions

Drawing Title:

Roof Support Layout

SAFFRON WALDEN TOWER

Mount Pleasant Road, Saffron Walden


Essex CB11 4GA

Drawn: AT Checked: AF

7145-01 | Rev 1 NTS


SECTIONAL ELEVATION

Clear heights and slab thicknesses

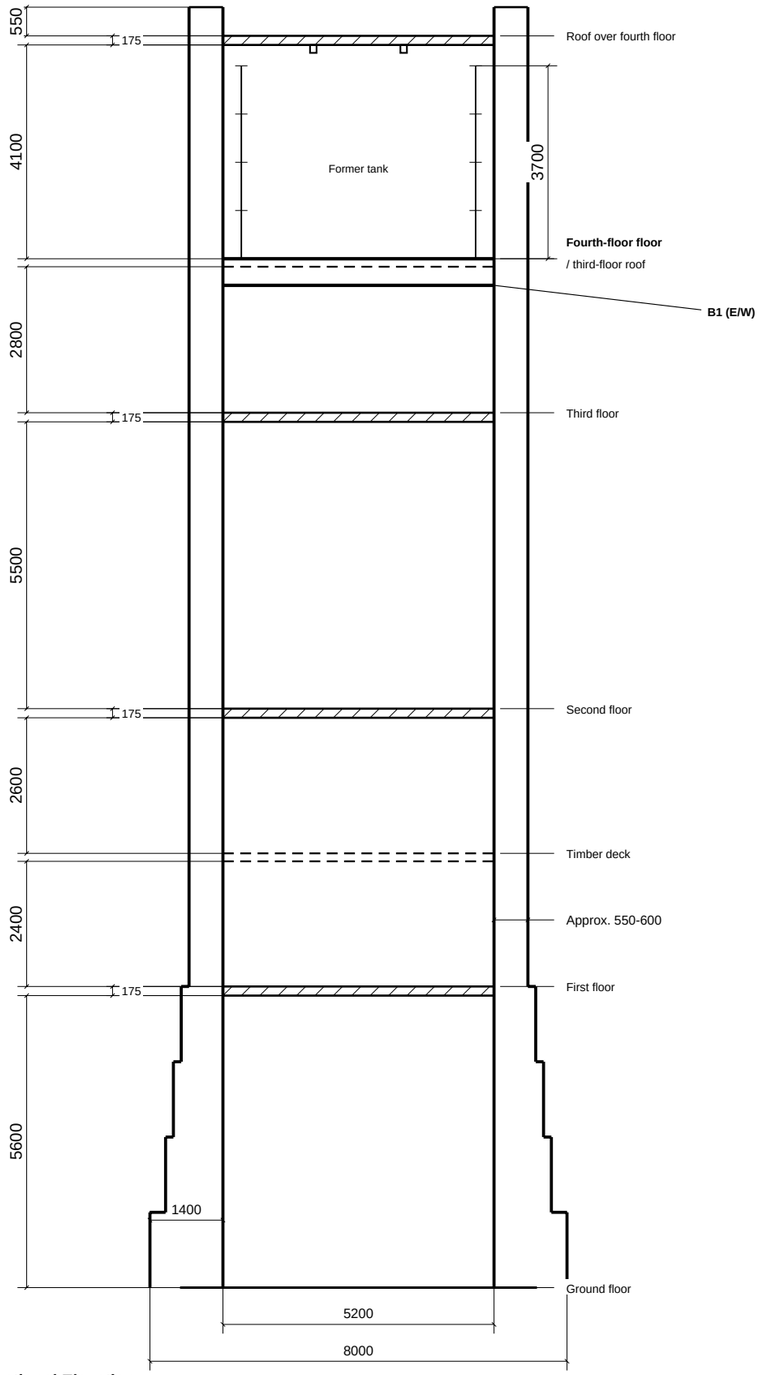


1 **Sectional Elevation**

NTS

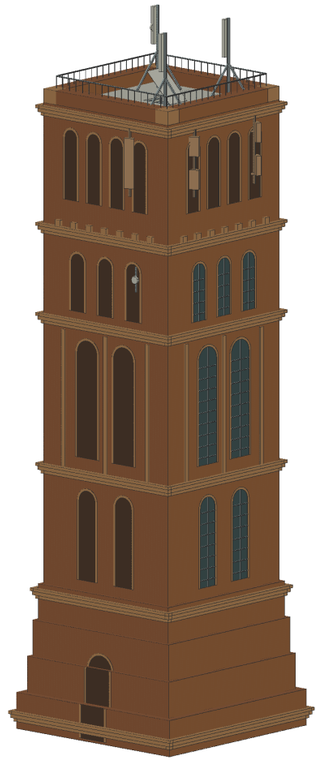

2 **Tower**

3D NTS

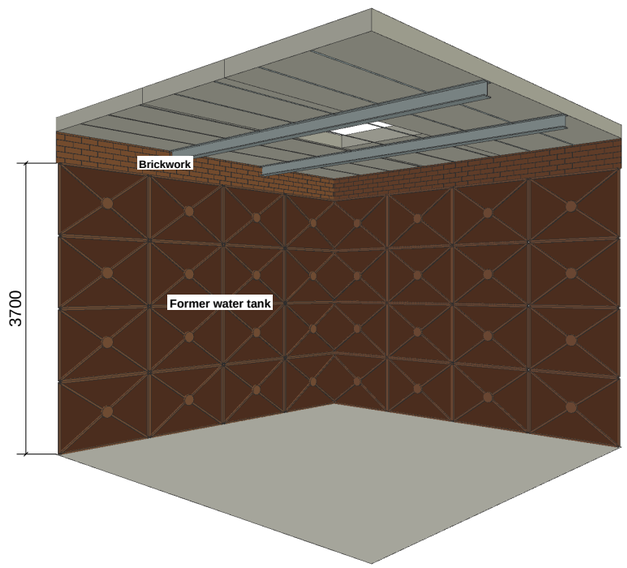

3 **Fourth-Floor Interior**

3D NTS

DIMENSIONS IN mm; LEVELS ABOVE GROUND

DRAWING NOTES

1. All height dimensions are floor to ceiling; concrete slabs 175 thick shown separately.
2. B1: 510 x 190, flange 20; at fourth-floor FLOOR / third-floor ROOF.
3. Fourth-floor steel floor and intermediate timber-deck build-ups not measured.
4. Ribbed panels are the former water tank.

ELEMENT KEY

Concrete slab

Steel floor

Intermediate timber deck

B1 Primary E/W beam at floor 4

Rev	Issue	Drawn	Chkd	Date
1	REVIEW	AT	AF	04-11-26

Consultant:

KA ENGINEERING GROUP

Client: JetNSL

JET network solutions

Drawing Title:

Elevation / 3D Views

SAFFRON WALDEN TOWER

Mount Pleasant Road, Saffron Walden

Essex CB11 4GA

Drawn: AT Checked: AF

7145-02 | Rev 1 NTS