
DIMENSIONS IN mm; LEVELS ABOVE GROUND

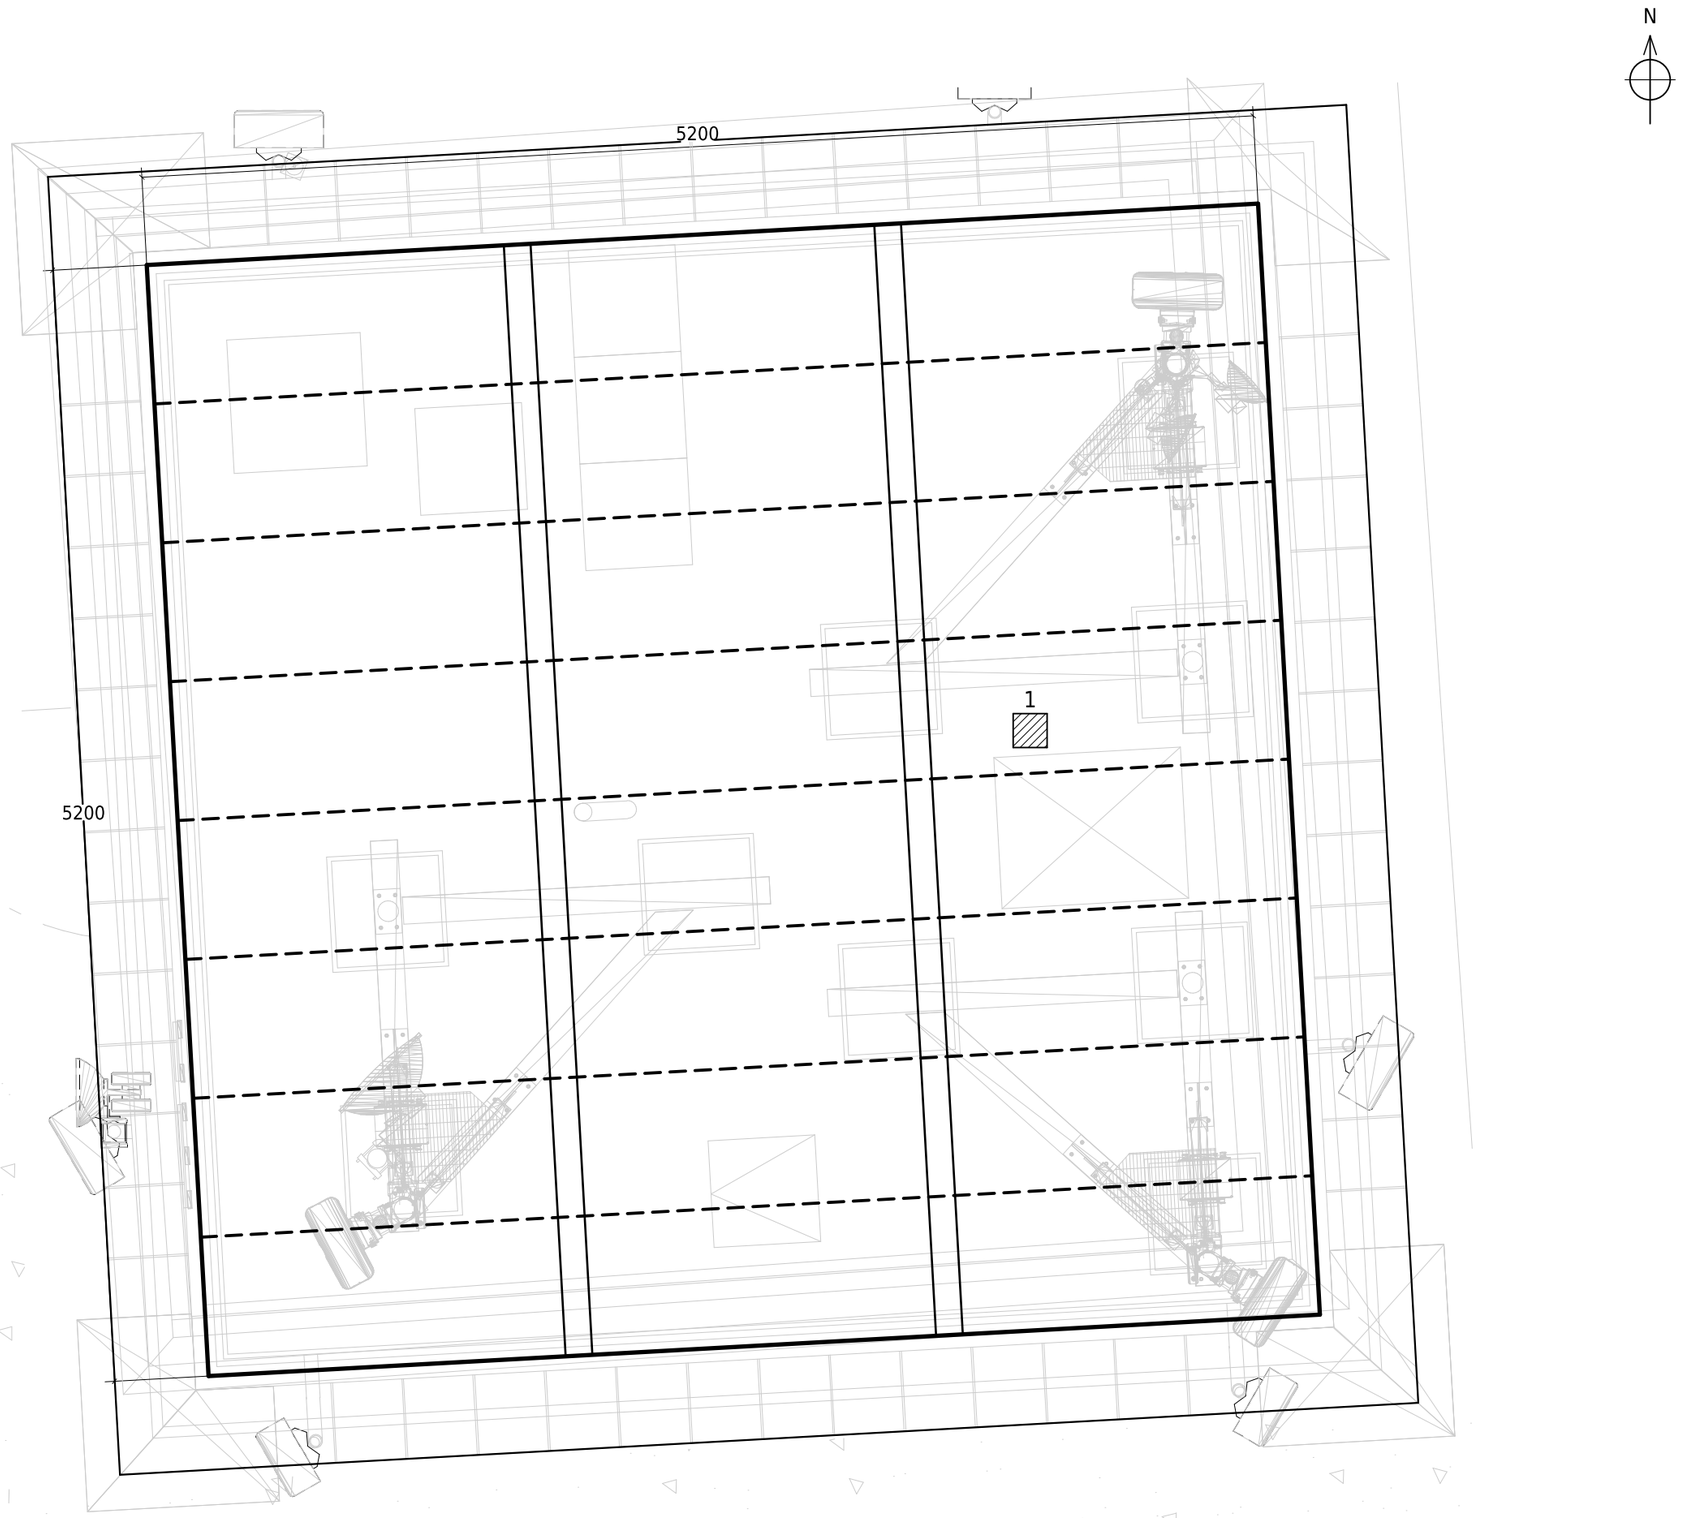

① Roof Support Layout / Scan Location

NTS

DRAWING NOTES

1. Roof over fourth floor: slab 175 thick; parapet 550 high.
2. Exposed roof members: measured 152 x 125; flange 9.
3. Scan 1: soffit of roof over fourth floor.

ELEMENT KEY

- Masonry wall faces
- Embedded roof beams
- Exposed roof members
- Soffit scan - location 1

Rev	Issue	Drawn	Chkd	Date
1	REVIEW	AT	AF	04-11-26

Consultant:

KA ENGINEERING GROUP

Client: JetNSL

JET network solutions

Drawing Title:

Roof Support Layout

SAFFRON WALDEN TOWER

Mount Pleasant Road, Saffron Walden
Essex CB11 4GA

Drawn: AT Checked: AF

7145-01 | Rev 1 NTS