
DIMENSIONS IN mm; LEVELS ABOVE GROUND


SECTIONAL ELEVATION

Clear heights and slab thicknesses

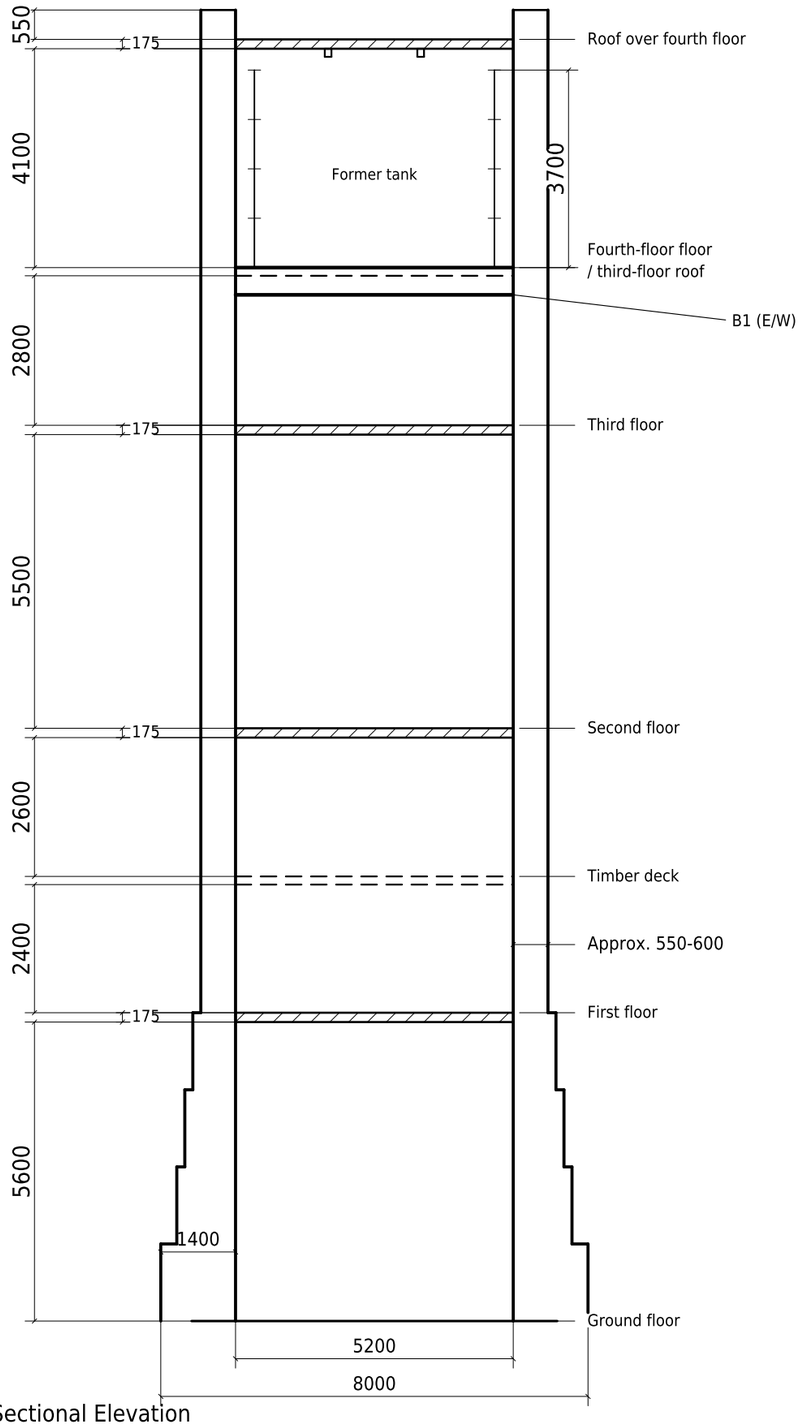


1 Sectional Elevation

NTS

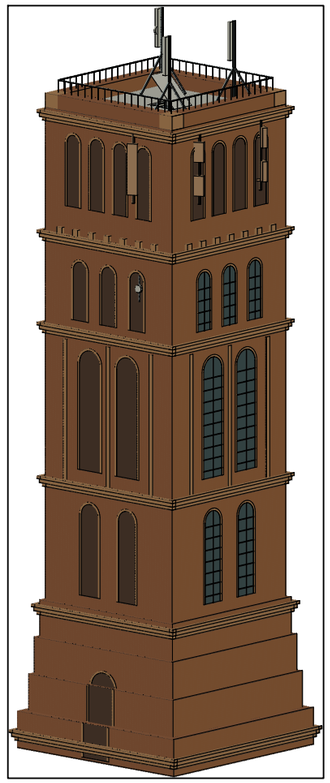

2 Tower

3D NTS

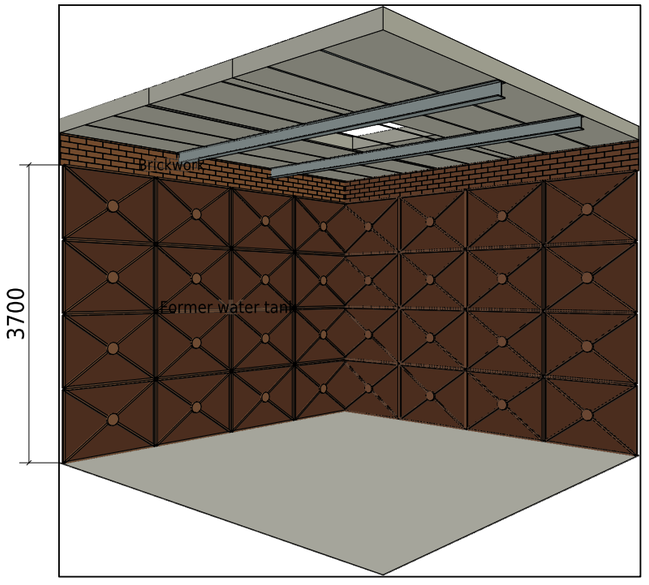

3 Fourth-Floor Interior

3D NTS

DRAWING NOTES

1. All height dimensions are floor to ceiling; concrete slabs 175 thick shown separately.
2. B1: 510 x 190, flange 20; at fourth-floor FLOOR / third-floor ROOF.
3. Fourth-floor steel floor and intermediate timber-deck build-ups not measured.
4. Ribbed panels are the former water tank.

ELEMENT KEY

Concrete slab

Steel floor

Intermediate timber deck

B1 Primary E/W beam at floor 4

Rev	Issue	Drawn	Chkd	Date
1	REVIEW	AT	AF	04-11-26

Consultant:

KA ENGINEERING GROUP

Client: JetNSL

JET network solutions

Drawing Title:

Elevation / 3D Views

SAFFRON WALDEN TOWER

Mount Pleasant Road, Saffron Walden
Essex CB11 4GA

Drawn: AT Checked: AF

7145-02 | Rev 1 NTS