cornerstone

CORNERSTONE – BEACON 4

Pack Issue:	Option:
1A	–

CELL NAME: SAFFRON WALDEN TOWER

circet UK

Unit 27F-G, Hartlebury Trading Estate, Crown Lane, Hartlebury, Worcestershire, DY10 4JD

✓ INDICATES MNO(S)/SHARER WITH LIVE DEMAND IN PROGRESS

CSID	– TEF	– VF
111051	8233	75548
PROJECT No.	– TM Cell ID	– N/A
147	–	–

PASSIVE SCOPE OF WORKS:

EXISTING 1No. CABINET TO BE REMOVED & REPLACED WITH ALLOCATED TEF 1No. CABINET WITHIN EQUIPMENT ROOM (INDOOR).


ACTIVE SCOPE OF WORKS:

EXISTING TEF 6No. ANTENNAS TO BE REMOVED & REPLACED WITH ALLOCATED TEF 9No. ANTENNAS.
EXISTING TEF 12No. RRU's TO BE REMOVED & REPLACED WITH ALLOCATED 15No. RRU's.

DRAWING TITLE	DRAWING No.	DATE OF ISSUE	21.10.25						
		REV	REV	REV	REV	REV	REV	REV	
Site Location Maps	100	1A							
Lease Agreement Plan	101	1A							
Existing Site Plan	200	1A							
Proposed Site Plan	201	1A							
Existing Site Elevation	300	1A							
Proposed Site Elevation	301	1A							
Existing Antenna Plan	400	1A							
Existing RRU Plan	401	1A							
Allocated Antenna Plan	402	1A							
Allocated RRU Plan	403	1A							
Allocated Equipment Layout	404	1A							
Occupational ICNIRP Zone Plan	450	1A							
Occupational ICNIRP Zone Elevation	451	1A							
Public ICNIRP Zone Plan	452	1A							
Public ICNIRP Zone Elevation	453	1A							
Existing TEF R.F. System	500	1A							
Allocated TEF R.F. System Schematic	550	1A							
Allocated TEF Antenna Schedule	551	1A							
TEF Equipment Schedule	570	1A							

ROLE	EMAIL	ISSUED						
TEF Delivery Manager	Peter.Oshaughnessy@virginmediao2.co.uk	✓						
TEF TX Planner	Reece.Balmer2@virginmediao2.co.uk	✓						
TEF Radio Planner	Peter.Durant@virginmediao2.co.uk	✓						

SITE LOCATION

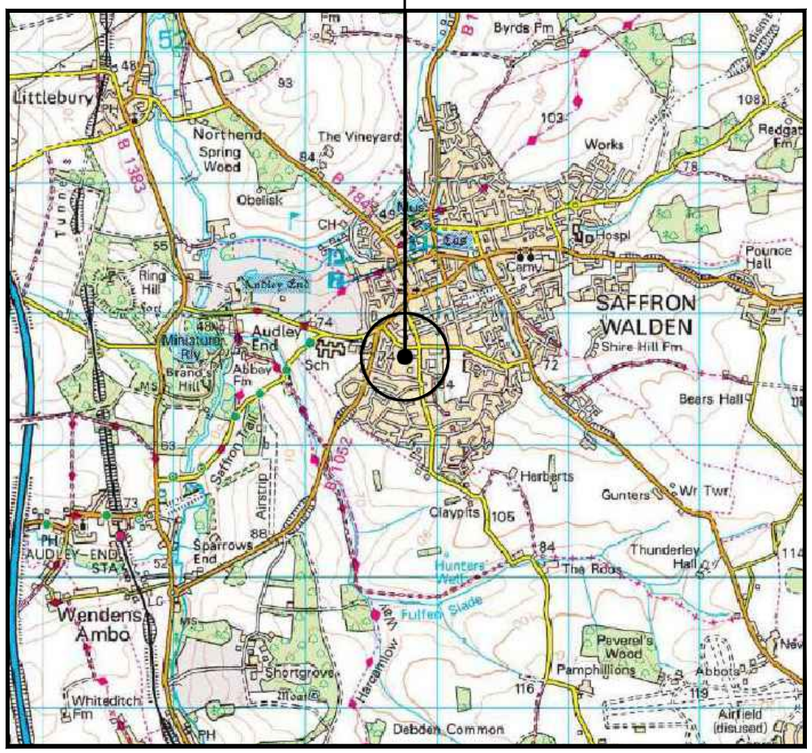

SITE LOCATION
(Scale 1:50000)

Ordnance Survey map extract based upon Landranger map series with the permission of the controller of His Majesty's Stationery Office Licence No. 100022432 Crown copyright.

0 500 1000 1500 2000 2500m
1:50000




SITE PHOTOGRAPH

N
W E
S

= Right of Access
= Public Access Route

SITE LOCATION
W3W REF:
MANAGED.SIDEBURNS.EDIT

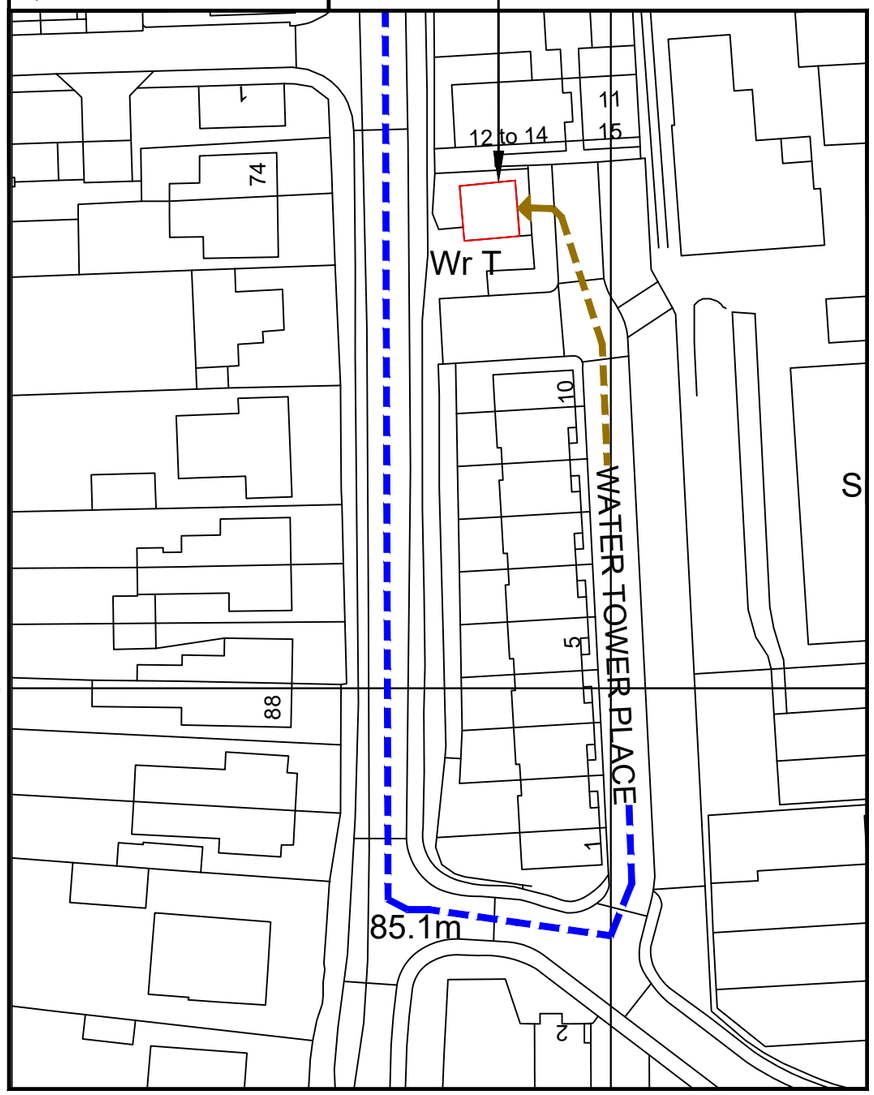

DETAILED SITE LOCATION
(Scale 1:1250)

Based upon Ordnance Survey map extract with the permission of the Controller of His Majesty's Stationery Office. Crown copyright. Licence No. 100022432

0 12.5 25 37.5 50 62.5m
1:1250

ALL DIMENSIONS ARE IN mm UNLESS NOTED OTHERWISE

N.G.R	E: 553884	N: 237653

DIRECTIONS TO SITE: EXIT THE M11 AT JUNCTION 10. AT THE ROUNDABOUT TAKE THE FIRST EXIT ONTO THE A505, GO THROUGH ONE ROUNDABOUT, THEN AT THE NEXT ROUNDABOUT TAKE THE THIRD EXIT ONTO THE A1301. PROCEED THROUGH 2 ROUNDABOUTS THEN AT THE NEXT ROUNDABOUT TAKE THE 1ST EXIT ONTO THE B184. CONTINUE ALONG THE B184 THEN BEAR RIGHT ONTO THE B1052. TURN LEFT ONTO DEBDEN ROAD AND SITE IS LOCATED ON THE LEFT. TO ENTER SITE TURN LEFT ONTO THE AVENUE AND THEN TURN LEFT ONTO WATER TOWER PLACE. TO GAIN ENTRANCE TO WATER TOWER/SITE YOU MUST FIRST REPORT TO SCHOOL RECEPTION TO OBTAIN A COMPOUND GATE KEY THEN USE KEY PAD CODE: CZ1702 TO ENTER EQUIPMENT ROOM AT BASE OF TOWER.

NOTES:

REV	MODIFICATION	BY	CH	DATE
1A	PLANNING ISSUE	VW	RF	21.10.25

circet UK
Unit 27F-G, Hartlebury Trading Estate, Crown Lane, Hartlebury, Worcestershire, DY10 4JD

cornerstone

Cell Name	Opt.
SAFFRON WALDEN TOWER	–

Cell ID No

CSID	– TEF	– VF
111051	8233	75548
Project No.	– TM Cell ID	– N/A
147	–	–

Site Address / Contact Details

FRIENDS OF SCHOOL WATER TOWER MOUNT
PLEASANT ROAD
SAFFRON WALDEN
ESSEX
CB11 4GA

Drawing Title: SITE LOCATION MAPS

Purpose of issue: PLANNING — Dwg Rev: 1A

Drawing Number: 100


Surveyed By:	Original Sheet Size:	Pack Issue:
CIRCET	A3	1A

Drawn:	Date:	Checked:	Date:
VW	21.10.25	RF	21.10.25

= Right of Access

= Public Access Route

SITE LOCATION
W3W REF:
MANAGED.SIDEBURNS.EDIT

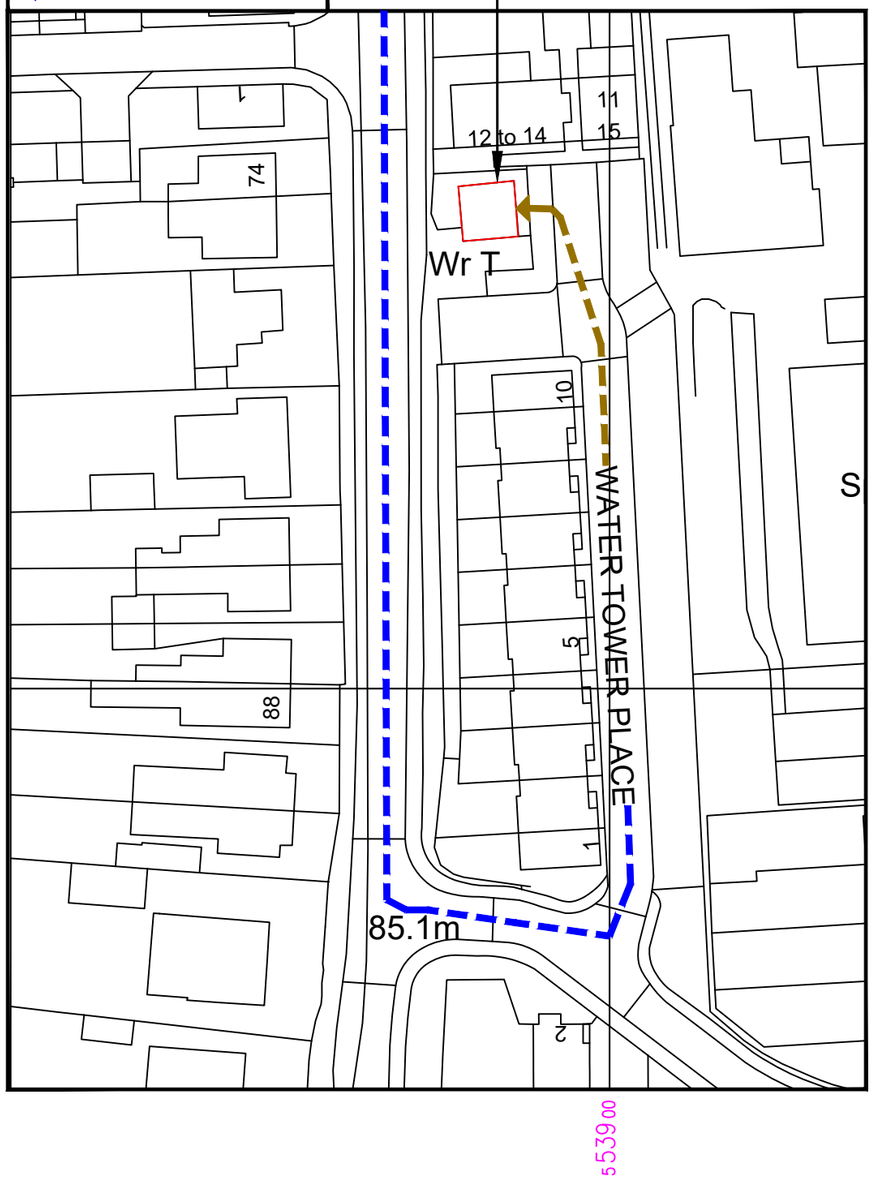


DETAILED SITE LOCATION

(Scale 1:1250)

Based upon Ordnance Survey map extract with the permission of the Controller of His Majesty's Stationery Office. Crown copyright. Licence No. 100022432

0 12.5 25 37.5 50 62.5m
1:1250

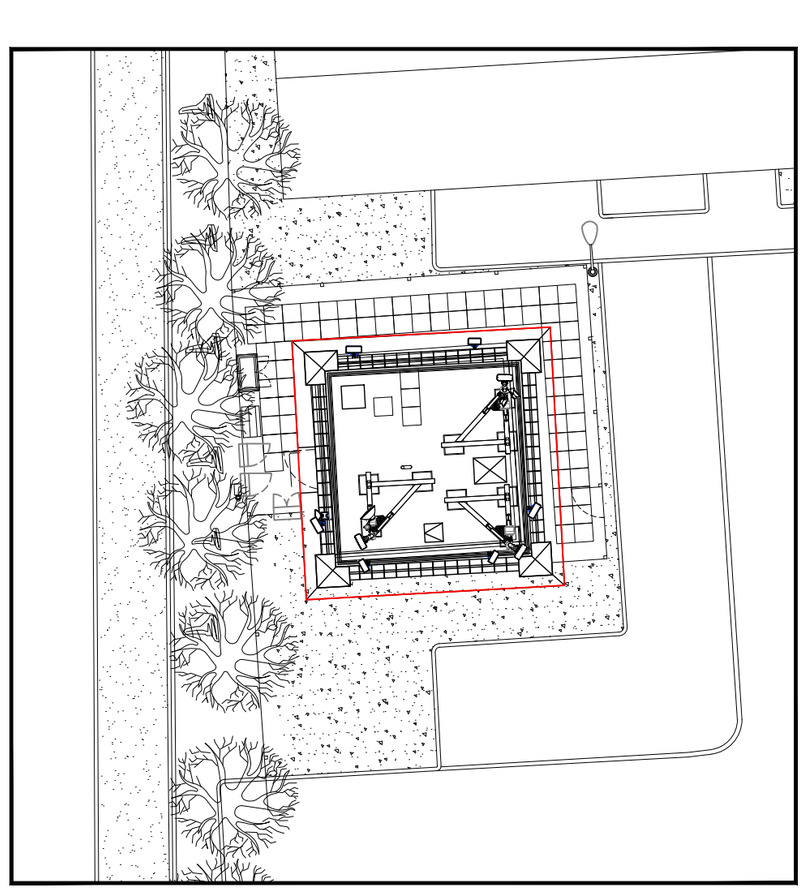

SITE PLAN

(Scale 1:200)

0 2 4 6 8 10m
1:200

ALL DIMENSIONS ARE IN mm UNLESS NOTED OTHERWISE

N.G.R | E: 553884 | N: 237653

NOTES:

REV				
1A	PLANNING ISSUE	VW	RF	21.10.25
REV	MODIFICATION	BY	CH	DATE

circet UK
Unit 27F-G, Hartlebury Trading Estate, Crown Lane, Hartlebury, Worcestershire, DY10 4JD

cornerstone

Cell Name	Opt.
SAFFRON WALDEN TOWER	–

Cell ID No

CSID	– TEF	– VF
111051	8233	75548
Project No.	– TM Cell ID	– N/A
147	–	–

Site Address / Contact Details

FRIENDS OF SCHOOL WATER TOWER MOUNT
PLEASANT ROAD
SAFFRON WALDEN
ESSEX
CB11 4GA


Drawing Title: LEASE AGREEMENT PLAN

Purpose of issue: PLANNING — Dwg Rev: 1A

Drawing Number: 101

Surveyed By:	Original Sheet Size:	Pack Issue:
CIRCET	A3	1A

Drawn:	Date:	Checked:	Date:
VW	21.10.25	RF	21.10.25

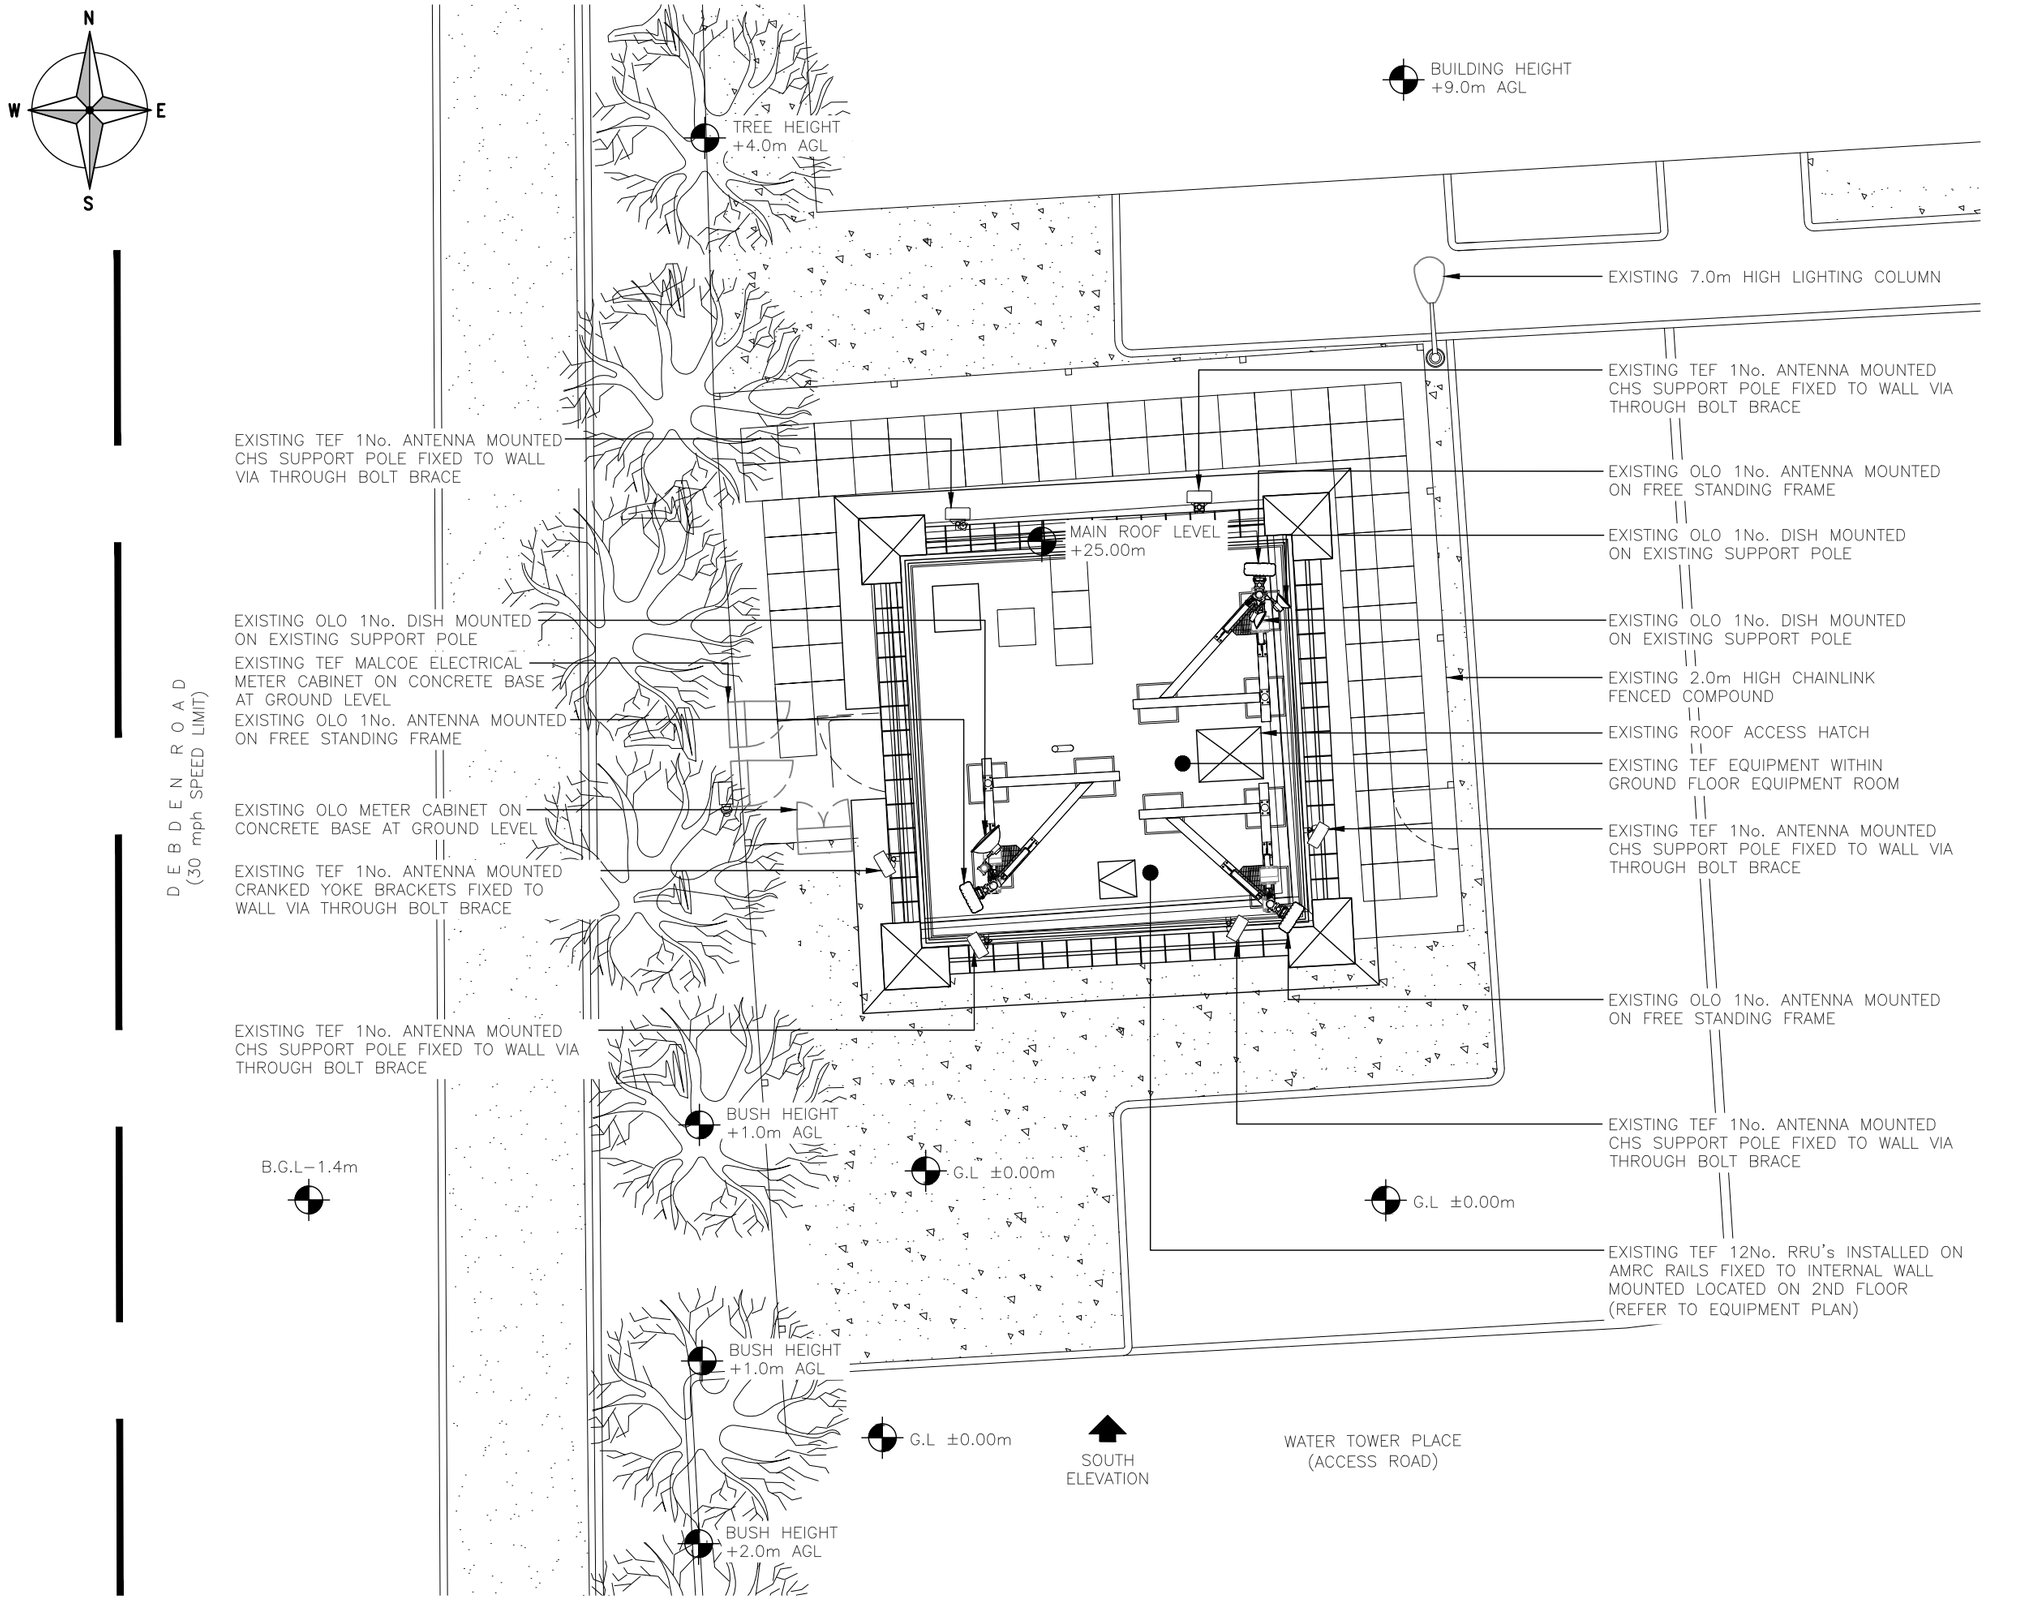

EXISTING SITE PLAN

(1:100)

0 1 2 3 4 5m

1:100

ALL DIMENSIONS ARE IN mm UNLESS NOTED OTHERWISE

N.G.R E: 553884 N: 237653

NOTES:

REV	MODIFICATION	BY	CH	DATE
1A	PLANNING ISSUE	W	RF	21.10.25

circet UK

Unit 27F-G, Hartlebury Trading Estate, Crown Lane, Hartlebury, Worcestershire, DY10 4JD

cornerstone

Cell Name	Opt.
SAFFRON WALDEN TOWER	–

Cell ID No

CSID	– TEF	– VF
111051	8233	75548
Project No.	– TM Cell ID	– N/A
147	–	–

Site Address / Contact Details

FRIENDS OF SCHOOL WATER TOWER MOUNT
PLEASANT ROAD
SAFFRON WALDEN
ESSEX
CB11 4GA


Drawing Title: EXISTING SITE PLAN

Purpose of issue: PLANNING — Dwg Rev: 1A

Drawing Number: 200

Surveyed By:	Original Sheet Size:	Pack Issue:
CIRCET	A3	1A

Drawn:	Date:	Checked:	Date:
W	21.10.25	RF	21.10.25

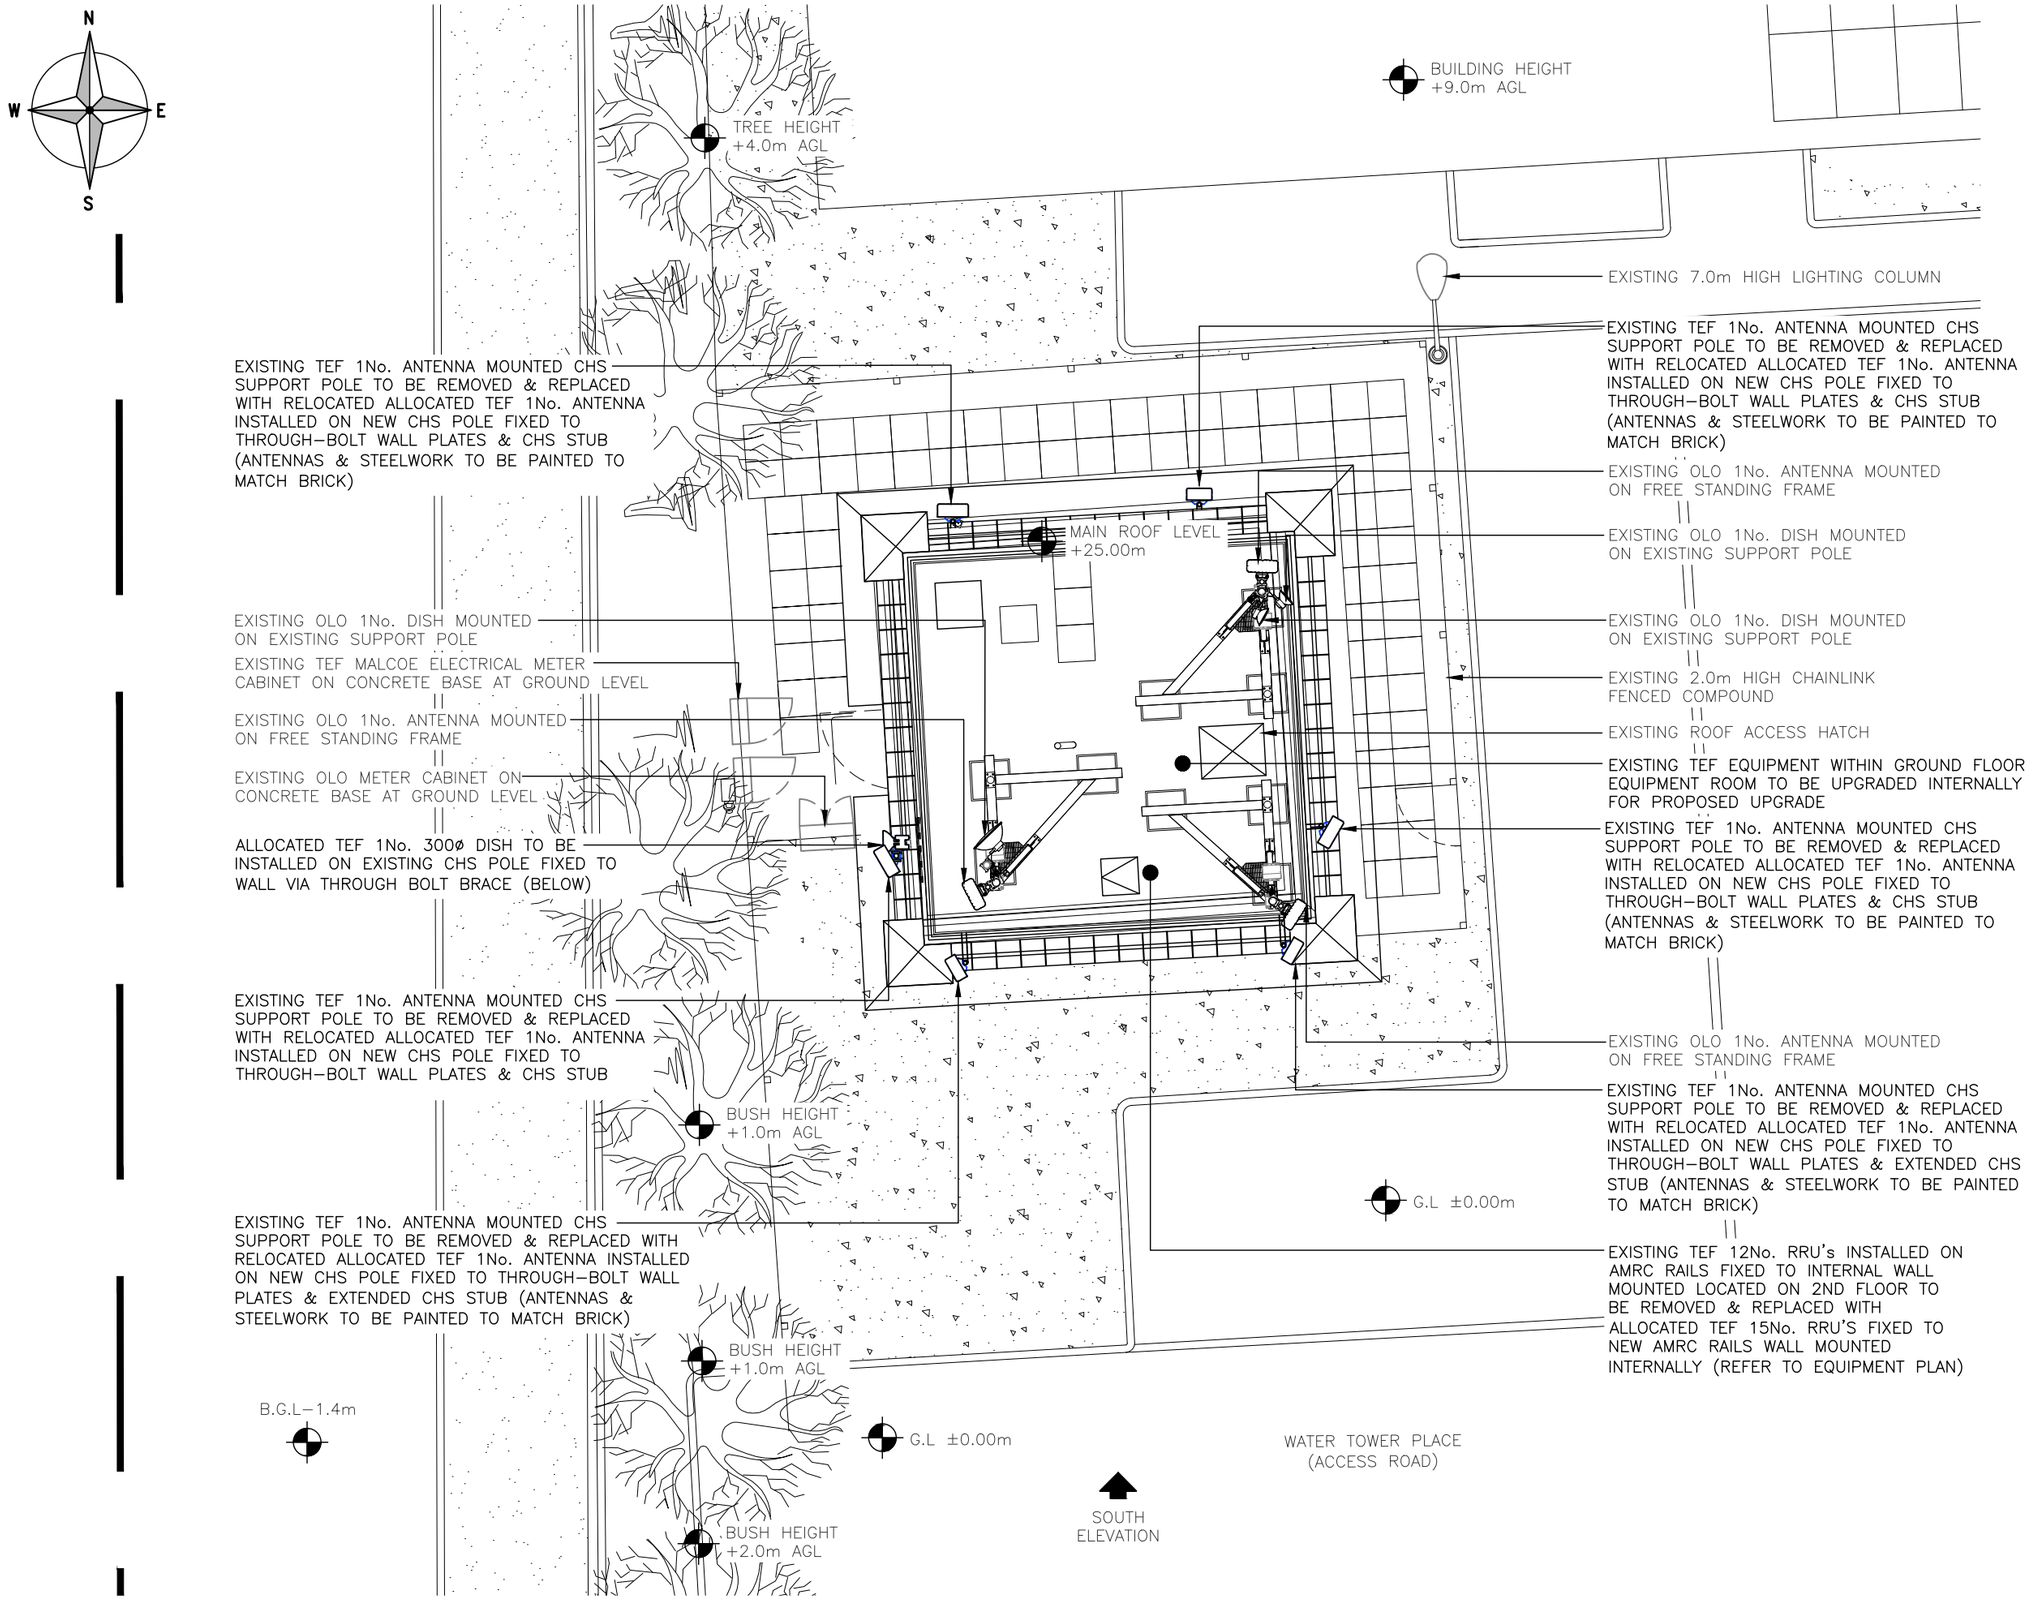

PROPOSED SITE PLAN

(1:100)

0 1 2 3 4 5m

1:100

ALL DIMENSIONS ARE IN mm UNLESS NOTED OTHERWISE

N.G.R E: 553884 N: 237653

NOTES:

REV	MODIFICATION	BY	CH	DATE
1A	PLANNING ISSUE	W	RF	21.10.25

circet UK

Unit 27F-G, Hartlebury Trading Estate, Crown Lane, Hartlebury, Worcestershire, DY10 4JD

cornerstone

Cell Name	Opt.
SAFFRON WALDEN TOWER	–

Cell ID No

CSID	– TEF	– VF
111051	8233	75548
Project No.	– TM Cell ID	– N/A
147	–	–

Site Address / Contact Details

FRIENDS OF SCHOOL WATER TOWER MOUNT
PLEASANT ROAD
SAFFRON WALDEN
ESSEX
CB11 4GA


Drawing Title: PROPOSED SITE PLAN

Purpose of issue: PLANNING — Dwg Rev: 1A

Drawing Number: 201

Surveyed By:	Original Sheet Size:	Pack Issue:
CIRCET	A3	1A

Drawn:	Date:	Checked:	Date:
W	21.10.25	RF	21.10.25

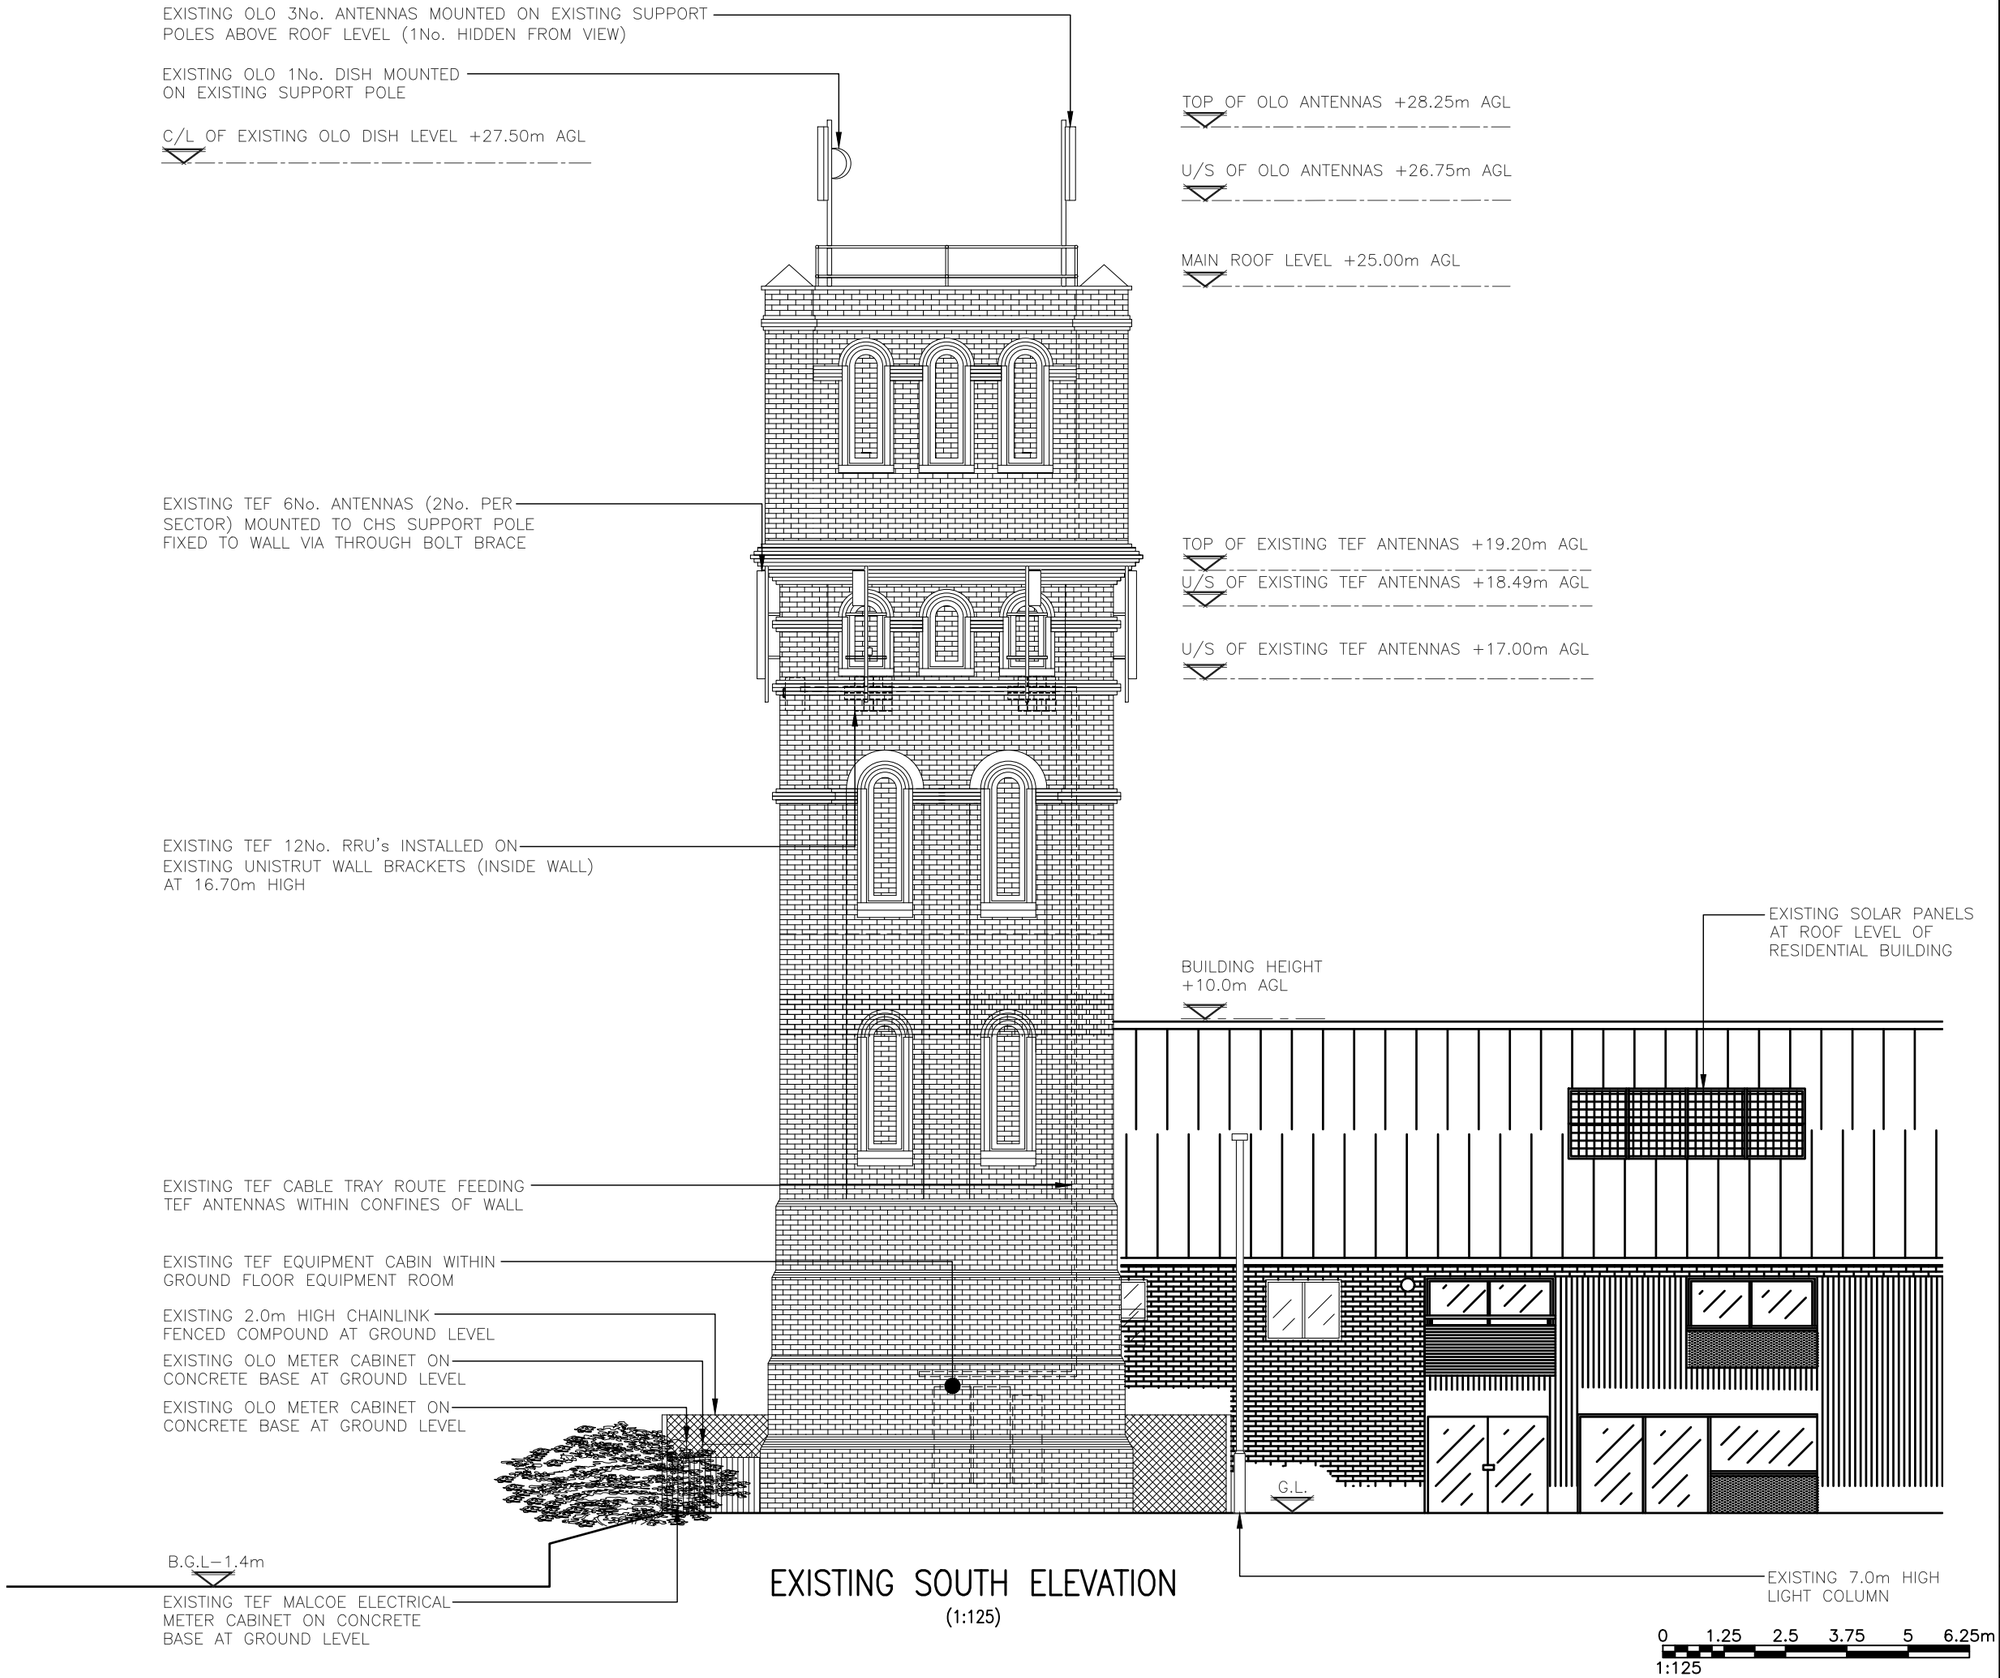

EXISTING SOUTH ELEVATION

(1:125)

ALL DIMENSIONS ARE IN mm UNLESS NOTED OTHERWISE

N.G.R | E: 553884 | N: 237653

NOTES:

REV	MODIFICATION	BY	CH	DATE
1A	PLANNING ISSUE	W	RF	21.10.25

circet UK
Unit 27F-G, Hartlebury Trading Estate, Crown Lane, Hartlebury, Worcestershire, DY10 4JD

cornerstone

Cell Name	Opt.
SAFFRON WALDEN TOWER	–

Cell ID No

CSID	– TEF	– VF
111051	8233	75548
Project No.	**– TM Cell ID**	**– N/A**
147	–	–

Site Address / Contact Details


FRIENDS OF SCHOOL WATER TOWER MOUNT
PLEASANT ROAD
SAFFRON WALDEN
ESSEX
CB11 4GA

Drawing Title: EXISTING SITE ELEVATION

Purpose of issue:	Dwg Rev:
PLANNING	1A

Drawing Number:	Surveyed By:	Original Sheet Size:	Pack Issue:
300	CIRCET	A3	1A

Drawn:	Date:	Checked:	Date:
W	21.10.25	RF	21.10.25

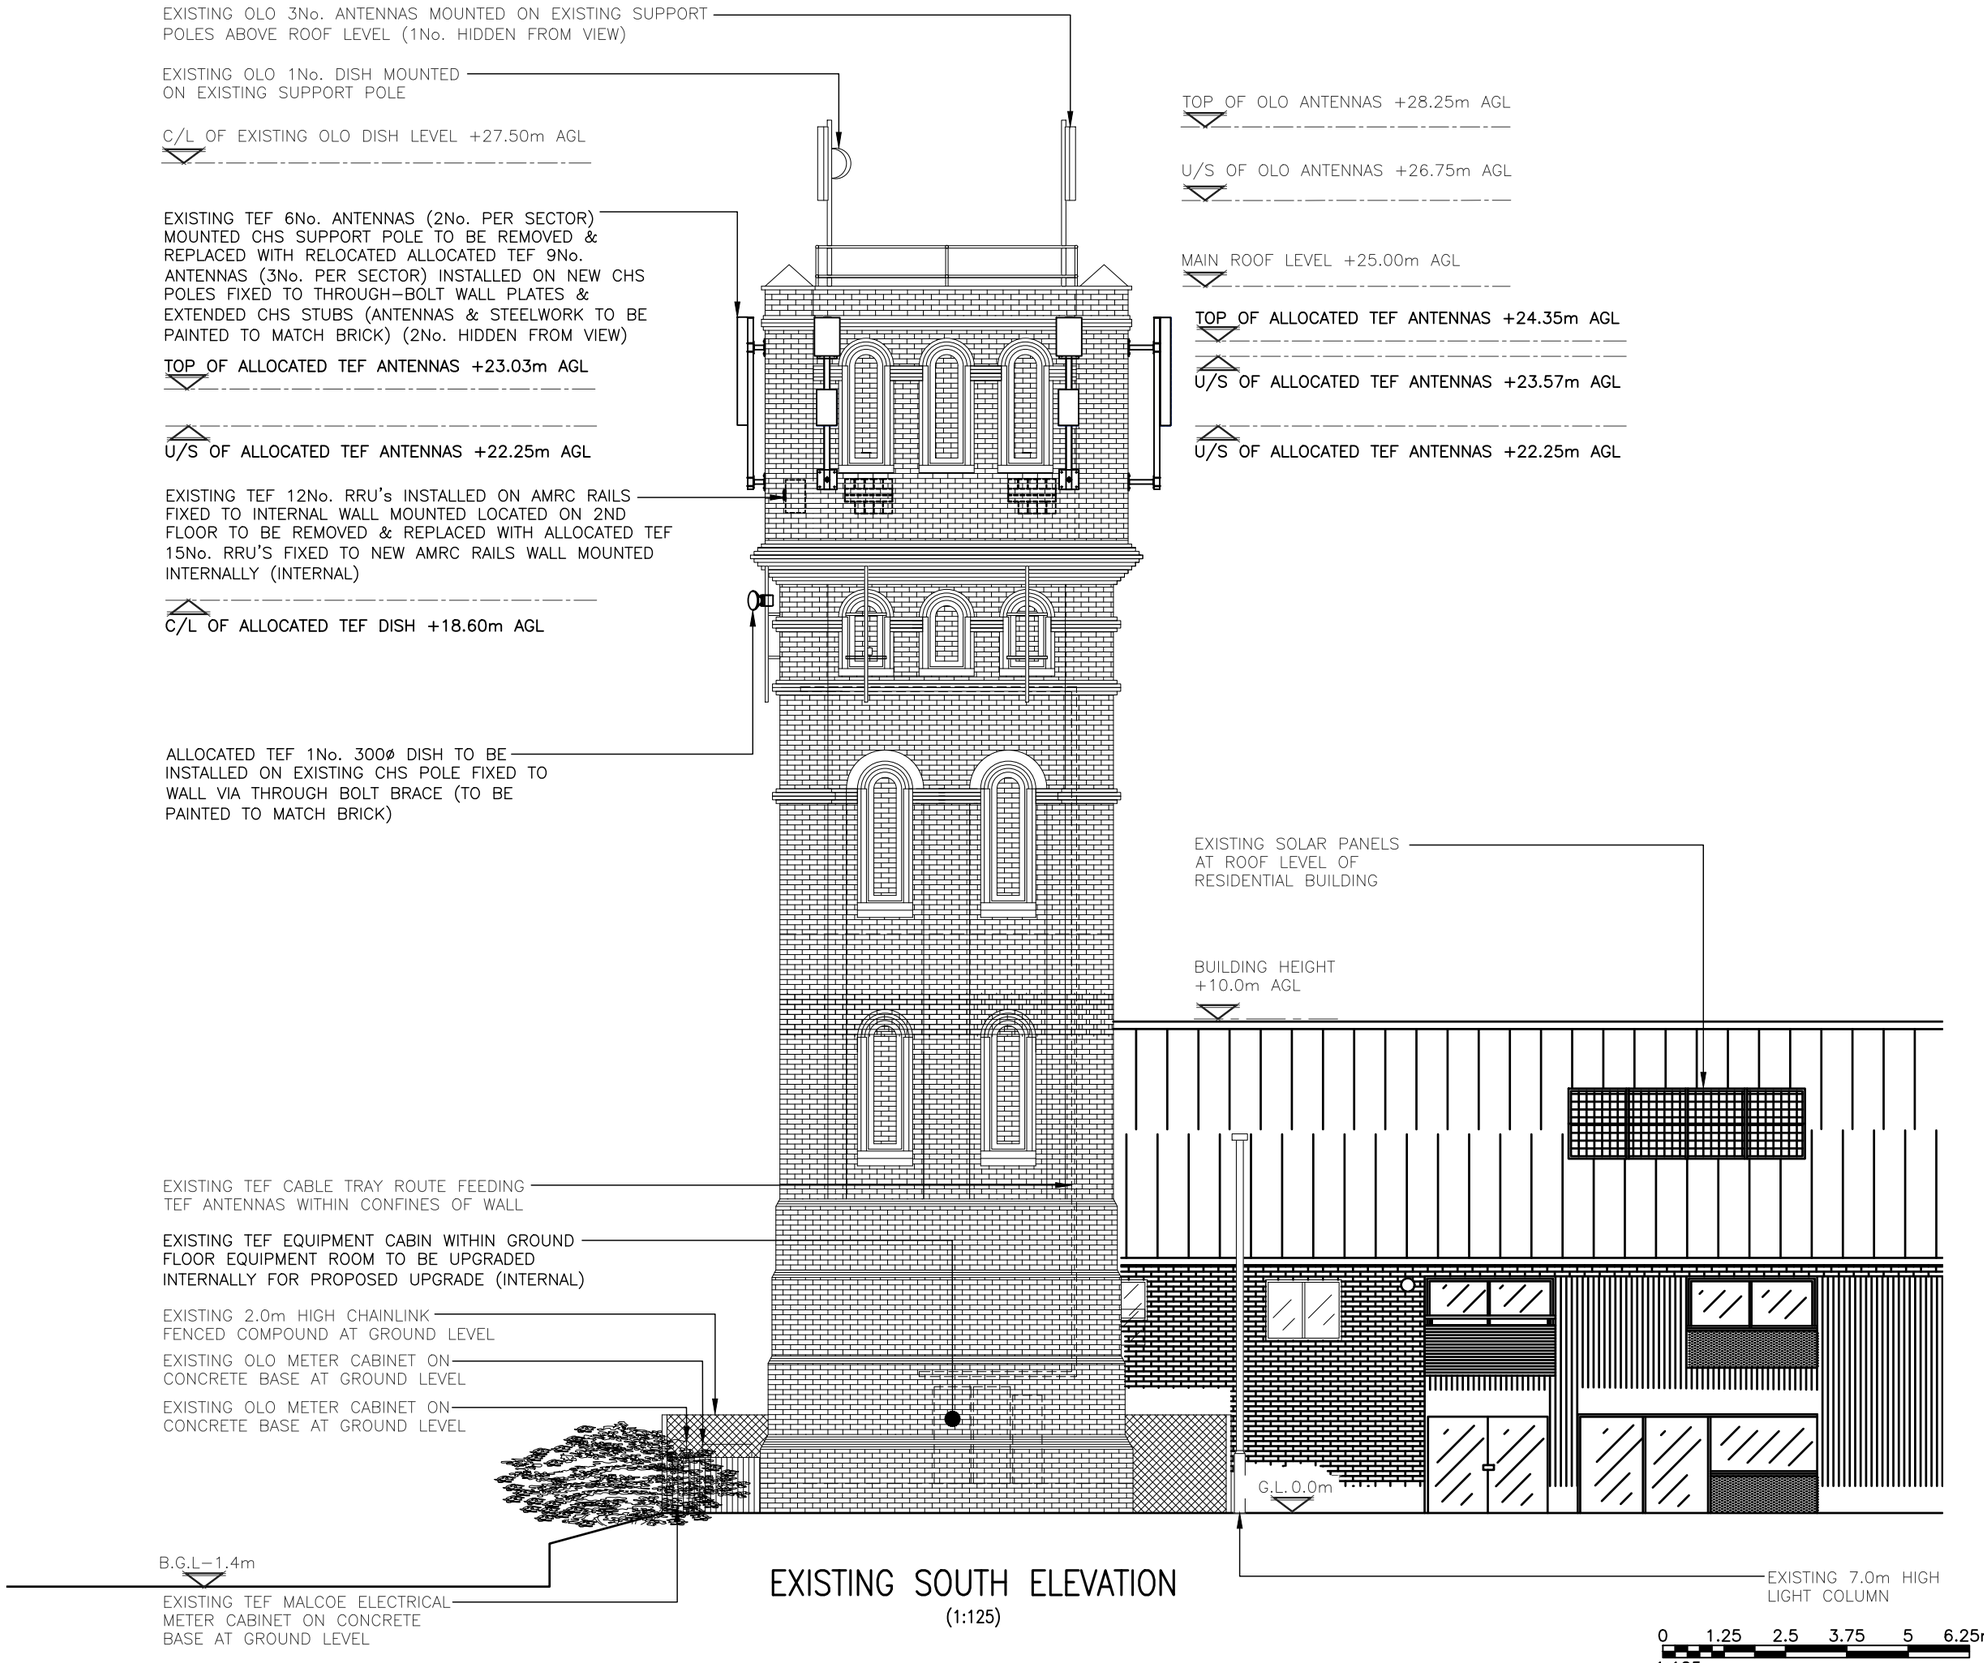

EXISTING SOUTH ELEVATION
(1:125)

ALL DIMENSIONS ARE IN mm UNLESS NOTED OTHERWISE

N.G.R E: 553884 N: 237653

NOTES:

REV	MODIFICATION	BY	CH	DATE
1A	PLANNING ISSUE	W	RF	21.10.25

circet UK
Unit 27F-G, Hartlebury Trading Estate, Crown Lane, Hartlebury, Worcestershire, DY10 4JD

cornerstone

Cell Name	Opt.
SAFFRON WALDEN TOWER	–

Cell ID No

CSID	– TEF	– VF
111051	8233	75548
Project No.	– TM Cell ID	– N/A
147	–	–

Site Address / Contact Details

FRIENDS OF SCHOOL WATER TOWER MOUNT
PLEASANT ROAD
SAFFRON WALDEN
ESSEX
CB11 4GA

Drawing Title: PROPOSED SITE ELEVATION

Purpose of issue: PLANNING — Dwg Rev: 1A


Drawing Number: 301

Surveyed By:	Original Sheet Size:	Pack Issue:
CIRCET	A3	1A

Drawn:	Date:	Checked:	Date:
W	21.10.25	RF	21.10.25



ITEM DESCRIPTION	QTY
EXISTING ANTENNAS	2

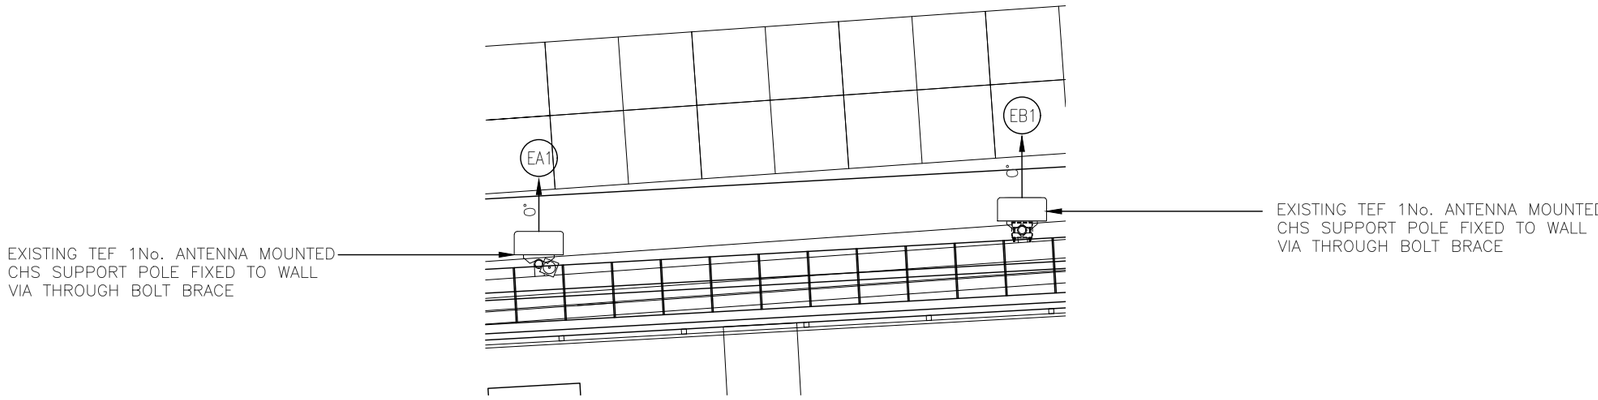

EXISTING ANTENNA PLAN @18.10m/17.74m AGL

(1:50)

0 0.5 1 1.5 2 2.5m

1:50

ALL DIMENSIONS ARE IN mm UNLESS NOTED OTHERWISE


N.G.R E: 553884 N: 237653

EQUIPMENT COLOUR KEY

EXISTING EQUIPMENT	
TEF EQUIPMENT ALLOCATED	
TEF PROPOSED EQUIPMENT	
NEUTRAL FOOTPRINT	

NOTES:

ITEM DESCRIPTION	QTY
EXISTING ANTENNAS	2

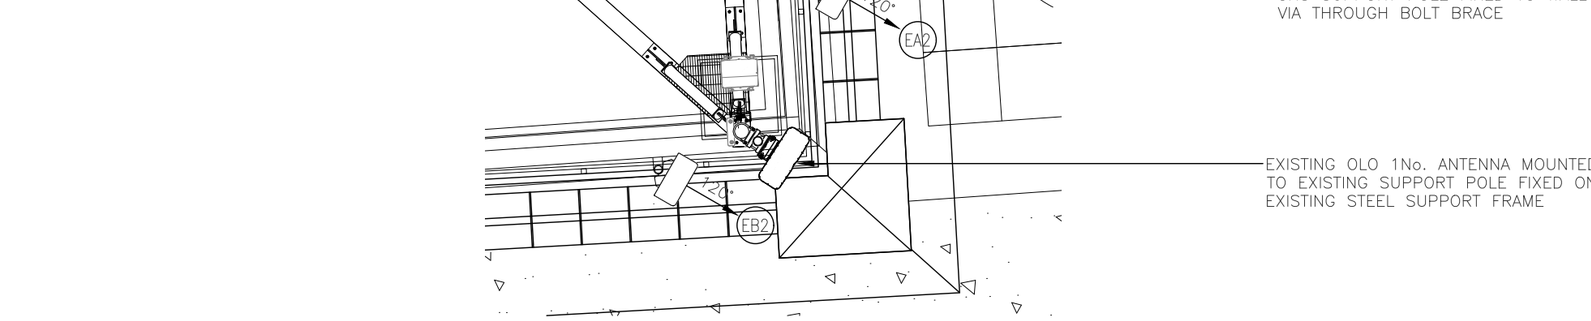

EXISTING ANTENNA PLAN @18.10m/17.74m AGL

(1:50)


0 0.5 1 1.5 2 2.5m

1:50


REV	MODIFICATION	BY	CH	DATE
1A	PLANNING ISSUE	W	RF	21.10.25

circet UK
Unit 27F-G, Hartlebury Trading Estate, Crown Lane, Hartlebury, Worcestershire, DY10 4JD

cornerstone

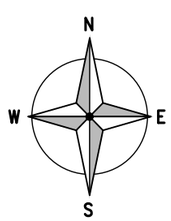

ITEM DESCRIPTION	QTY
EXISTING ANTENNAS	2

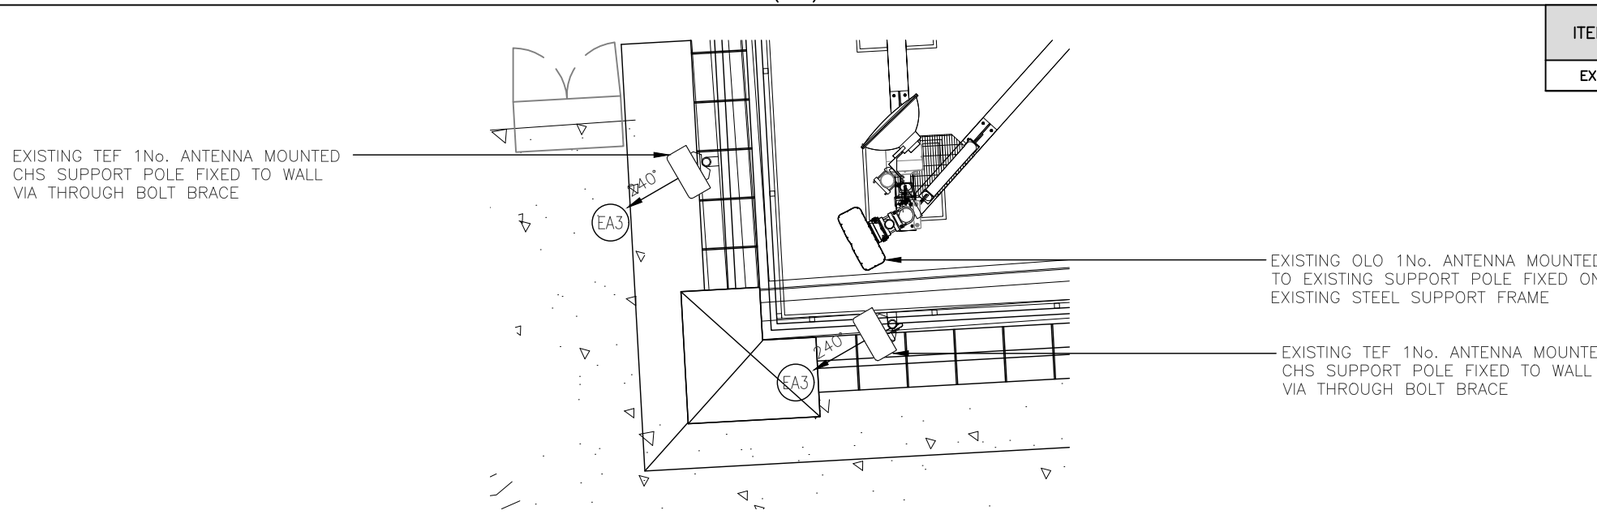

EXISTING ANTENNA PLAN @18.10m/17.74m AGL

(1:50)

0 0.5 1 1.5 2 2.5m

1:50

Cell Name	Opt.
SAFFRON WALDEN TOWER	–

Cell ID No

CSID	– TEF	– VF
111051	8233	75548
Project No.	– TM Cell ID	– N/A
147	–	–

Site Address / Contact Details

FRIENDS OF SCHOOL WATER TOWER MOUNT
PLEASANT ROAD
SAFFRON WALDEN
ESSEX
CB11 4GA

Drawing Title: EXISTING ANTENNA PLAN


Purpose of issue:	Dwg Rev:
PLANNING	1A
Drawing Number: 400	

Surveyed By:	Original Sheet Size:	Pack Issue:
CIRCET	A3	

Drawn:	Date:	Checked:	Date:	
W	21.10.25	RF	21.10.25	1A



ITEM DESCRIPTION	QTY
EXISTING RRUS	12

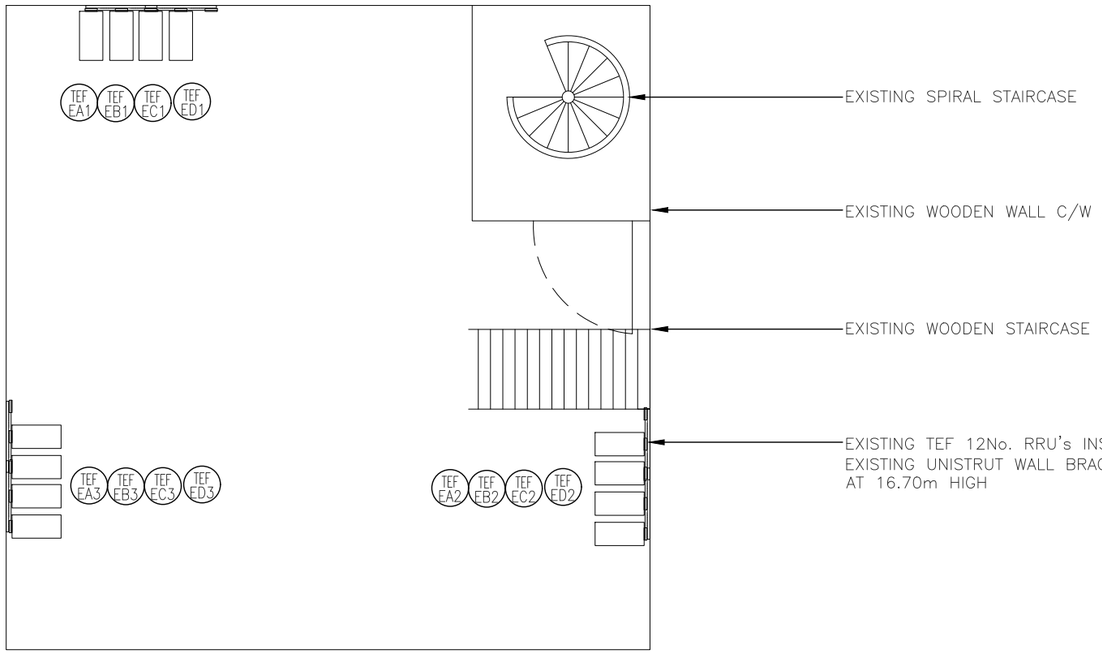

EXISTING RRU PLAN @16.70 AGL 2ND FLOOR

(1:50)

0 0.5 1 1.5 2 2.5m

1:50

ALL DIMENSIONS ARE IN mm UNLESS NOTED OTHERWISE

N.G.R E: 553884 N: 237653

EQUIPMENT COLOUR KEY

EXISTING EQUIPMENT	
TEF EQUIPMENT ALLOCATED	
TEF PROPOSED EQUIPMENT	
NEUTRAL FOOTPRINT	

NOTES:

REV	MODIFICATION	BY	CH	DATE
1A	PLANNING ISSUE	W	RF	21.10.25

circet UK
Unit 27F-G, Hartlebury Trading Estate, Crown Lane, Hartlebury, Worcestershire, DY10 4JD

cornerstone

Cell Name	Opt.
SAFFRON WALDEN TOWER	–

Cell ID No

CSID	– TEF	– VF
111051	8233	75548
Project No.	– TM Cell ID	– N/A
147	–	–

Site Address / Contact Details

FRIENDS OF SCHOOL WATER TOWER MOUNT
PLEASANT ROAD
SAFFRON WALDEN
ESSEX
CB11 4GA

Drawing Title: EXISTING RRU PLAN


Purpose of issue:	Dwg Rev:
PLANNING	1A

Drawing Number:	
401	1A

Surveyed By:	Original Sheet Size:	Pack Issue:
CIRCET	A3	

Drawn:	Date:	Checked:	Date:	
W	21.10.25	RF	21.10.25	1A



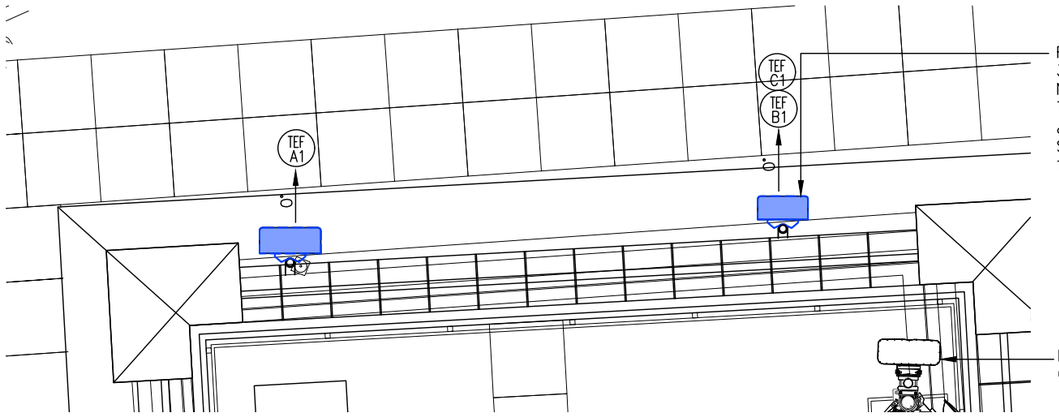

ALLOCATED ANTENNA PLAN S1 @23.25m, 23.96m, 22.64m AGL


(1:50)

ITEM DESCRIPTION	QUANTITY
AFF3	1
AFF1	1
AFF6	1

0 0.5 1 1.5 2 2.5m

1:50



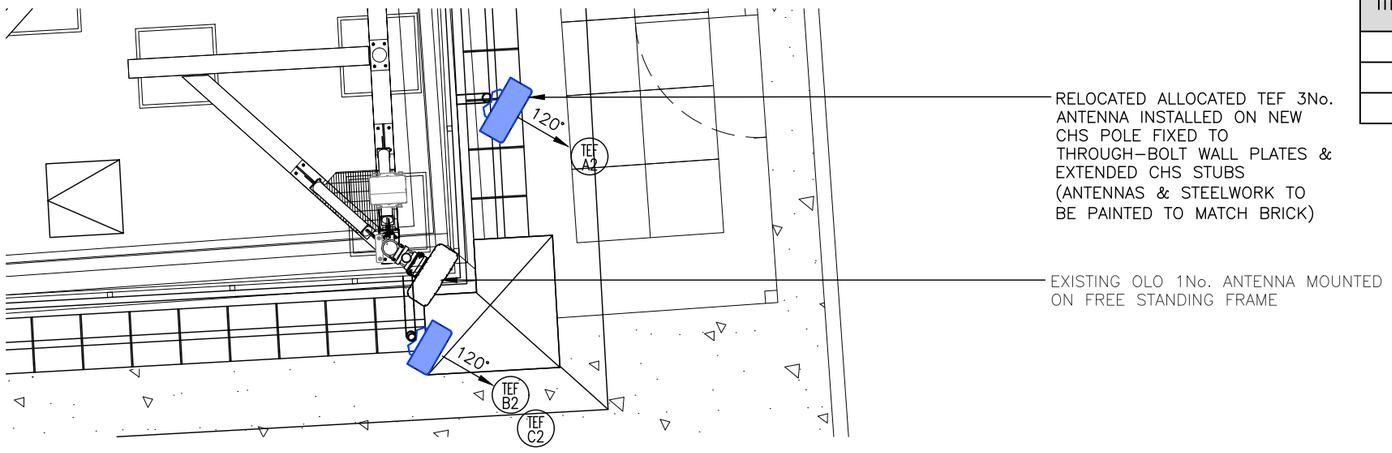

ALLOCATED ANTENNA PLAN S2 @23.25m, 23.96m, 22.64m AGL


(1:50)

ITEM DESCRIPTION	QUANTITY
AFF3	1
AFF1	1
AFF6	1

0 0.5 1 1.5 2 2.5m

1:50



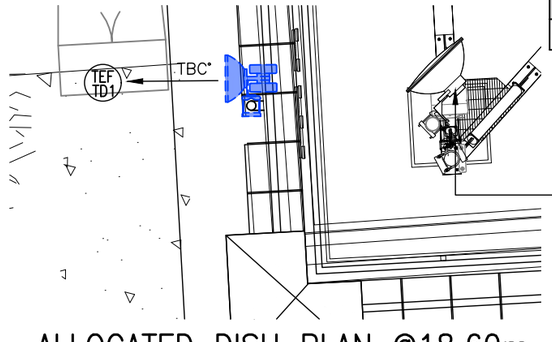

ALLOCATED DISH PLAN @18.60m AGL

(1:50)


ITEM DESCRIPTION	QUANTITY
DFF1	1

0 0.5 1 1.5 2 2.5m

1:50

ALLOCATED DISH SCHEDULE

STATUS	OPERATOR	DISH REF	DESIGN REFERENCE	DIMENSIONS (ØxD)	DISH BEARING (°)	LOCATION	HEIGHT (C/L)
ALLOCATED	TEF	TD1	DFF1	300mmØ	TBC	EXISTING POLE	+18.60m

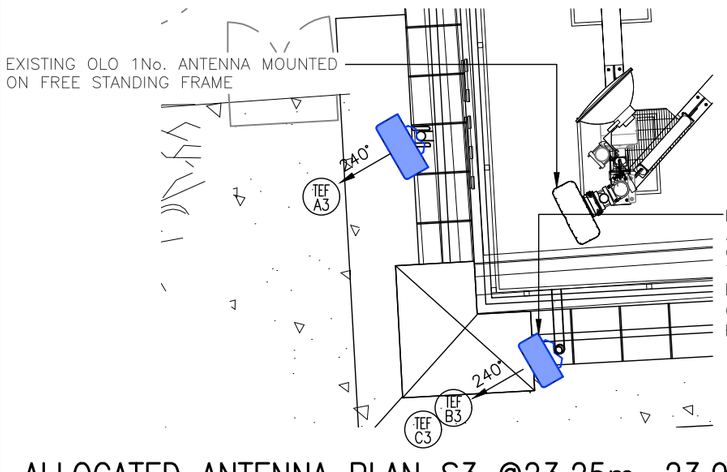

ALLOCATED ANTENNA PLAN S3 @23.25m, 23.96m, 22.64m AGL

(1:50)

ITEM DESCRIPTION	QUANTITY
AFF3	1
AFF1	1
AFF6	1

0 0.5 1 1.5 2 2.5m

1:50

ALL DIMENSIONS ARE IN mm UNLESS NOTED OTHERWISE

N.G.R E: 553884 N: 237653

EQUIPMENT COLOUR KEY

EXISTING EQUIPMENT	
TEF EQUIPMENT ALLOCATED	
TEF PROPOSED EQUIPMENT	
NEUTRAL FOOTPRINT	

NOTES:

REV	MODIFICATION	BY	CH	DATE
1A	PLANNING ISSUE	W	RF	21.10.25

circet UK

Unit 27F-G, Hartlebury Trading Estate, Crown Lane, Hartlebury, Worcestershire, DY10 4JD

cornerstone

Cell Name	Opt.
SAFFRON WALDEN TOWER	–

Cell ID No

CSID	– TEF	– VF
111051	8233	75548
Project No.	– TM Cell ID	– N/A
147	–	–

Site Address / Contact Details

FRIENDS OF SCHOOL WATER TOWER MOUNT
PLEASANT ROAD
SAFFRON WALDEN
ESSEX
CB11 4GA

Drawing Title: ALLOCATED ANTENNA PLAN

Purpose of issue: PLANNING — Dwg Rev: 1A


Drawing Number: 402

Surveyed By:	Original Sheet Size:	Pack Issue:
CIRCET	A3	1A

Drawn:	Date:	Checked:	Date:
W	21.10.25	RF	21.10.25



ITEM DESCRIPTION	QUANTITY
RFF1	12
RFF2	3

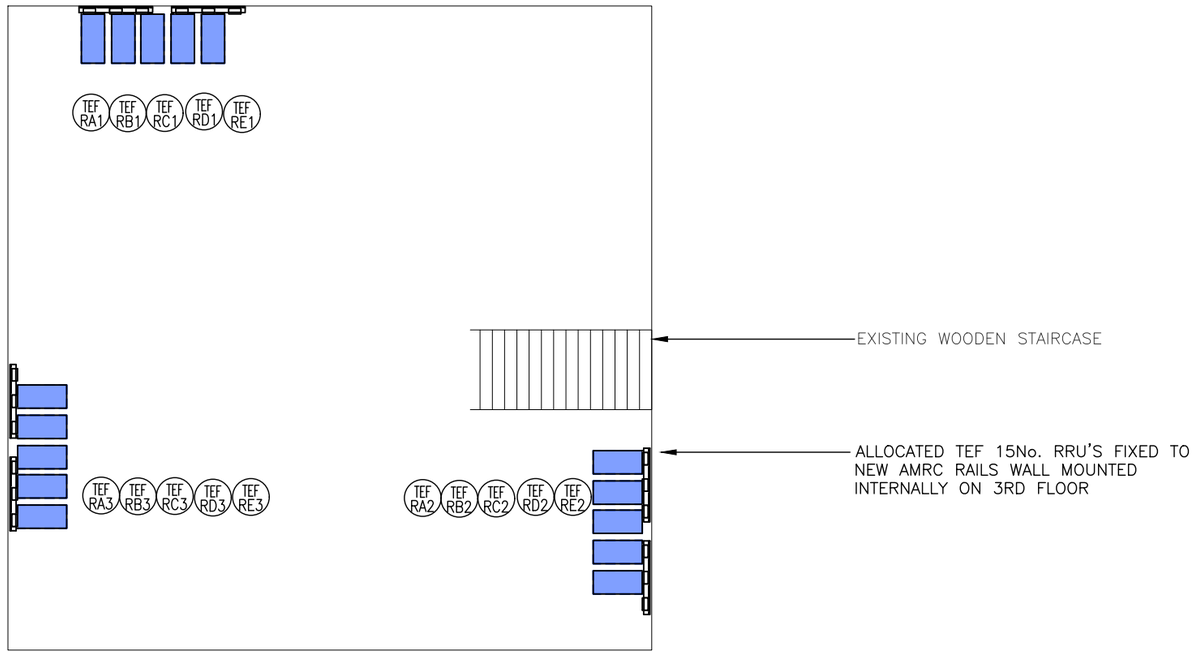

ALLOCATED RRU PLAN @20.70 AGL 3RD FLOOR

(1:50)

ALL DIMENSIONS ARE IN mm UNLESS NOTED OTHERWISE

N.G.R E: 553884 N: 237653

EQUIPMENT COLOUR KEY

EXISTING EQUIPMENT	
TEF EQUIPMENT ALLOCATED	
TEF PROPOSED EQUIPMENT	
NEUTRAL FOOTPRINT	

NOTES:

REV	MODIFICATION	BY	CH	DATE
1A	PLANNING ISSUE	W	RF	21.10.25

circet UK
Unit 27F-G, Hartlebury Trading Estate, Crown Lane, Hartlebury, Worcestershire, DY10 4JD

cornerstone

Cell Name	Opt.
SAFFRON WALDEN TOWER	–

Cell ID No

CSID	– TEF	– VF
111051	8233	75548
Project No.	– TM Cell ID	– N/A
147	–	–

Site Address / Contact Details

FRIENDS OF SCHOOL WATER TOWER MOUNT
PLEASANT ROAD
SAFFRON WALDEN
ESSEX
CB11 4GA

Drawing Title: ALLOCATED RRU PLAN

Purpose of issue:	Dwg Rev:
PLANNING	1A
Drawing Number: 403	
Surveyed By: CIRCET	Original Sheet Size: A3 — Pack Issue:
Drawn: W — Date: 21.10.25 — Checked: RF — Date: 21.10.25	1A



ITEM DESCRIPTION	QUANTITY
EFF1	1


ALL DIMENSIONS ARE IN mm UNLESS NOTED OTHERWISE

N.G.R E: 553884 N: 237653

EQUIPMENT COLOUR KEY

EXISTING EQUIPMENT	
TEF EQUIPMENT ALLOCATED	
TEF PROPOSED EQUIPMENT	
NEUTRAL FOOTPRINT	

NOTES:

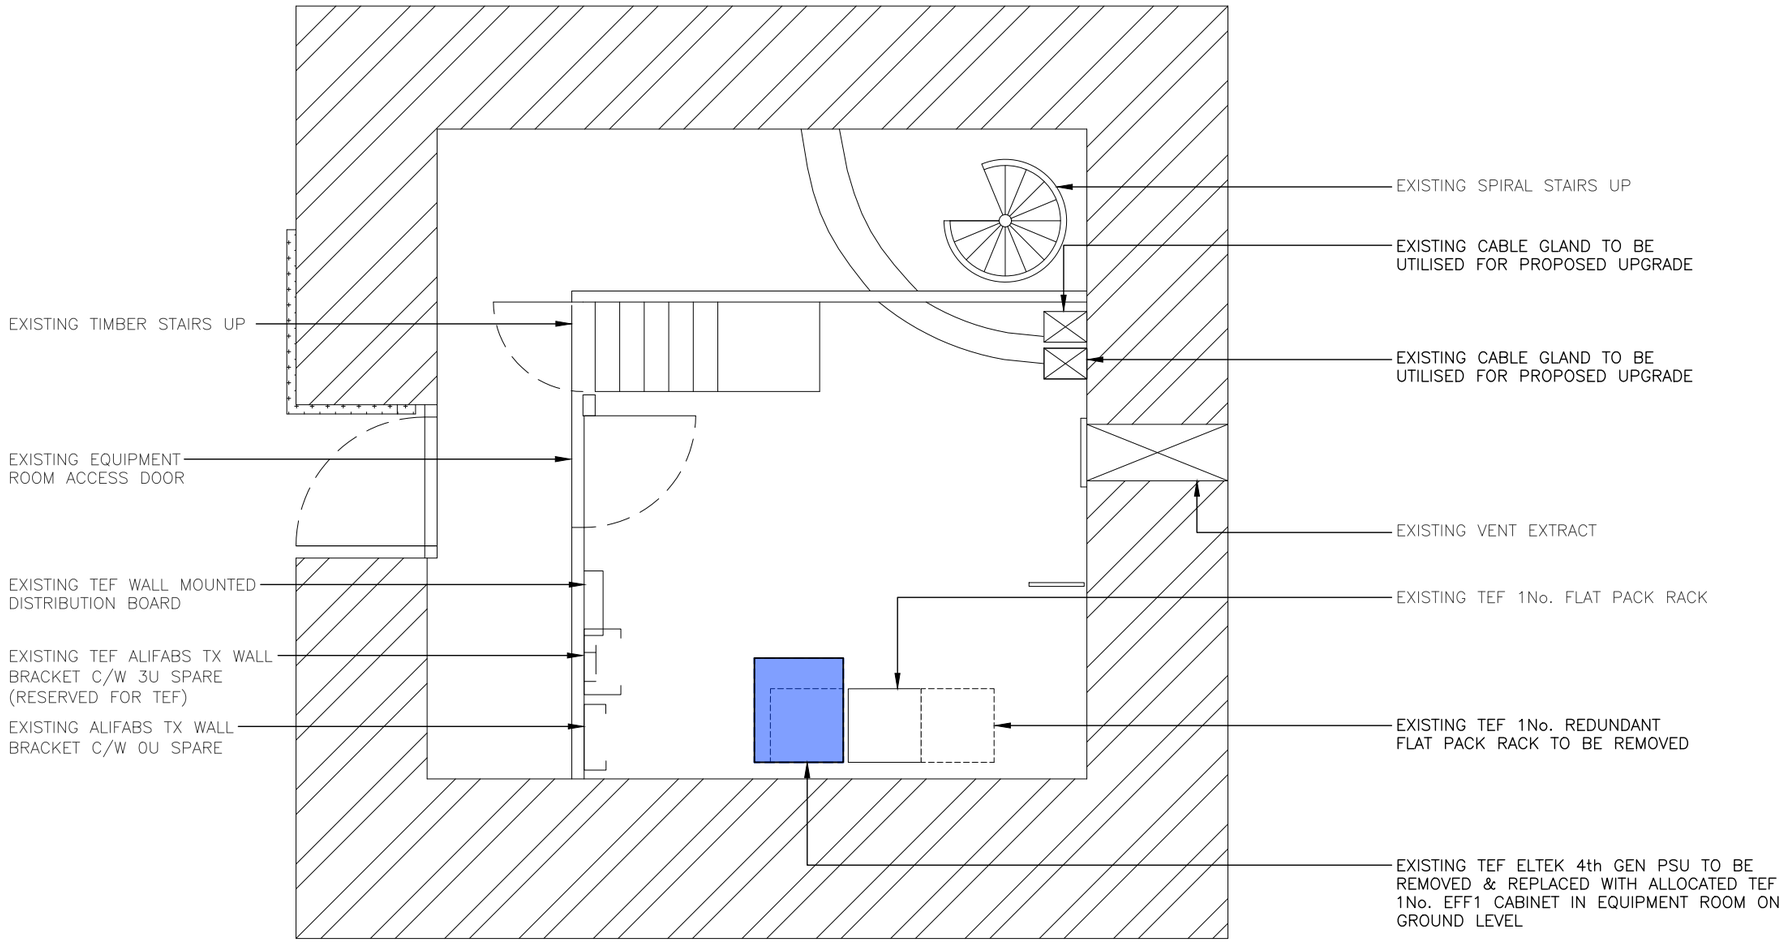

ALLOCATED EQUIPMENT LAYOUT

(1:50)

0 0.5 1 1.5 2 2.5m

1:50

REV	MODIFICATION	BY	CH	DATE
1A	PLANNING ISSUE	W	RF	21.10.25

circet UK
Unit 27F-G, Hartlebury Trading Estate, Crown Lane, Hartlebury, Worcestershire, DY10 4JD

cornerstone

Cell Name	Opt.
SAFFRON WALDEN TOWER	–

Cell ID No


CSID	– TEF	– VF
111051	8233	75548
Project No.	– TM Cell ID	– N/A
147	–	–

Site Address / Contact Details

FRIENDS OF SCHOOL WATER TOWER MOUNT
PLEASANT ROAD
SAFFRON WALDEN
ESSEX
CB11 4GA

Drawing Title: ALLOCATED EQUIPMENT LAYOUT

Purpose of issue:	Dwg Rev:
PLANNING	1A
Drawing Number: 404	
Surveyed By: CIRCET	Original Sheet Size: A3 — Pack Issue: 1A
Drawn: W — Date: 21.10.25	Checked: RF — Date: 21.10.25

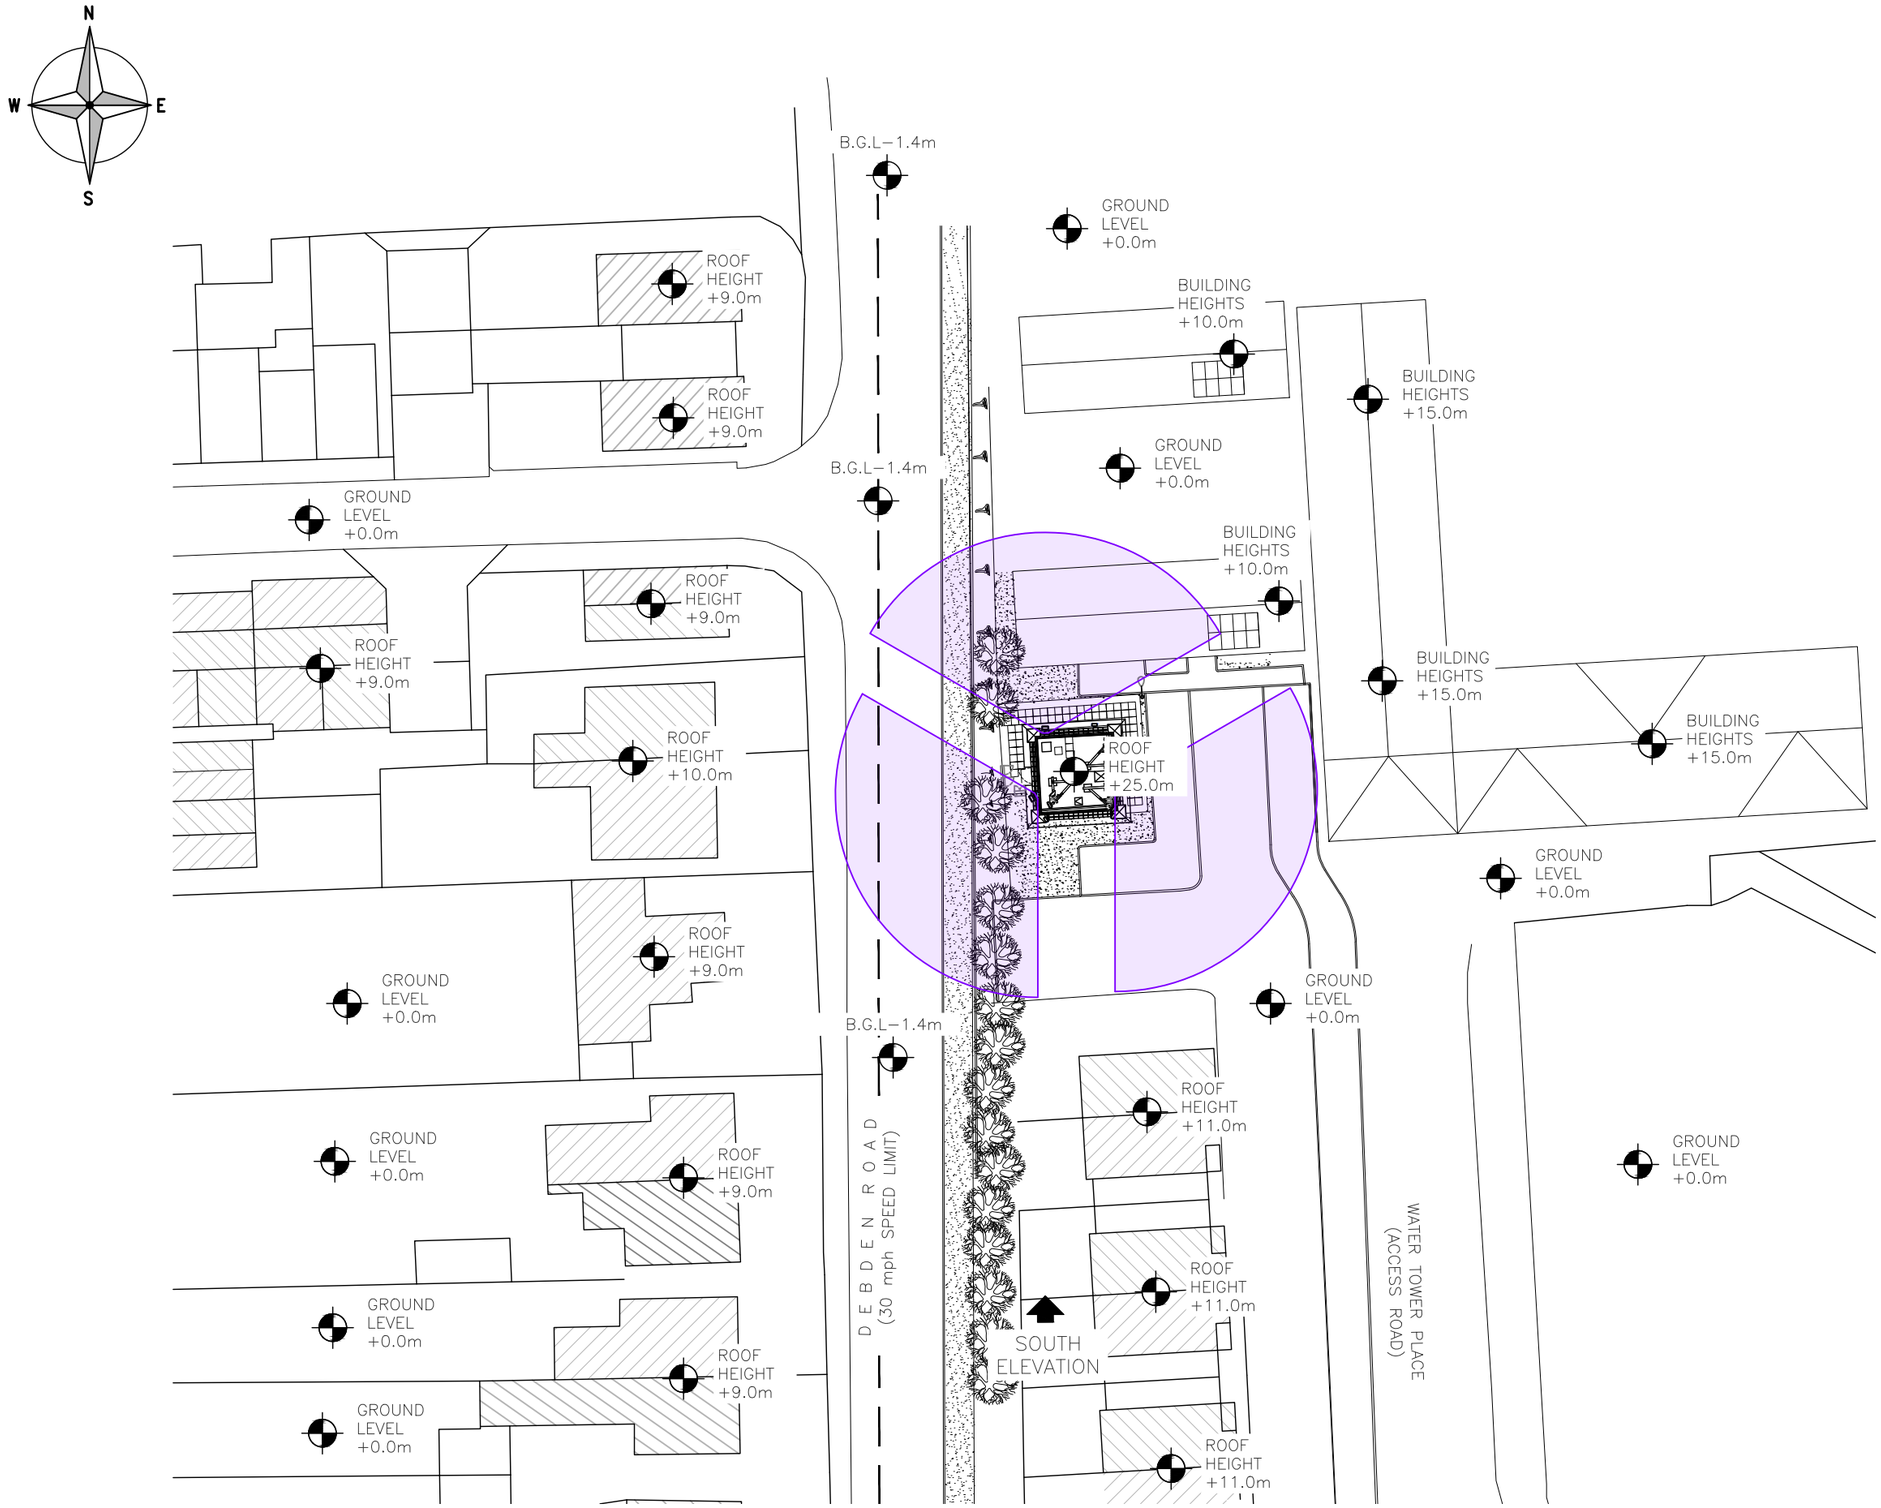

OCCUPATIONAL EXCLUSION ZONE PLAN

(1:250)

0 2.5 5 7.5 10 12.5m

1:250

These drawings comply with TEF Standard ICNIRP guidelines,
Designed in accordance with Cornerstone documents: SDN006; SDN0007 & SDN0008

Notes
Outstanding concession REF 1101 to be made redundant due to design of height increase thus tilt restrictions not required.
Minor Public penetration into NE pitch roof confirmed from EMF as compliant due to slate roof and no skylights present.

ALL DIMENSIONS ARE IN mm UNLESS NOTED OTHERWISE


N.G.R	E: 553884	N: 237653

ICNIRP ZONE INFORMATION

DOCUMENT REF.	SDN0006	v2.0
ICNIRP DOCUMENT SECTION	8.15 ID 15	
ICNIRP CONFIG CAPACITY	HIGH+	
ICNIRP CONFIG ID	ID15 STEP 0	
EMF CODE	15–VM–V4.8–GR–BM–F–0	
MORAN + OLO	SECTOR(S)	ALL

OCCUPATIONAL ICNIRP ZONE

OCCUPATIONAL EXCL. ZONE (A)	16.50m
OCCUPATIONAL BUILD HGT. (B)	4.03m

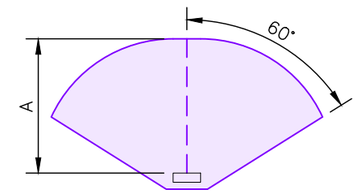

REV	MODIFICATION	BY	CH	DATE
1A	PLANNING ISSUE	W	RF	21.10.25

circet UK
Unit 27F-G, Hartlebury Trading Estate, Crown Lane, Hartlebury, Worcestershire, DY10 4JD

cornerstone

Cell Name	Opt.
SAFFRON WALDEN TOWER	–

Cell ID No


CSID	– TEF	– VF
111051	8233	75548
Project No.	– TM Cell ID	– N/A
147	–	–

Site Address / Contact Details

FRIENDS OF SCHOOL WATER TOWER MOUNT
PLEASANT ROAD
SAFFRON WALDEN
ESSEX
CB11 4GA

Drawing Title:
OCCUPATIONAL ICNIRP PLAN

Purpose of issue:	Dwg Rev:
PLANNING	1A
Drawing Number: 450	
Surveyed By: CIRCET	Original Sheet Size: A3 / Pack Issue:
Drawn: W / Date: 21.10.25	Checked: RF / Date: 21.10.25 / 1A

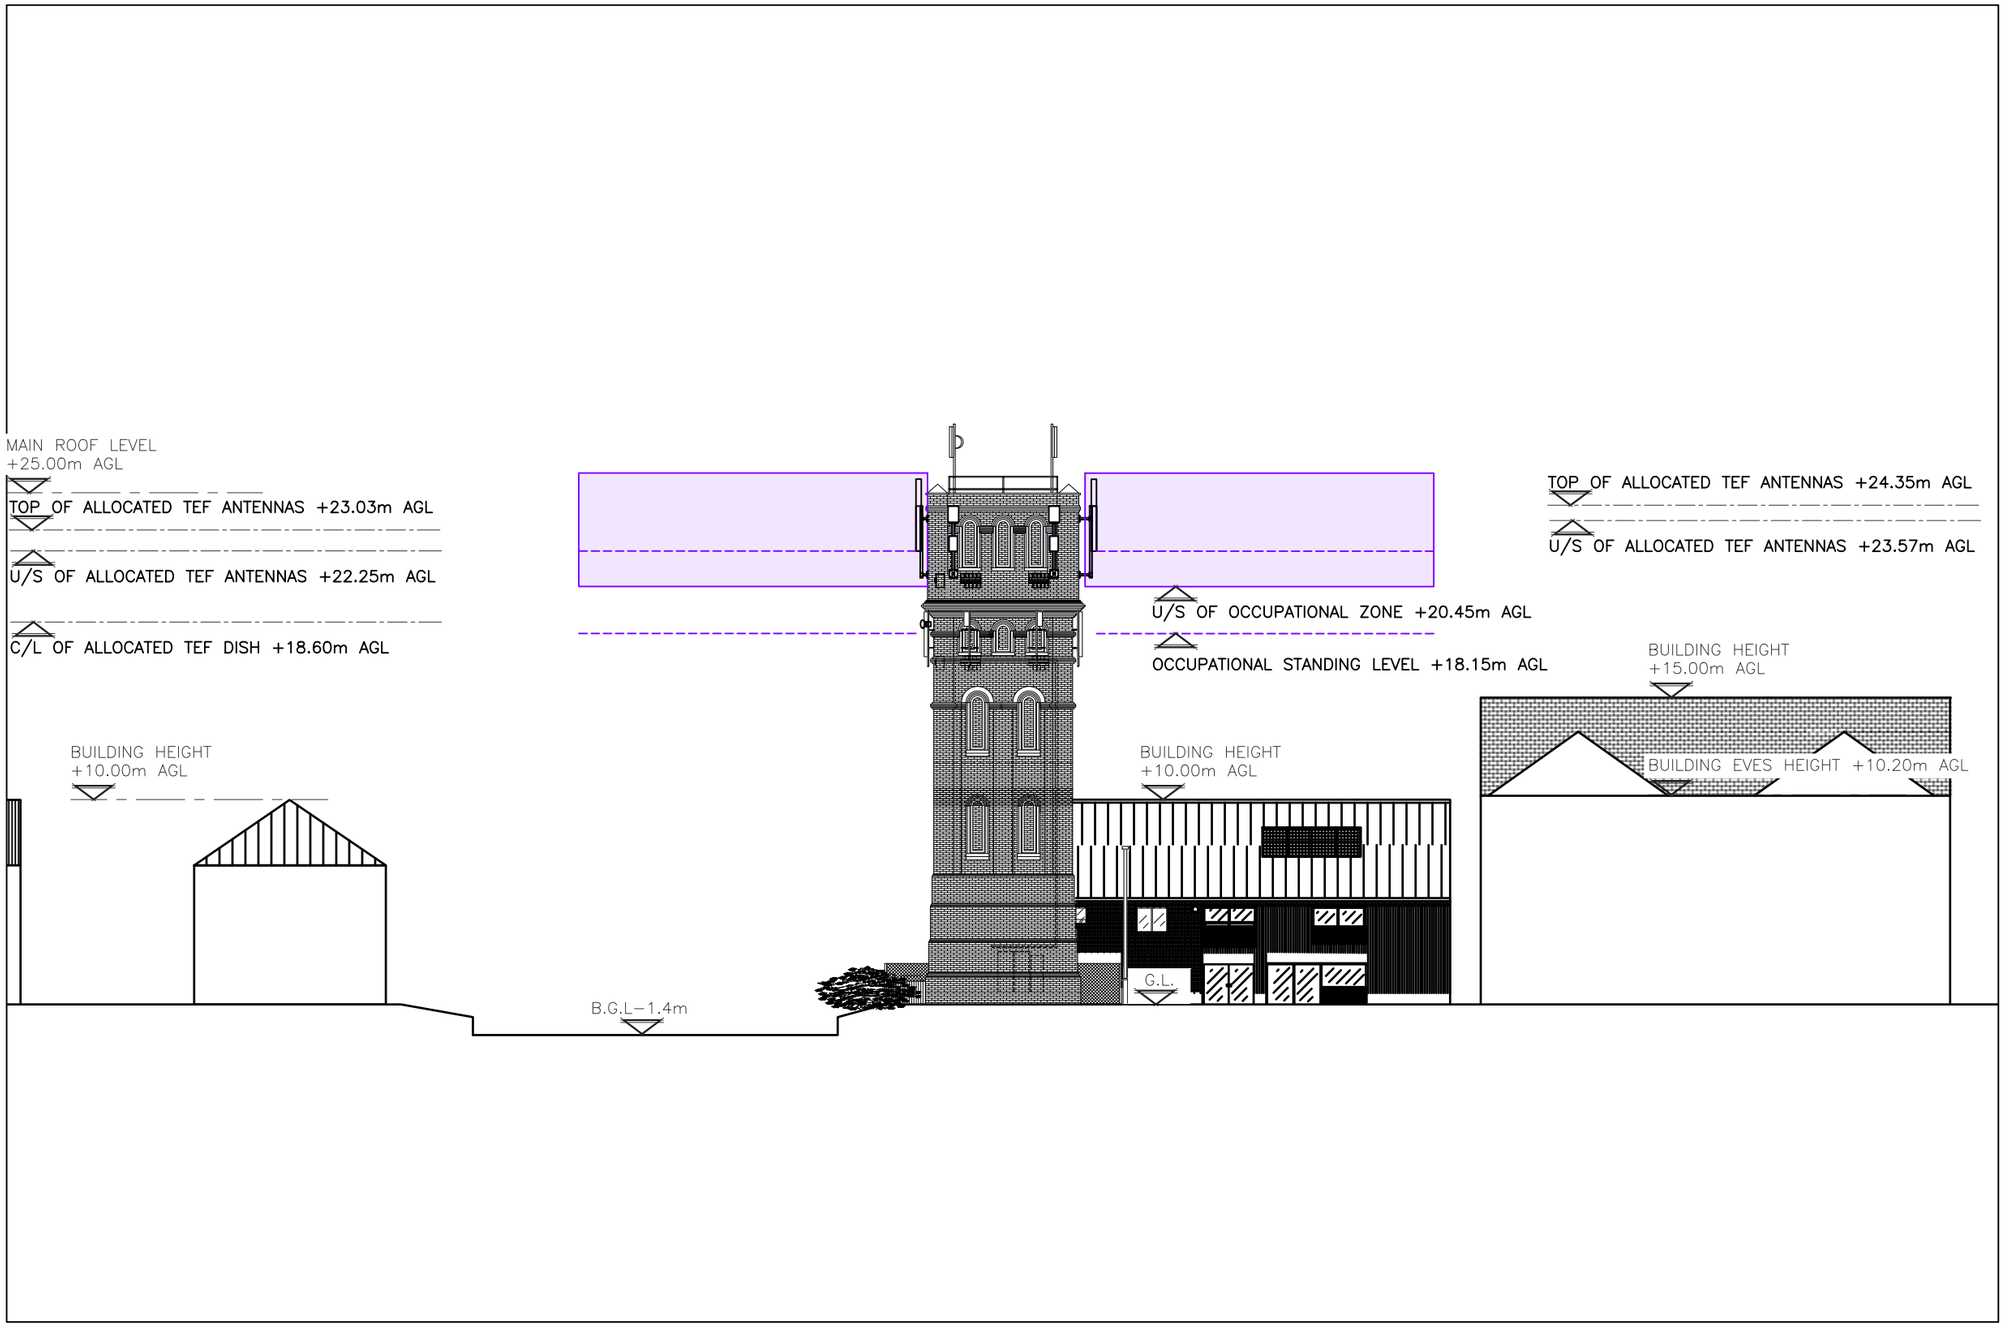

OCCUPATIONAL EXCLUSION ZONE ELEVATION (SOUTH ELEVATION)

(1:300)

0 2.5 5 7.5 10 12.5m
1:250

These drawings comply with TEF Standard ICNIRP guidelines,
Designed in accordance with Cornerstone documents: SDN006; SDN0007 & SDN0008

Notes
Outstanding concession REF 1101 to be made redundant due to design of height increase thus tilt restrictions not required.
Minor Public penetration into NE pitch roof confirmed from EMF as compliant due to slate roof and no skylights present.

ALL DIMENSIONS ARE IN mm UNLESS NOTED OTHERWISE


N.G.R	E: 553884	N: 237653

ICNIRP ZONE INFORMATION

DOCUMENT REF.	SDN0006	v2.0
ICNIRP DOCUMENT SECTION	8.15 ID 15	
ICNIRP CONFIG CAPACITY	HIGH+	
ICNIRP CONFIG ID	ID15 STEP 0	
EMF CODE	15-VM-V4.8-GR-BM-F-0	
MORAN + OLO	SECTOR(S)	ALL

OCCUPATIONAL ICNIRP ZONE

OCCUPATIONAL EXCL. ZONE (A)	16.50m
OCCUPATIONAL BUILD HGT. (B)	4.03m

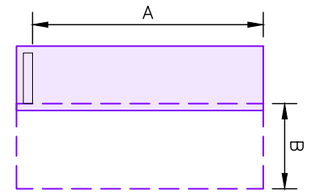

REV	MODIFICATION	BY	CH	DATE
1A	PLANNING ISSUE	W	RF	21.10.25

circet UK
Unit 27F-G, Hartlebury Trading Estate, Crown Lane, Hartlebury, Worcestershire, DY10 4JD

cornerstone

Cell Name	Opt.
SAFFRON WALDEN TOWER	–

Cell ID No

CSID	– TEF	– VF
111051	8233	75548
Project No.	– TM Cell ID	– N/A
147	–	–

Site Address / Contact Details

FRIENDS OF SCHOOL WATER TOWER MOUNT
PLEASANT ROAD
SAFFRON WALDEN
ESSEX
CB11 4GA


Drawing Title:
OCCUPATIONAL ICNIRP ELEVATION

Purpose of issue:	Dwg Rev:
PLANNING	
Drawing Number: 451	1A

Surveyed By:	Original Sheet Size:	Pack Issue:
CIRCET	A3	

Drawn:	Date:	Checked:	Date:	
W	21.10.25	RF	21.10.25	1A

FOR INTERNAL USE ONLY
DO NOT ISSUE EXTERNALLY UNDER ANY CIRCUMSTANCES

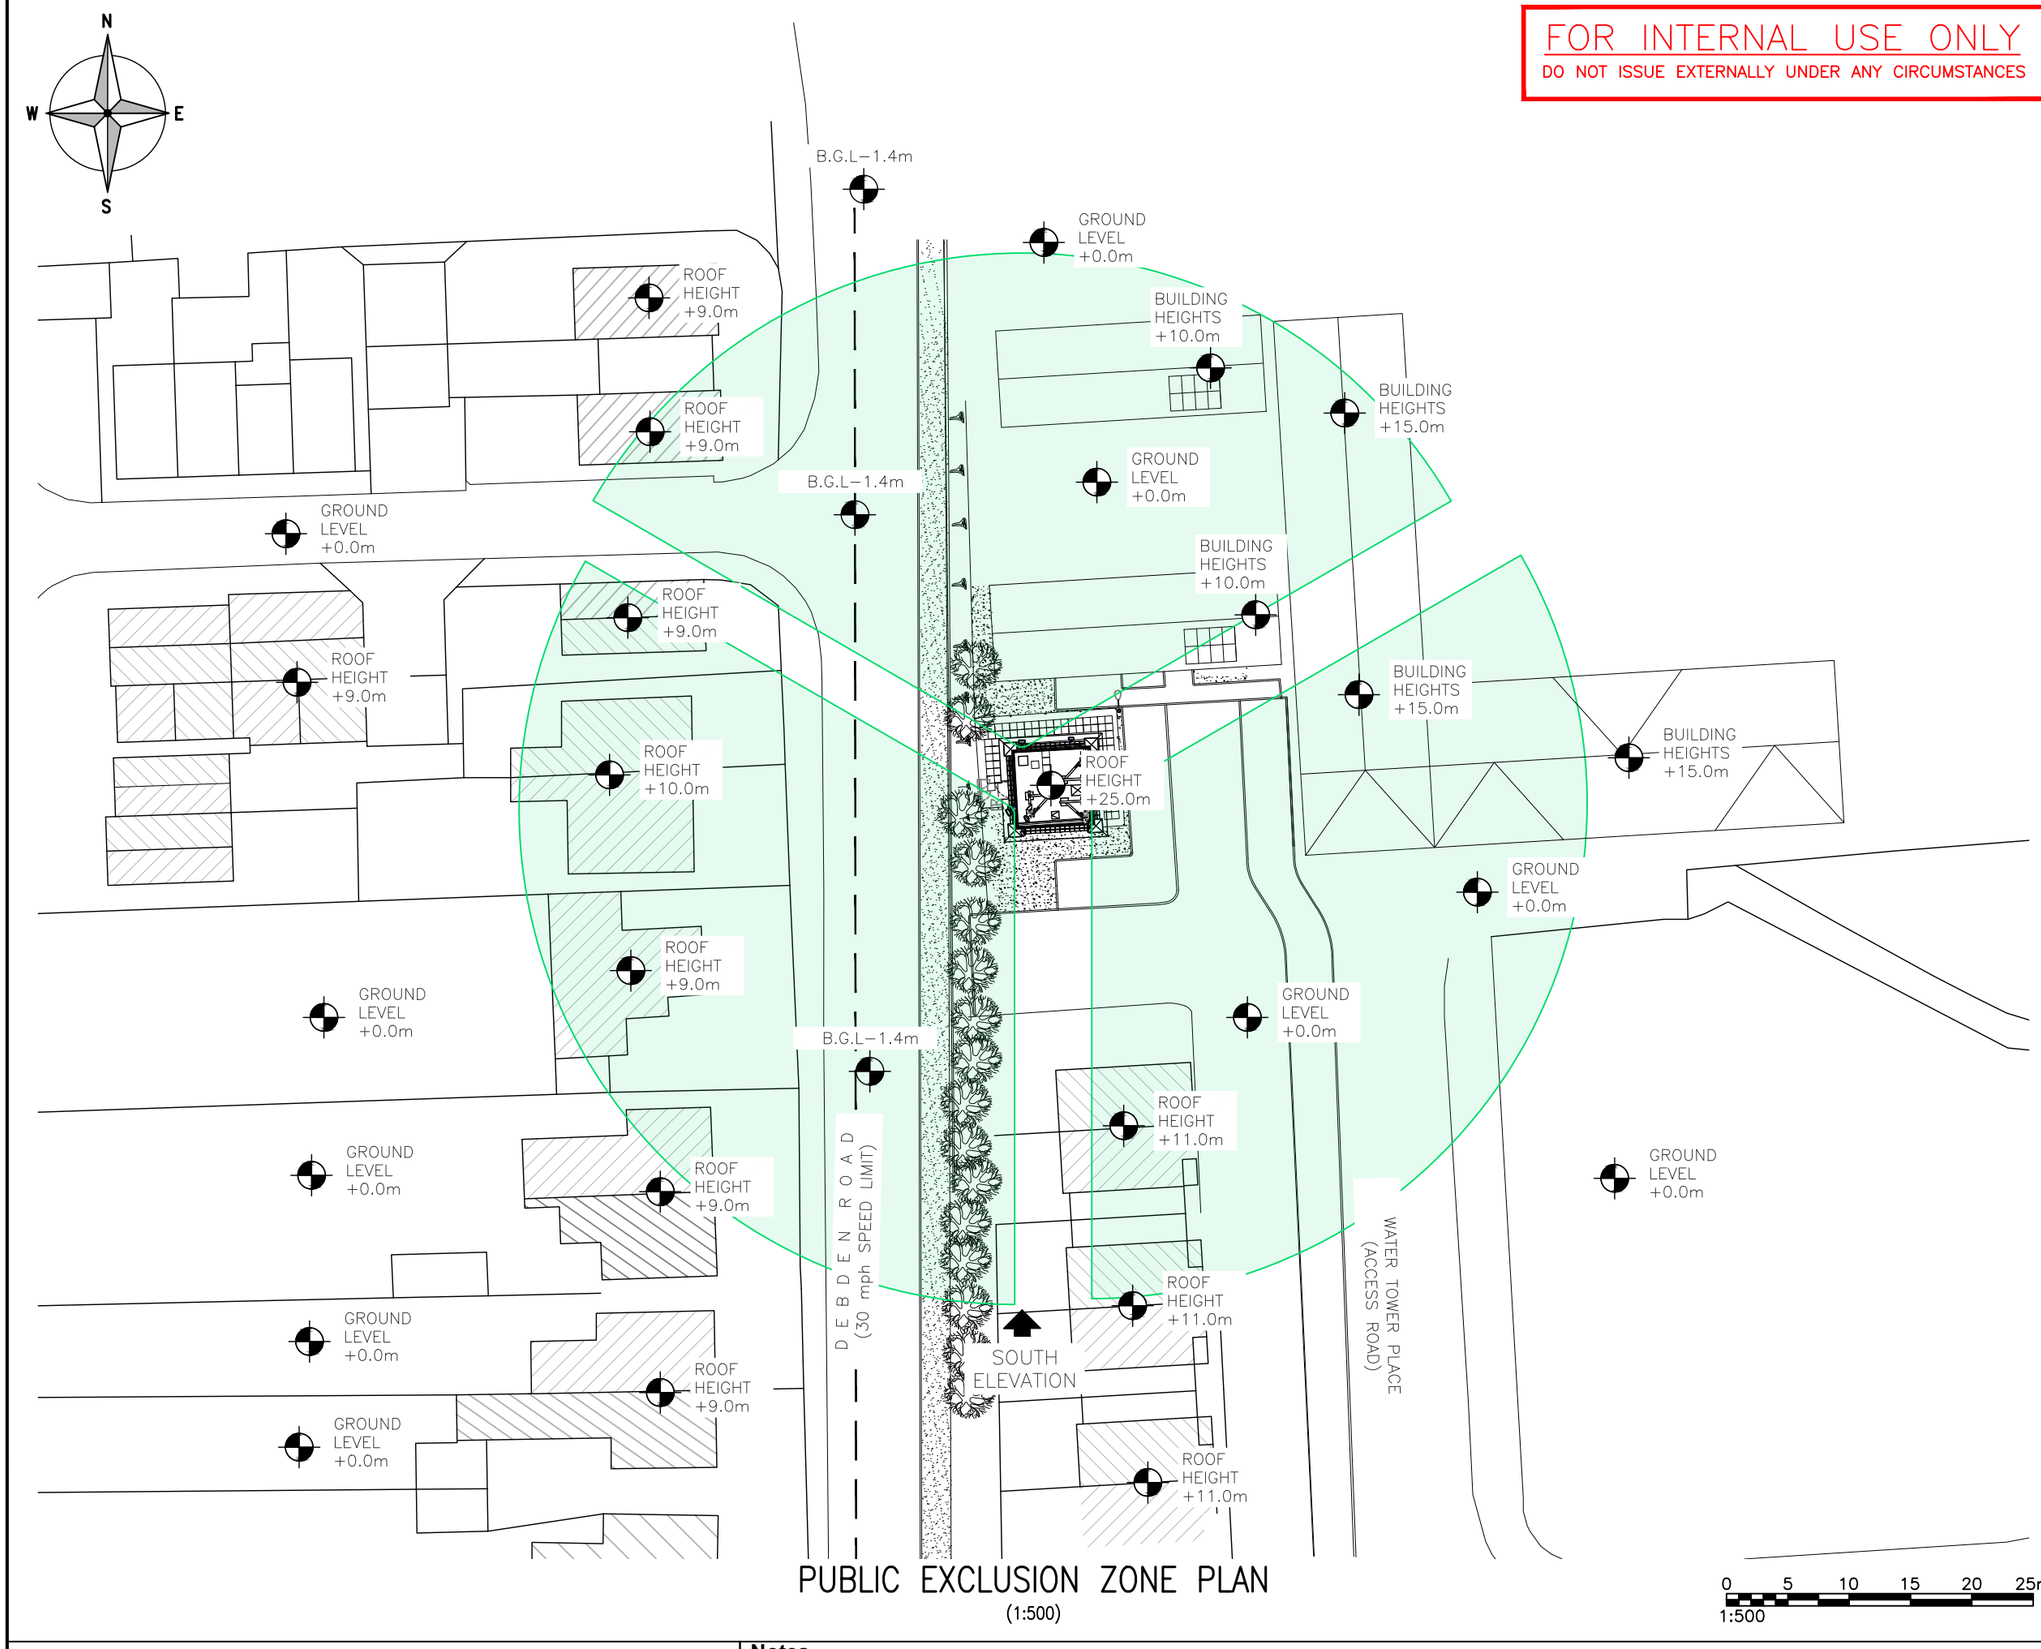

PUBLIC EXCLUSION ZONE PLAN
(1:500)

These drawings comply with TEF Standard ICNIRP guidelines,
Designed in accordance with Cornerstone documents: SDN006; SDN0007 & SDN0008


Notes
Outstanding concession REF 1101 to be made redundant due to design of height increase thus tilt restrictions not required.
Minor Public penetration into NE pitch roof confirmed from EMF as compliant due to slate roof and no skylights present.

ALL DIMENSIONS ARE IN mm UNLESS NOTED OTHERWISE

N.G.R	E: 553884	N: 237653

ICNIRP ZONE INFORMATION

DOCUMENT REF.	SDN0006	v2.0
ICNIRP DOCUMENT SECTION	8.15 ID 15	
ICNIRP CONFIG CAPACITY	HIGH+	
ICNIRP CONFIG ID	ID15 STEP 0	
EMF CODE	15–VM–V4.8–GR–BM–F–0	
MORAN + OLO	SECTOR(S)	ALL
PUBLIC ICNIRP ZONE		
PUBLIC EXCL. ZONE (C)		40.40m
PUBLIC BUILD HGT. (D)		11.13m
ANGLE (∠)		18°

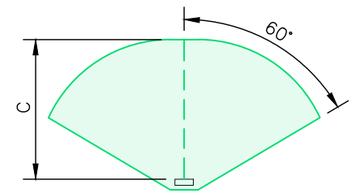

REV	MODIFICATION	BY	CH	DATE
1A	PLANNING ISSUE	W	RF	21.10.25

circet UK
Unit 27F-G, Hartlebury Trading Estate, Crown Lane, Hartlebury, Worcestershire, DY10 4JD

cornerstone

Cell Name	Opt.
SAFFRON WALDEN TOWER	–

Cell ID No

CSID	– TEF	– VF
111051	8233	75548
Project No.	– TM Cell ID	– N/A
147	–	–

Site Address / Contact Details

FRIENDS OF SCHOOL WATER TOWER MOUNT
PLEASANT ROAD
SAFFRON WALDEN
ESSEX
CB11 4GA


Drawing Title:
PUBLIC ICNIRP PLAN

Purpose of issue:	Dwg Rev:
PLANNING	1A
Drawing Number: 452	

Surveyed By:	Original Sheet Size:	Pack Issue:
CIRCET	A3	

Drawn:	Date:	Checked:	Date:	
W	21.10.25	RF	21.10.25	1A

FOR INTERNAL USE ONLY
DO NOT ISSUE EXTERNALLY UNDER ANY CIRCUMSTANCES

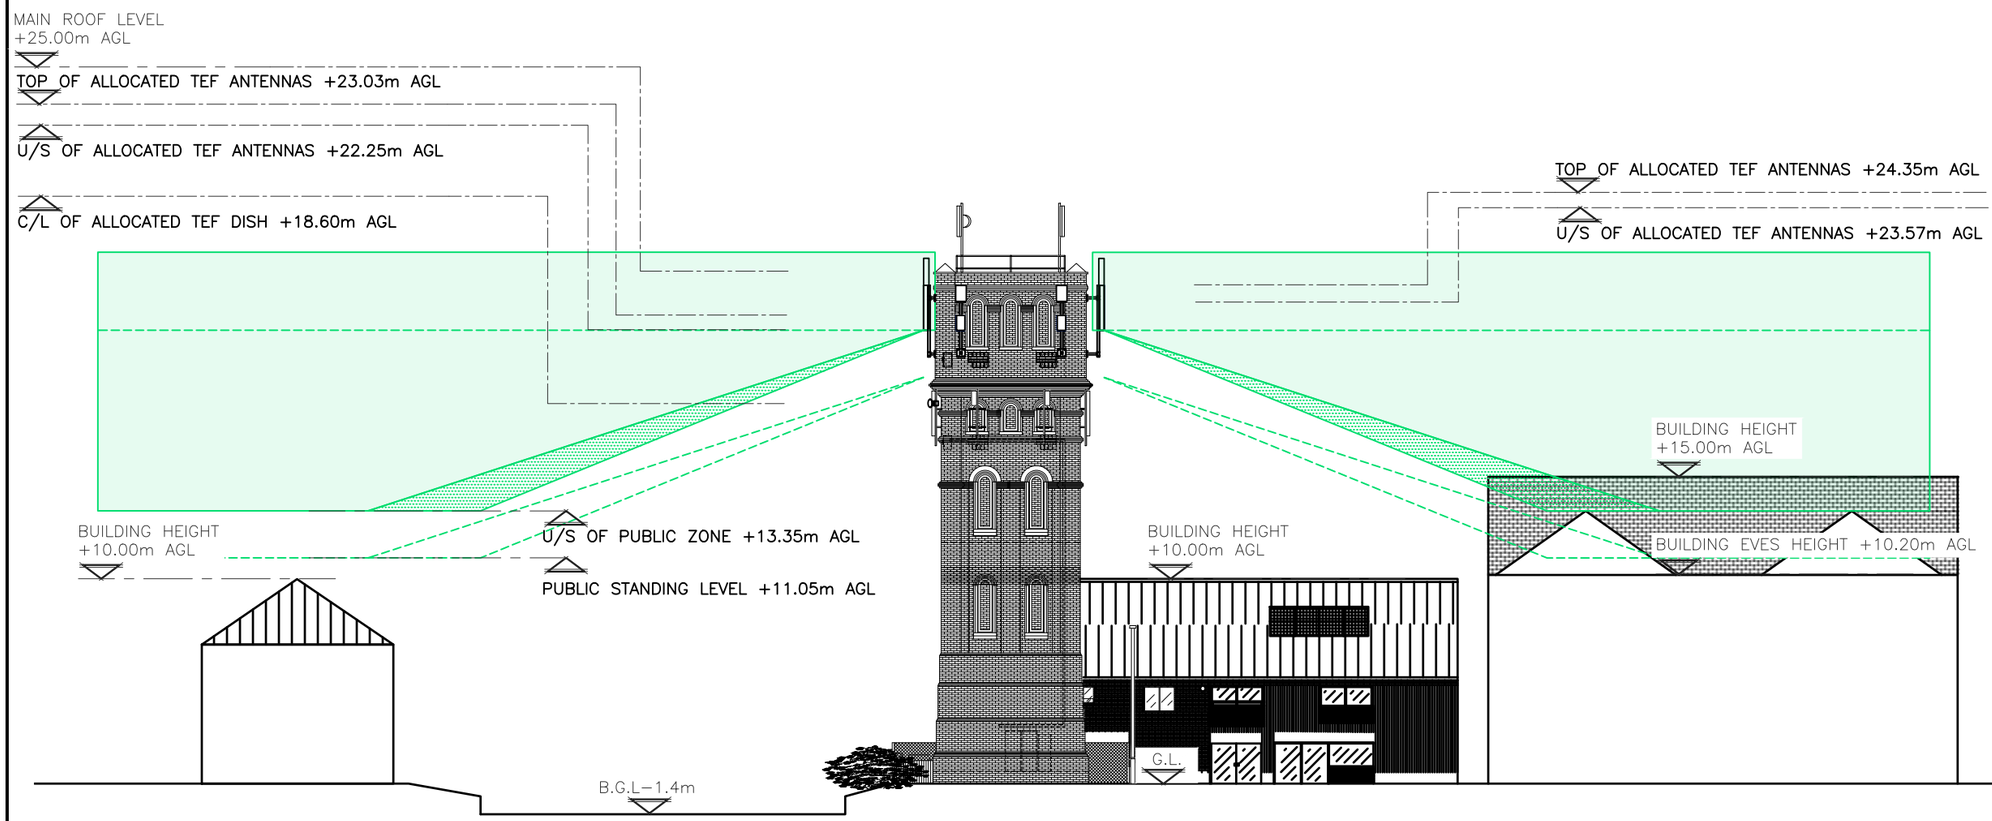

PUBLIC EXCLUSION ZONE ELEVATION
(1:300)

0 5 10 15 20 25m
1:500

These drawings comply with TEF Standard ICNIRP guidelines,
Designed in accordance with Cornerstone documents: SDN006; SDN0007 & SDN0008

Notes
Outstanding concession REF 1101 to be made redundant due to design of height increase thus tilt restrictions not required.
Minor Public penetration into NE pitch roof confirmed from EMF as compliant due to slate roof and no skylights present.

ALL DIMENSIONS ARE IN mm UNLESS NOTED OTHERWISE


N.G.R	E: 553884	N: 237653

ICNIRP ZONE INFORMATION

DOCUMENT REF.	SDN0006	v2.0
ICNIRP DOCUMENT SECTION	8.15 ID 15	
ICNIRP CONFIG CAPACITY	HIGH+	
ICNIRP CONFIG ID	ID15 STEP 0	
EMF CODE	15–VM–V4.8–GR–BM–F–0	
MORAN + OLO	SECTOR(S)	ALL

PUBLIC ICNIRP ZONE

PUBLIC EXCL. ZONE (C)	40.40m
PUBLIC BUILD HGT. (D)	11.13m
ANGLE (∠)	18°

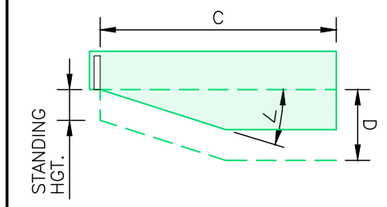

REV	MODIFICATION	BY	CH	DATE
1A	PLANNING ISSUE	W	RF	21.10.25

circet UK
Unit 27F-G, Hartlebury Trading Estate, Crown Lane, Hartlebury, Worcestershire, DY10 4JD

cornerstone

Cell Name	Opt.
SAFFRON WALDEN TOWER	–

Cell ID No

CSID	– TEF	– VF
111051	8233	75548
Project No.	– TM Cell ID	– N/A
147	–	–

Site Address / Contact Details

FRIENDS OF SCHOOL WATER TOWER MOUNT
PLEASANT ROAD
SAFFRON WALDEN
ESSEX
CB11 4GA

Drawing Title:
PUBLIC ICNIRP ELEVATION

Purpose of issue:	Dwg Rev:
PLANNING	1A
Drawing Number: 453	

Surveyed By:	Original Sheet Size:	Pack Issue:
CIRCET	A3	1A

Drawn:	Date:	Checked:	Date:
W	21.10.25	RF	21.10.25

EXISTING ANTENNA SCHEDULE

R.F. CONFIG CODE:	SECTOR 1 BEARING (DEG)						SECTOR 2 BEARING (DEG)						SECTOR 3 BEARING (DEG)						SECTOR 4 BEARING (DEG)					
N3–L–M–A	EA1	0°	EB1	0°	–	–	EA2	120°	EB2	120°	–	–	EA3	240°	EB3	240°	–	–	–	–	–	–	–	–

ANTENNA DETAILS	SECTOR (SELECT ALL THAT APPLY)	SECTOR 1/2/3		
	ANTENNA REFERENCE	EA	EB	–
	ANTENNA CENTER (m)	17.74	18.10	–
	STATUS	REMOVE	REMOVE	–

EXISTING ANTENNA SCHEMATIC

SUA–7 ANTENNA

MIMO
AQQC

C2 08/09

C2 07/09

L08/L09
AHPMDA
(4x4)
RRU

N07/GU09
AHPMDA
(4x4)
RRU

L18/L21
AHEGB
(4x4)
RRU

L23
AKNA
(8x8)
RRU

RRU ABOVE THIS LINE REMOTE

RRU BELOW THIS LINE LOCAL

ALL DIMENSIONS ARE IN mm UNLESS NOTED OTHERWISE

N.G.R E: 553884 N: 237653

EQUIPMENT COLOUR KEY

EXISTING EQUIPMENT	
TEF EQUIPMENT ALLOCATED	
TEF PROPOSED EQUIPMENT	
NEUTRAL FOOTPRINT	

NOTES:

REV	MODIFICATION	BY	CH	DATE
1A	PLANNING ISSUE	W	RF	21.10.25

circet UK
Unit 27F-G, Hartlebury Trading Estate, Crown Lane, Hartlebury, Worcestershire, DY10 4JD

cornerstone

Cell Name	Opt.
SAFFRON WALDEN TOWER	–

Cell ID No

CSID	– TEF	– VF
111051	8233	75548
Project No.	– TM Cell ID	– N/A
147	–	–

Site Address / Contact Details

FRIENDS OF SCHOOL WATER TOWER MOUNT
PLEASANT ROAD
SAFFRON WALDEN
ESSEX
CB11 4GA

Drawing Title: EXISTING TEF R.F. SYSTEM

Purpose of issue:	Dwg Rev:
PLANNING	1A
Drawing Number: 500	

Surveyed By:	Original Sheet Size:	Pack Issue:
CIRCET	A3	1A

Drawn:	Date:	Checked:	Date:
W	21.10.25	RF	21.10.25

ALLOCATED SCHEMATIC – DOC REF: UKDBS_BAU_0705_ALL REGIONS V4.0

AFF3

AFF6

AFF1

RFF1 RFF1 RFF1 RFF1 RFF2

RRU ABOVE THIS LINE REMOTE

RRU BELOW THIS LINE LOCAL

DESIGN CODES

The Actual Code reflects the positions in which each operator has reserved the right to install equipment as shown in the Allocated schematic

ACTUAL: 03H(5+0)v4

Allocated = Operator acquired rights, Position reserved for future equipment

ALL DIMENSIONS ARE IN mm UNLESS NOTED OTHERWISE

N.G.R E: 553884 N: 237653

EQUIPMENT COLOUR KEY

EXISTING EQUIPMENT	
TEF EQUIPMENT ALLOCATED	
TEF PROPOSED EQUIPMENT	
NEUTRAL FOOTPRINT	

NOTES:

REV	MODIFICATION	BY	CH	DATE
1A	PLANNING ISSUE	W	RF	21.10.25

circet UK
Unit 27F-G, Hartlebury Trading Estate, Crown Lane, Hartlebury, Worcestershire, DY10 4JD

cornerstone

Cell Name	Opt.
SAFFRON WALDEN TOWER	–

Cell ID No

CSID	– TEF	– VF
111051	8233	75548
Project No.	– TM Cell ID	– N/A
147	–	–

Site Address / Contact Details

FRIENDS OF SCHOOL WATER TOWER MOUNT
PLEASANT ROAD
SAFFRON WALDEN
ESSEX
CB11 4GA

Drawing Title:
ALLOCATED TEF R.F. SYSTEM SCHEMATIC

Purpose of issue:	Dwg Rev:
PLANNING	1A
Drawing Number: 550	

Surveyed By:	Original Sheet Size:	Pack Issue:
CIRCET	A3	1A

Drawn:	Date:	Checked:	Date:
W	21.10.25	RF	21.10.25

ALLOCATED SCHEDULE – DOC REF: UKDBS_BAU_0705_ALL REGIONS v4.0

R.F. CONFIG CODE:	SECTOR 1 BEARING (DEG)						SECTOR 2 BEARING (DEG)						SECTOR 3 BEARING (DEG)						SECTOR 4 BEARING (DEG)					
O3H(5+0)v4	TA1	0°	TB1	0°	TC1	0°	TA2	120°	TB2	120°	TC2	120°	TA3	240°	TB3	240°	TC3	240°						

ANTENNA DETAILS	SECTOR (SELECT ALL THAT APPLY)	SECTOR 1/2/3		
	ANTENNA REFERENCE	TA	TB	TC
	ANTENNA CENTER (m)	23.25m	23.96m	22.64m
	STATUS	ALLOCATED	ALLOCATED	ALLOCATED

ALL DIMENSIONS ARE IN mm UNLESS NOTED OTHERWISE

N.G.R E: 553884 N: 237653

EQUIPMENT COLOUR KEY

EXISTING EQUIPMENT	
TEF EQUIPMENT ALLOCATED	
TEF PROPOSED EQUIPMENT	
NEUTRAL FOOTPRINT	

NOTES:

REV	MODIFICATION	BY	CH	DATE
1A	PLANNING ISSUE	VW	RF	21.10.25

circet UK

Unit 27F-G, Hartlebury Trading Estate, Crown Lane, Hartlebury, Worcestershire, DY10 4JD

cornerstone

Cell Name	Opt.
SAFFRON WALDEN TOWER	–

Cell ID No

CSID	– TEF	– VF
111051	8233	75548
Project No.	– TM Cell ID	– N/A
147	–	–

Site Address / Contact Details

FRIENDS OF SCHOOL WATER TOWER MOUNT
PLEASANT ROAD
SAFFRON WALDEN
ESSEX
CB11 4GA

Drawing Title:
ALLOCATED TEF ANTENNA SCHEDULE

Purpose of issue:	Dwg Rev:
PLANNING	1A
Drawing Number: 551	

Surveyed By:	Original Sheet Size:	Pack Issue:
CIRCET	A3	1A

Drawn:	Date:	Checked:	Date:
VW	21.10.25	RF	21.10.25

SUPPORT STRUCTURE SCHEDULE

EXISTING/ PROPOSED	OWNER	MANUFACTURER	MODEL	STRUCTURE HEIGHT	FOUNDATION TYPE (ROOT/PAD/GRILLAGE)	FOUNDATION DIMENSIONS (WxDxH)	COLOUR/ FINISH	STATUS	COMMENTS
EXISTING	TEF	BESPOKE	WALL MOUNTED SUPPORT POLE	18.00m	–	–	GALVANISED	REMAIN	–
PROPOSED	TEF	BESPOKE	CHS 3500x114	22.80m	WALL	–	GALVANISED	NEW	6No. REQUIRED TRHOUGH BOLTED
PROPOSED	TEF	BESPOKE	THROUGH BOLT WALL PLATE	22.80m	CHS	–	GALVANISED	NEW	12No. REQUIRED (2No. PER POLE)
PROPOSED	TEF	BESPOKE	CHS WALL PLATE STUB 500x114	22.80m	WALL PLATE	–	GALVANISED	NEW	6No. REQUIRED (2No. PER POLE)
PROPOSED	TEF	BESPOKE	CHS WALL PLATE STUB 250x114	22.80m	WALL PLATE	–	GALVANISED	NEW	6No. REQUIRED (2No. PER POLE)
PROPOSED	TEF	NOKIA	AMRC RAIL	22.80m	WALL (INTERNAL)	–	GALVANISED	NEW	6No. REQUIRED – WALL MOUNTED

ENCLOSURE SCHEDULE

EXISTING/ PROPOSED	OPERATOR	MANUFACTURER	MODEL	DIMENSIONS (WxDxH)	LOCATION	COLOUR/ FINISH	STATUS	COMMENTS
EXISTING	TEF	MALCOE	METER CABINET	1000x450x1200	GROUND LEVEL	GREEN	REMAIN	–
EXISTING	TEF	COMMSCOPE	FLAT PACK RACK	600x630x1500	EQUIPMENT ROOM	GREY	REMAIN	–
EXISTING	TEF	COMMSCOPE	FLAT PACK RACK (REDUNDANT)	600x630x1500	EQUIPMENT ROOM	GREY	REMAIN	–
EXISTING	TEF	ELTEK	4th GEN INDOOR	600x750x1800	EQUIPMENT ROOM	GREY	REMOVE	1No. TO BE REMOVED
ALLOCATED	TEF	–	EFF1	725x850x2100	EQUIPMENT ROOM	GREY	NEW	1No. REQUIRED

AC POWER SUPPLY SCHEDULE

EXISTING/ PROPOSED	OPERATOR	LOCATION	SUPPLY TYPE (LL/DNO/LOCAL THIRD PARTY)	PHASE (SINGLE/THREE/TWO)	SOURCE OCPD RATING (A)	EARTHING SYSTEM TYPE (TN-C-S/TT)	2nd SUPPLY TO BUILDING (Y/N)	LPS (ADDITION/NEW)	COMMENTS
EXISTING	TEF	GROUND LEVEL	DNO	THREE	100A	TN-C-S	N	–	–

DC POWER SUPPLY UNIT SCHEDULE

EXISTING/ PROPOSED	OPERATOR	MANUFACTURER	MODEL	LOCATION	AC SUPPLY TO PSU BREAKER SIZE (AMPS)	RECTIFIER SIZE (kW)	RECTIFIER QUANTITY	UPGRADE REQUIRED (Y/N)	COMMENTS
EXISTING	TEF	ELTEK	4TH GEN	CABIN	3xC40	3kW	4	N	CABINET TO BE REMOVED
EXISTING	TEF	ERICSSON	PSU 4813	ELTEK	1xC125	5.6kW	1	–	CABINET TO BE REMOVED
EXISTING	TEF	GCA	7WAY BOB	INTERNAL	–	–	–	–	TO BE REMOVED
ALLOCATED	TEF	ELTEK	EFF1	EQUIPMENT ROOM	TBC	TBC	TBC	N/A	–

TRANSMISSION SUPPLY SCHEDULE

EXISTING/ PROPOSED (ENCLOSURE)	OPERATOR		TRANSMISSION ENCLOSURE	TRANSMISSION SOLUTION (MICROWAVE ONLY/FIBRE ONLY/ MICROWAVE+FIBRE (WITH PROVIDER NAME))	U SPACE AVAILABLE	CURRENT TRANSMISSION EQUIPMENT LOCATION	PROPOSED TRANSMISSION EQUIPMENT LOCATION	COMMENTS
	HOST	SHARER						
EXISTING	TEF	–	ALIFABS WALL BRACKET	BT FIBRE	0U	–	–	TO REMAIN
EXISTING	TEF	–	ALIFABS WALL BRACKET	FIBRE & MICROWAVE	2U	X	–	TO REMAIN
ALLOCATED	TEF	–	EFF1	FIBRE & MICROWAVE	2U	–	EFF1	TO BE INSTALLED

COOLING SCHEDULE

EXISTING/ PROPOSED	COOLING TYPE	COOLING MAKE/MODEL	QUANTITY	COOLING CAPACITY (kW)	SITE HEAT LOAD (kW)	COOLING CALCULATOR VERSION	COOLING SYSTEM STATUS
EXISTING	FREE AIR	VENT AXIA T-SERIES	1	12kW	–	–	REMAIN

ALLOCATED RF EQUIPMENT SCHEDULE

STATUS	OPERATOR	ALLOCATED POSITION REF	DESIGN REFERENCE	DIMENSIONS (WxDxH)	WEIGHT (kg)	LOCATION	HEIGHT (C/L)	QUANTITY
ALLOCATED	TEF	A1,2,3	AFF3	500x230x2200	55	SUPPORT POLE	23.25m	3
ALLOCATED	TEF	B1,2,3	AFF6	410x190x730	40	SUPPORT POLE	23.96m	3
ALLOCATED	TEF	C1,2,3	AFF1	410x190x730	40	SUPPORT POLE	22.64m	3
ALLOCATED	TEF	–	RFF1	400x240x700	45	THIRD FLOOR	20.70m	12
ALLOCATED	TEF	–	RFF2	400x190x480	25	THIRD FLOOR	20.70m	3
ALLOCATED	TEF	–	DFF1	382x177	25	SUPPORT POLE	18.60m	1

ANCILLARY RF EQUIPMENT (COMBINER/BBU/MHA/FILTER/GPS)

STATUS	OPERATOR	MANUFACTURER	MODEL	LOCATION	HEIGHT (C/L)	QUANTITY	COMMENTS
EXISTING	TEF	NOKIA	GPS MODULE	SUPPORT POLE	19.40m	1	REMAIN

ALL DIMENSIONS ARE IN mm UNLESS NOTED OTHERWISE

N.G.R E: 553884 N: 237653

REFER TO THE SITE SPECIFIC DRAWING SUBMISSION CHECKLIST (SDN0020) FOR A COMPREHENSIVE LIST AND INSTRUCTION ON WHERE TO FIND ALL ACCOMPANYING DESIGN DOCUMENTATION.

DESIGN DEPENDENCIES		COMPLETED
IBD	✓	17.09.2025
PANs	✓	20.08.2025
DRA	✓	21.10.2025
RADAR SCAN	✓	XX.XX.XXXX
GDC	✓	XX.XX.XXXX
ELECTRICAL CALCS	✓	XX.XX.XXXX
TRIAL HOLE	✓	XX.XX.XXXX
DNO QUOTE	✓	XX.XX.XXXX

REV	MODIFICATION	BY	CH	DATE
1A	PLANNING ISSUE	VW	RF	21.10.25

circet UK
Unit 27F-G, Hartlebury Trading Estate, Crown Lane, Hartlebury, Worcestershire, DY10 4JD

cornerstone

Cell Name	Opt.
SAFFRON WALDEN TOWER	–

Cell ID No

CSID	– TEF	– VF
111051	8233	75548
Project No.	– TM Cell ID	– N/A
147	–	–

Site Address / Contact Details

FRIENDS OF SCHOOL WATER TOWER MOUNT
PLEASANT ROAD
SAFFRON WALDEN
ESSEX
CB11 4GA

Drawing Title: TEF EQUIPMENT SCHEDULES

Purpose of issue: PLANNING — Dwg Rev: 1A

Drawing Number: 570

Surveyed By: CIRCET — Original Sheet Size: A3 — Pack Issue: 1A

Drawn:	Date:	Checked:	Date:
VW	21.10.25	RF	21.10.25