TASK	Roof scan
CLIENT	Jet NSL
PREPARED BY	Ayodele Fajuyigbe
SITE NAME	Saffron Walden Tower
DATE	29th of October 2026


KA ENGINEERING GROUP

CHECKLIST	
Description	Actioned
Roof Scan Sector (All sectors)	✓
Plinth Scan Sector (All sectors)	N/A
Beam Scan Sector (All sectors)	N/A
Column Scan Sector (All sectors)	N/A
Roof Support Layout (All sectors)	✓
Sketch of equipment position externally (All sectors)	N/A
Roof Thickness (All sectors)	✓
Plant Room Wall Thickness	N/A
Plant Room Brick Size	N/A
Plant Room layout	N/A
	✓
External photos of main building (4 faces)	✓
External main roof photos (All sectors)	✓
Internal photos (All sectors)	✓
External photographs of plant room (4 faces)	N/A
Internal photos of plant room (4 faces)	N/A
Load path photo	✓
Photo of survey equipment	N/A

Notes

① N/S Ramp Roof Support

② E/w Ramp Roof Support

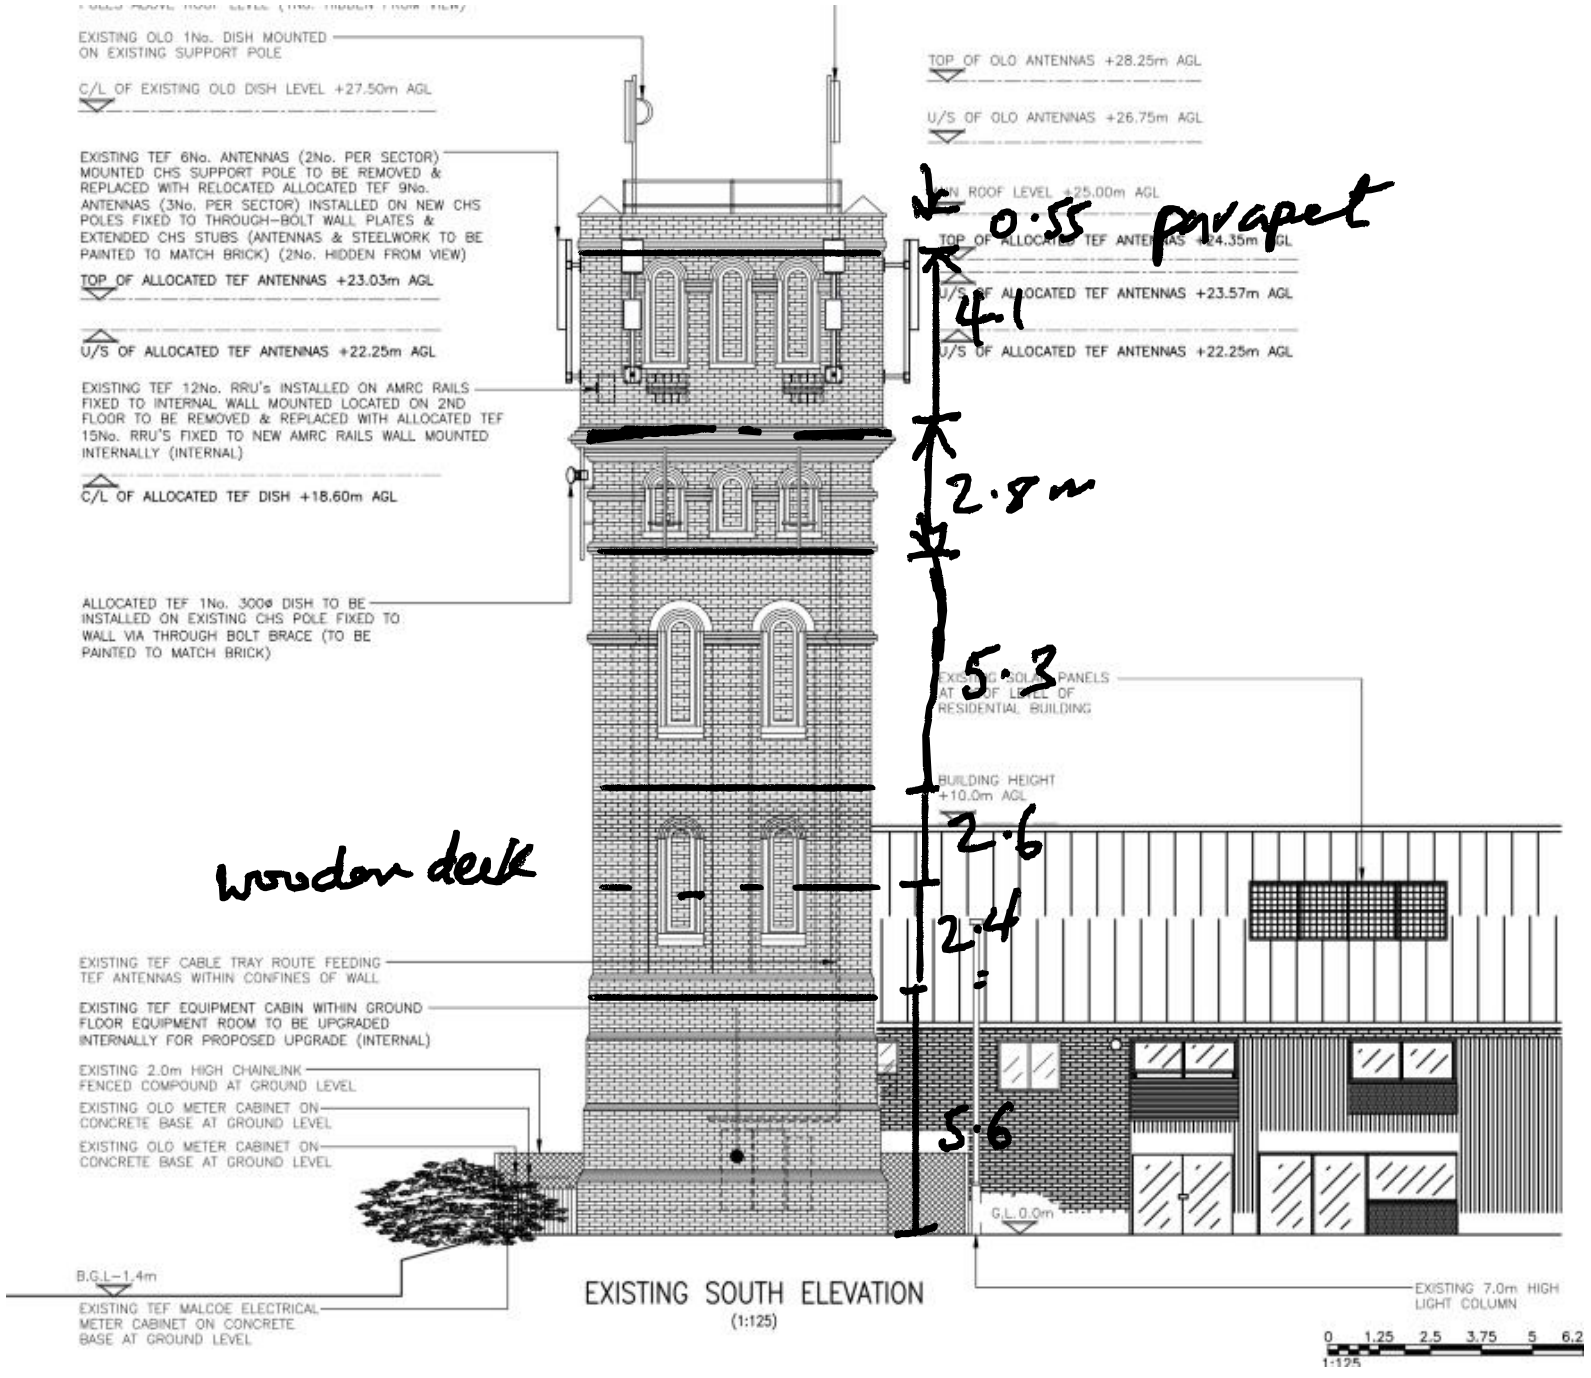


EXISTING SOUTH ELEVATION
(1:125)

Slab thickness - 175mm


— Concrete slab

— - — Steel floor — Primary beam E/W 510 x 190 x 20mm

Height dimensions are from floor to ceiling

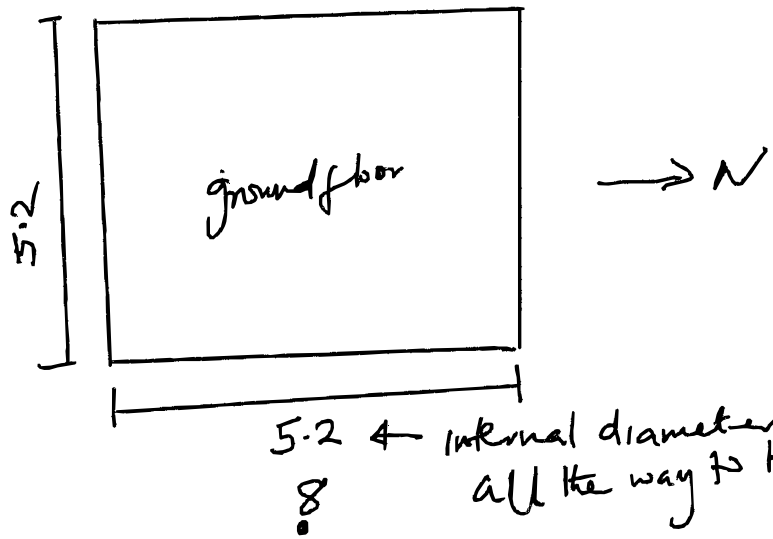
ground floor
N
5.2
5.2 ← internal diameter
all the way to the top
150
150
150
300
20 brick
20 brick
20 bricks
2.0m

Fourth Floor

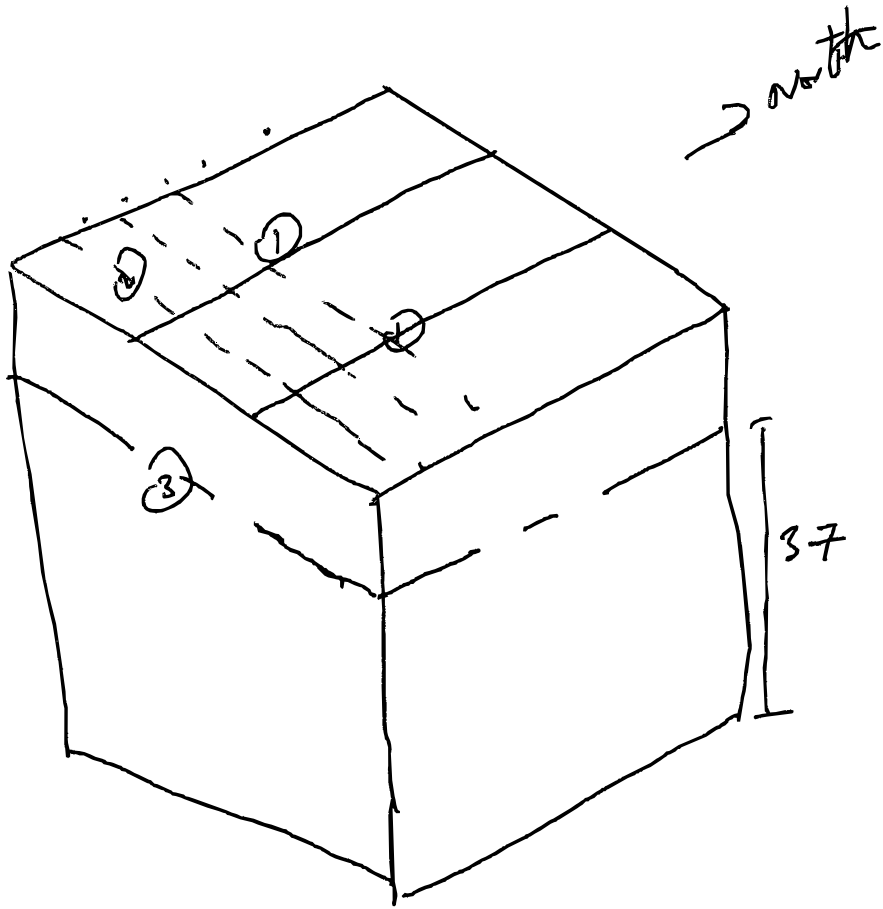

① 152 x 125 x 9mm

② 8 No bays Embedded beams – 850mm c/c

③ Height of internal steel wall